



BONFIRE HOUSE
BID SET
10/20/2021

LOCATION MAP

SHEET LIST

1 GENERAL	
G0.01	SYMBOLS AND ABBREVIATIONS
G0.11	CODE SUMMARY
G1.00	3D VIEWS
2 ARCHITECTURAL	
A1.00	SURVEY
A1.01	PLAN, SITE
A2.00	PLAN, FLOOR - CRAWL SPACE
A2.01	PLAN, FLOOR - LEVEL 1
A2.01A	PLANS, ENLARGED SOUTH
A2.01B	PLANS, ENLARGED NORTH
A2.02	PLAN, LEVEL 2
A2.03	PLAN, ROOF
A3.01	ELEVATIONS, EXTERIOR, EAST & WEST
A3.02	ELEVATIONS, EXTERIOR, NORTH & SOUTH
A3.03	ELEVATIONS, EXTERIOR, PARTIAL
A3.10	SECTIONS, BUILDING
A3.20	SECTIONS, WALL AND ENLARGED ELEVATIONS
A3.21	SECTIONS, WALL AND ENLARGED ELEVATIONS
A3.22	SECTIONS, WALL AND ENLARGED ELEVATIONS
A4.00	WALL ASSEMBLIES
A4.01	HORIZONTAL ASSEMBLIES
A4.10	DETAILS, EXTERIOR
A4.11	DETAILS, EXTERIOR
A4.12	DETAILS, EXTERIOR
A4.13	DETAILS, EXTERIOR
A5.01	ENLARGED PLAN, DECK
A5.10	ELEVATIONS, DECK
A5.11	SECTIONS, DECK
A5.30	DETAILS, DECK
A6.01	PLAN, REFLECTED CEILING
A7.01	ELEVATIONS, INTERIOR
A7.02	ELEVATIONS, INTERIOR
A7.10	DETAILS, INTERIOR
A8.01	DOOR AND WINDOW SCHEDULES

DIRECTORY

<u>Owner</u>	<u>Architect</u>	<u>Structural Engineer</u>
	Ben Feicht	

ABBREVIATIONS

& AND
@ AT
ADJ ADJACENT
AESS ARCHITECTURAL EXPOSED STRUCTURAL STEEL
AFF ABOVE FINISH FLOOR
ALUM ALUMINUM
APPROX APPROXIMATELY
ARCH ARCHITECTURAL

BD BOARD
BLDG BUILDING
B.O. BOTTOM OF

CL CENTERLINE
CF/OI CONTRACTOR FURNISHED / OWNER INSTALLED
CJ CONTROL JOINT
CLG CEILING
CLR CLEAR
CG CORNER GUARD
CMU CONCRETE MASONRY UNIT
COL COLUMN
CONC CONCRETE
CONT CONTINUOUS
COORD COORDINATE
CUH CABINET UNIT HEATER

DET DETAIL
DF DRINKING FOUNTAIN
DIA DIAMETER
DIM DIMENSION
DN DOWN
DWG DRAWING

EA EACH
EL ELEVATION
ELEC ELECTRICAL
EJ EXPANSION JOINT
ELEV ELEVATOR
EQ EQUAL
EQUIP EQUIPMENT
EXIST EXISTING
EXT EXTERIOR

FD FLOOR DRAIN
FE FIRE EXTINGUISHER
FEC FIRE EXTINGUISHER CABINET
FF FINISH FLOOR
FHC FIRE HOSE CABINET
FIN FINISH
FLR FLOOR
F.O. FACE OF
FT FEET/FOOT

GA GAUGE
GALV GALVANIZED
GL GLAZING
GYP GYPSUM

HM HOLLOW METAL
HORIZ HORIZONTAL
HR HOUR
HT HEIGHT

INCL INCLUDED
INSUL INSULATION
INT INTERIOR

JT JOINT

LAV LAVATORY

MAX MAXIMUM
MECH MECHANICAL
MFR MANUFACTURER
MIN MINIMUM
MISC MISCELLANEOUS
MO MASONRY OPENING
MTD MOUNTED
MTL METAL

NIC NOT IN CONTRACT
NO NUMBER
NOM NOMINAL
NTS NOT TO SCALE

OC ON CENTER
OD OVERFLOW DRAIN
OF/CI OWNER FURNISHED / CONTRACTOR INSTALLED
OF/OI OWNER FURNISHED / OWNER INSTALLED
OH OVERHEAD
OPP OPPOSITE

PTD PAINTED

R RADIUS
RCP REFLECTED CEILING PLAN
RD ROOF DRAIN
REINF REINFORCING
REQD REQUIRED
RM ROOM
RO ROUGH OPENING

SCHED SCHEDULE
SF SQUARE FOOT
SIM SIMILAR
SPEC SPECIFICATIONS
SQ SQUARE
SS STAINLESS STEEL
STL STEEL
STRUCT STRUCTURAL





















T.O. TOP OF
TYP TYPICAL

UNO UNLESS NOTED OTHERWISE
UL UNDERWRITERS LABORATORIES

VERT VERTICAL
VIF VERIFY IN FIELD

W/ WITH
W/O WITHOUT
WD WOOD

MATERIALS

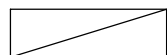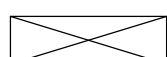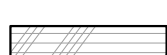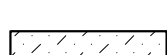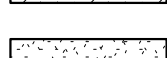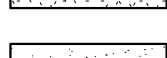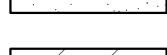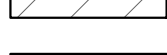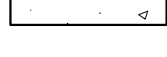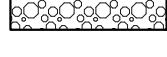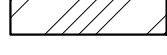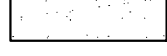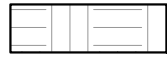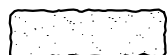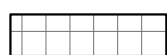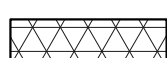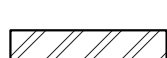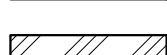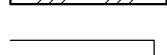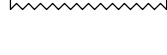-  WOOD SHIM
-  CONTINUOUS WOOD BLOCKING
-  WOOD, FINISH OR TRIM
-  PLYWOOD
-  HARDBOARD
-  GYPSUM WALLBOARD
-  CONCRETE, PRECAST
-  CONCRETE, MASONRY
-  CONCRETE, POURED
-  POROUS
-  RUBBER
-  SAND
-  STONE-SLAB
-  EARTH
-  FIREPROOFING
-  INSULATION, BATT
-  INSULATION, EXPANDED POLYSTYRENE
-  STEEL
-  ALUMINUM
-  SHEET METAL
-  HOLLOW METAL
-  ALUMINUM
-  METAL LATH AND PLASTER
-  GLAZING
-  CARPET

DIMENSIONING STANDARDS

EXTERIOR DIMENSIONS

1. BUILDING PLAN DIMENSIONS.

A. REFER TO 1/8" & 1/4" FLOOR PLANS IN A2.* SERIES FOR OVERALL BUILDING DIMENSIONS, AND DIMENSION POINTS TO MAJOR CONSTRUCTION TRANSITIONS OR OTHER PRIMARY ELEMENTS. IN SOME CASES ADDITIONAL DIMENSIONS MAY BE PROVIDED WHERE A TYPICAL CONDITION OCCURS, OR WHERE THERE IS NO 1/2" ENLARGED PLAN PROVIDED.

2. BUILDING FLOOR HEIGHT ELEVATIONS INDICATED IN PLAN, SECTION AND ELEVATION ARE BASED ON HEIGHT ABOVE LEVEL ONE. SITE VERIFY LEVEL ONE HEIGHT.

3. REFER TO 1/4" ELEVATIONS FOR TOP OF FRAMING (T.O.F) HEIGHT CONSTRUCTION.

4. REFER TO DETAILS IN A4.* SERIES FOR PLAN AND SECTION DETAIL DIMENSIONS.

INTERIOR DIMENSIONS

1. DO NOT SCALE DRAWINGS FOR DIMENSIONAL INFORMATION; ALL ELEMENTS ON THE DRAWINGS MAY NOT BE TO THE EXACT SCALE. ALL DIMENSIONS REQUIRED ARE SHOWN OR MAY BE DERIVED FROM THOSE SHOWN ON THE FLOOR PLANS, DETAIL PLANS, ELEVATIONS, SECTIONS, DETAILS, SCHEDULES AND SPECIFICATIONS.

2. REFER TO SYMBOLS ON THIS SHEET FOR ILLUSTRATIONS USED TO INDICATE "FACE OF" OR "CENTERLINE" DIMENSIONS.

3. EXCEPT WHERE SPECIFICALLY NOTED TO THE CONTRARY, ALL THE INTERIOR RELATED DIMENSIONS SHOWN ON THE ARCHITECTURAL DRAWINGS CONFORM TO THE FOLLOWING CONVENTIONS:

A. STUD AND CMU PARTITIONS AT GRID LINES ARE LOCATED WITH THE FACE OF FRAMING OF THE PARTITION ASSEMBLY AT THE GRID, UNLESS NOTED OTHERWISE.

B. DIMENSIONS SHOWN AND/OR NOTED TO THE CENTERLINE ARE MEASURED TO THE CENTERLINE OF DOORS, WINDOWS, OR OTHER FEATURES INDICATED.

C. WHERE "CLEAR" DIMENSIONS ARE SPECIFICALLY NOTED, THE DIMENSION INDICATED IS THE MINIMUM DIMENSION MEASURED TO FINISH FACES AT THE MOST CONSTRICTED POINTS WHERE THE DIMENSION IS SHOWN.


D. WHERE DIMENSIONS ARE NOT PROVIDED ON THE FLOOR PLANS TO LOCATE DOORS, REFER TO DETAILS ON SHEET **A8.01** IN ORDER TO DETERMINE THE LOCATION OF DOOR OPENINGS.

6. REFER TO ELEVATION SHEETS FOR MOUNTING HEIGHTS.


7. WHERE WALLS AND/OR PARTITIONS OF UNEQUAL THICKNESS ABUT, ALIGN EXPOSED FACES, UNO.

SYMBOLS


NORTH ARROW

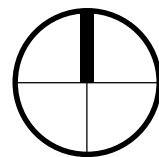


GRAPHIC SCALE

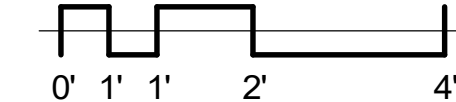


DRAWING TITLE

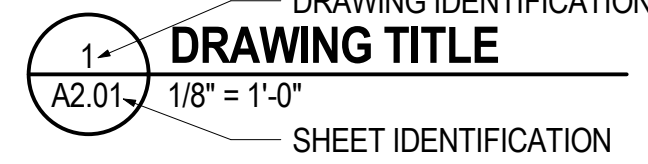

EXTERIOR ELEVATION

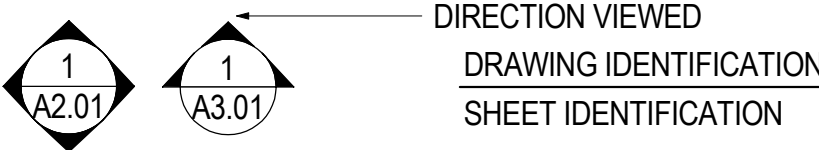


SECTION REFERENCE

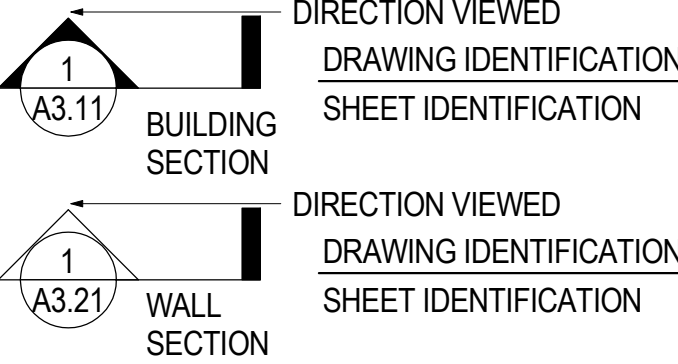


DETAIL REFERENCE




INTERIOR ELEVATION

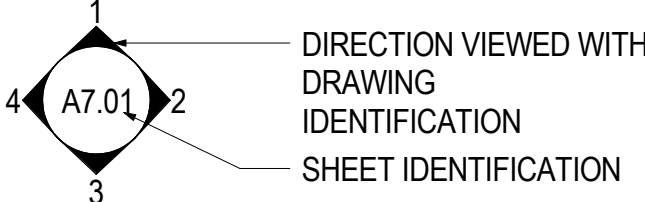

GRID REFERENCE

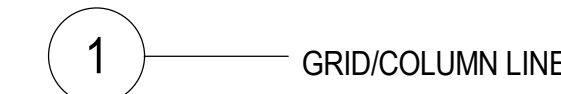


LEVEL DATUM

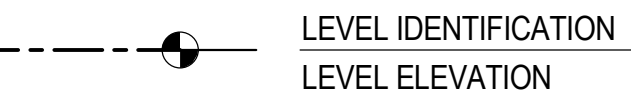

ROOM TAG



DOOR TAG

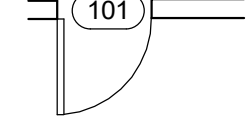

SEE DOOR AND RELITE TYPES AND DETAILS SHEET A8.01 DOOR SCHEDULES AND DATA IN SPECIFICATIONS DIV. 8

WALL ASSEMBLY TAG




WINDOW TYPE TAG



FLOOR ASSEMBLY TAG




REVISION TAG

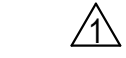

KEYNOTE



MATCH LINE

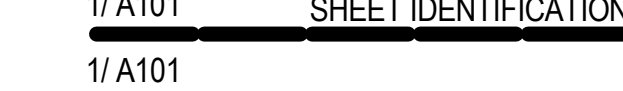


DIM PT.

DIMENSION TO FACE OF:


- FRAMING
- EDGE OF DOOR OPENING
- EDGE OF OTHER ASSEMBLY
- WORK POINT INDICATED ON DETAILS
- CENTERLINE AS SHOWN AND/OR WHERE NOTED
- GLASS

SPOT ELEVATION REFERENCE

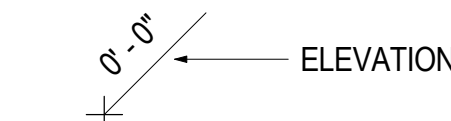

SHEET DESIGNATION LEGEND

A0.01

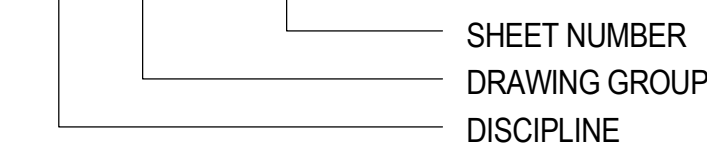

BEN FEICHT
ARCHITECT

SYMBOLS AND ABBREVIATIONS
BONFIRE HOUSE
BID SET

REVISIONS
Revision Date

JOB NO.
18
DATE
10/20/2021
DWG. NO.
G0.01

1	PROJECT DATA	4	ZONING
THE BUILDING IS A NEW CONSTRUCTION SINGLE FAMILY HOUSE (R-3 OCCUPANCY) LOCATED ON A YET UN-ADDRESSED PROPERTY. THE PARCEL IS ZONED RESIDENTIAL DISTRICT 1, CONSISTS OF 409,056 SF (9.39 ACRES). THE PROPOSED PROJECT ENCOMPASSES A FOUR BEDROOM TWO STORY BUILDING, WITH SITE WORK INCLUDING A WATER SUPPLY WELL, SEPTIC SYSTEM, AND POOL. PLANNING APPLICATION # _____ TOTAL AREA: 3840 SF HEATED AREA: 3270 SF UNCOVERED DECK AREA: 880 SF # OF STORIES: 2 BUILDING HEIGHT: 27' - 11" # BEDROOMS: 4 # BATHROOMS: 3.5		THE PROJECT IS CONSTRUCTION TYPE V-B WITH OCCUPANCY TYPE R-3 PER IBC, TABLE 503 THEREFORE IT WILL BE ALLOWED AN UNLIMITED BUILDING AREA PER STORY AND THREE STORIES ABOVE GRADE PLANE TO A MAX HEIGHT OF 40 FT. COUNTY ZONING: RESIDENTIAL DISTRICT 1 TOTAL SITE AREA: 409,056 SF (9.39 ACRES) RESIDENTIAL DISTRICT 1 MAX HEIGHT: 60 FT BUILDING SETBACKS: ALL SIDES: 50' FROM PROPERTY LINE <u>IMPERVIOUS AREA:</u> ROOF: 4000 SF DECK / POOL: 1500 SF PATH: 430 SF TOTAL: 5930 SF (1.5% OF TOTAL LOT AREA) DESIGN CRITERIA: STRUCTURAL: SEE STRUCTURAL DRAWINGS ENERGY: PRESCRIPTIVE - CLIMATE ZONE 4A	
2	APPLICABLE CODES	5	PLUMBING:
JURISDICTIONAL AUTHORITY: CHATHAM COUNTY, BUILDING INSPECTORS AND CENTRAL PERMITTING (CHATHAM COUNTY, NC) FEDERAL REGULATIONS U.S. ENVIRONMENTAL PROTECTION AGENCY REGULATIONS (EPA) BUILDING CODE: 2018 NORTH CAROLINA RESIDENTIAL CODE (ADOPTS THE IRC 2015 WITH AMENDMENTS)		FIXTURE COUNT: TOILETS: 4 LAVATORIES: 4 KITCHEN SINKS: 1 SHOWERS: 3 TUB: 1 DISHWASHER: 1 LAUNDRY WASHER: 1 HOSE BIBS: 5	
3	OCCUPANCY CLASSIFICATION AND CONSTRUCTION TYPE	6	ENERGY CODE COMPLIANCE:
OCCUPANCY CLASSIFICATION: R-3 CONSTRUCTION TYPE: V-B ▪ PRIMARY STRUCTURAL FRAME 0 HR ▪ BEARING WALLS: EXTERIOR 0 HR ▪ NON-BEARING EXTERIOR WALLS 0 HR ▪ NON-BEARING INTERIOR WALLS 0 HR ▪ FLOOR CONSTRUCTION 0 HR ▪ ROOF CONSTRUCTION 0 HR		ENERGY CODE: 2018 NORTH CAROLINA RESIDENTIAL CODE (ADOPTS THE IRC 2015 WITH AMENDMENTS) PER TABLE N1102.1.2: INSULATION AND FENESTRATION REQUIREMENTS BY COMPONENT: WINDOWS/ DOORS U = .35, SHGC = .3 CEILING R = 38 WOOD FRAME WALL R = 15 (CAVITY) / R = 13+2.5 (CAVITY+CONTINUOUS) CRAWL SPACE WALL R = 10 (INTERIOR) / 15 (EXTERIOR) PROJECT INSULATION VALUES: PICTURE WINDOWS U = .31, SHGC = .23 CASEMENT WINDOWS U = .32, SHGC = .20 EXTERIOR DOORS U = .35, SHGC = .3 CEILING R = 53 WOOD FRAME WALL R = 21 + 6 (CAVITY+CONTINUOUS) CRAWL SPACE WALL R = 10 (INTERIOR)	

BEN FEICHT ARCHITECT	CODE SUMMARY		REVISIONS	JOB NO. 18
	BONFIRE HOUSE			DATE 10/20/2021
	BID SET			DWG. NO. G0.11



3D VIEW - EAST FACADE



3D VIEW - WEST FACADE




3D VIEW - KITCHEN




3D VIEW - ENTRY


(SURVEY REMOVED FOR THIS REVIEW)			
BEN FEICHT ARCHITECT	SURVEY BONFIRE HOUSE BID SET		REVISIONS
			△ Revision Date
			DATE 10/20/2021 DWG. NO. A1.00

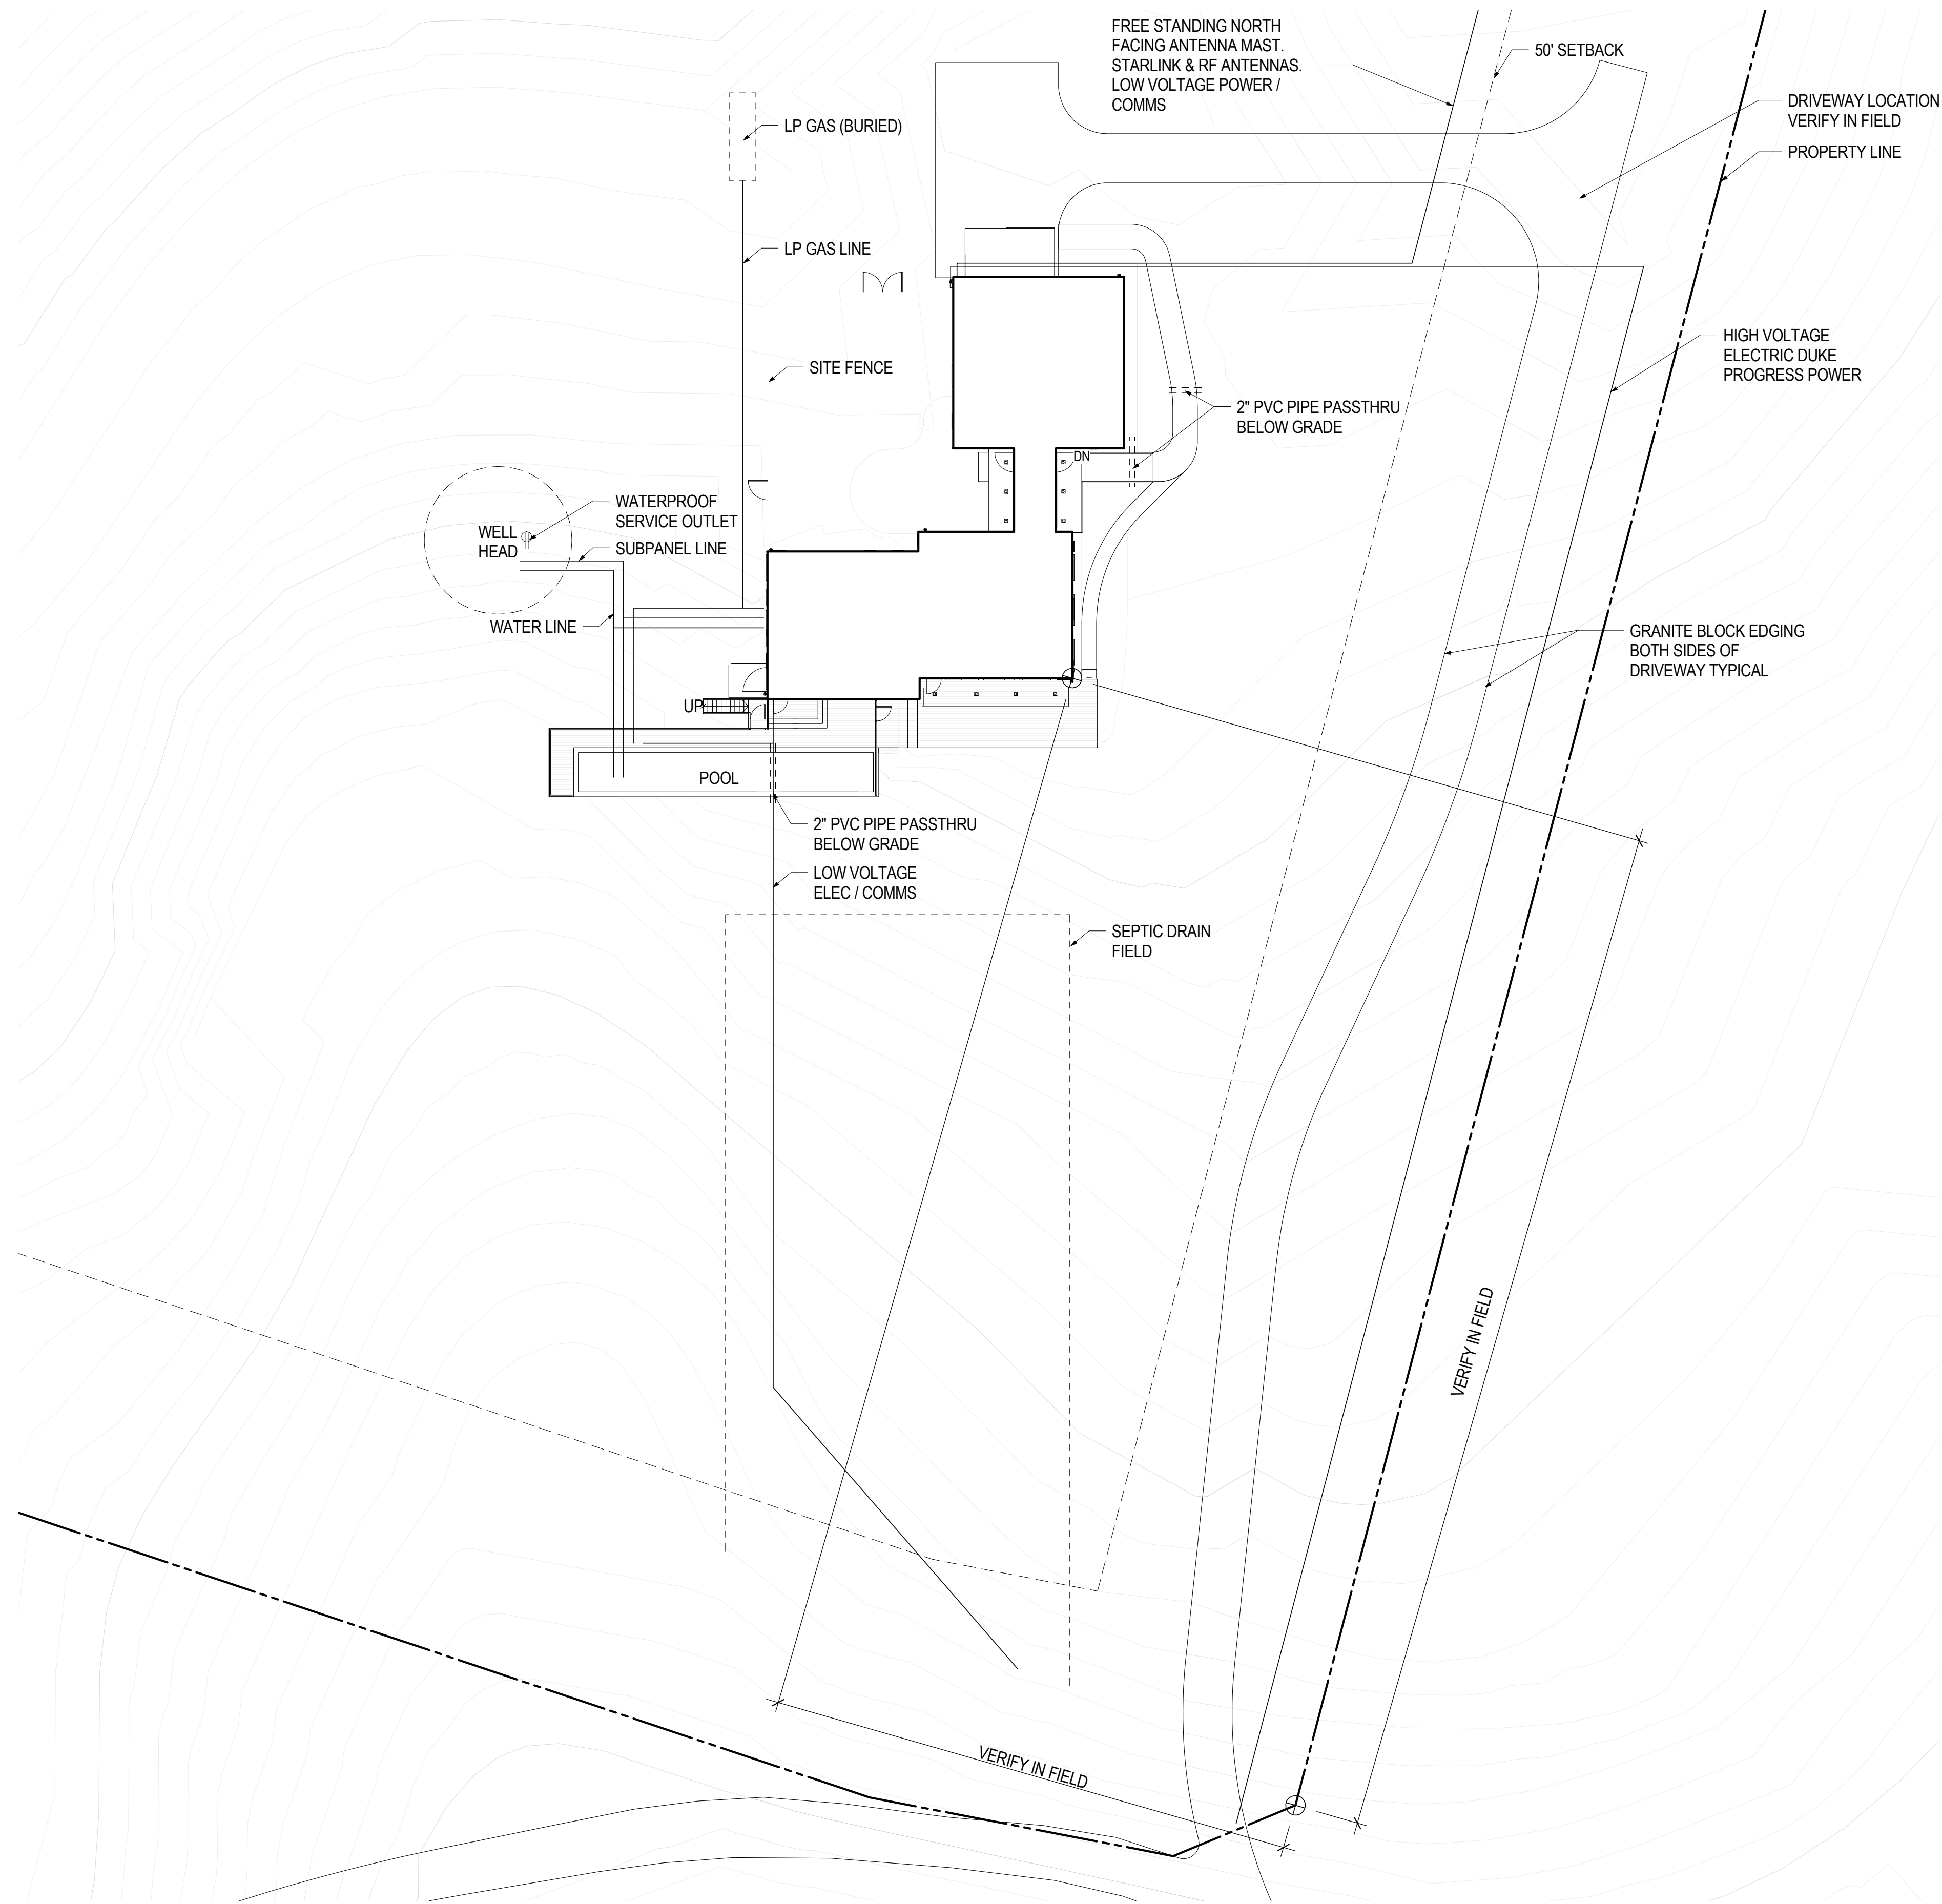

1 SITE PLAN
A1.01 1" = 20'-0"

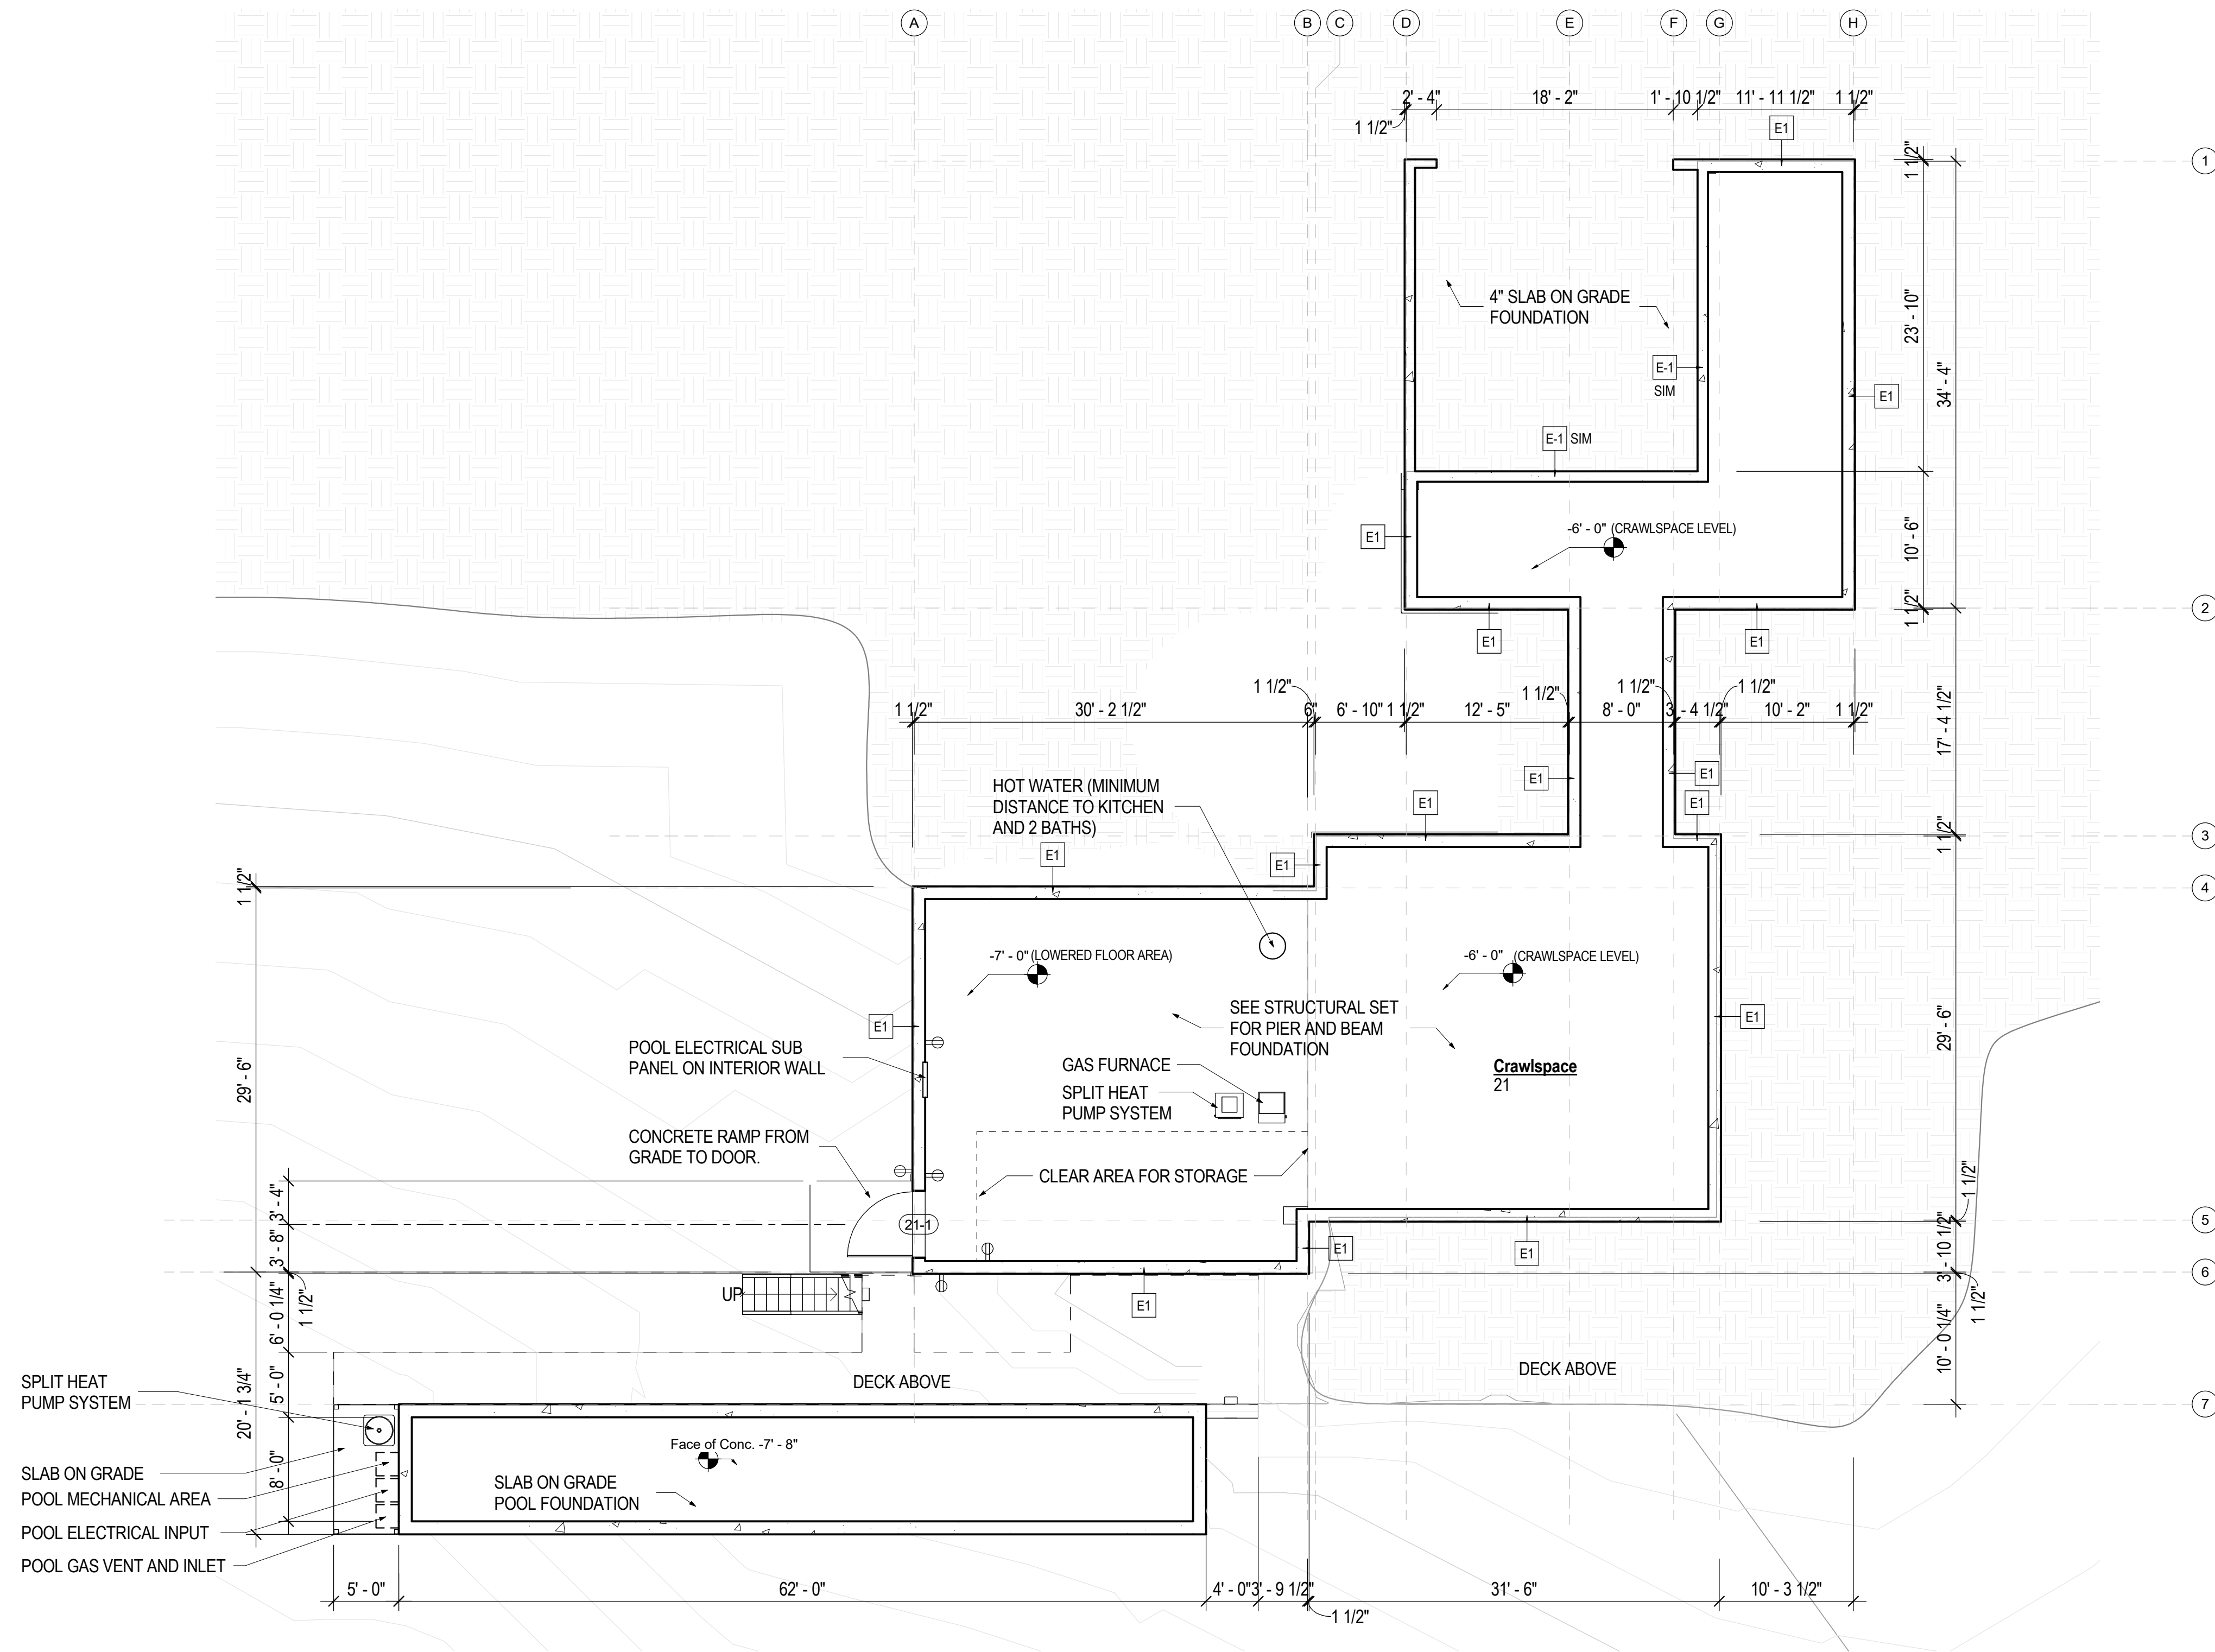



1 PLAN, CRAWL SPACE
A2.00 1/8" = 1'-0"

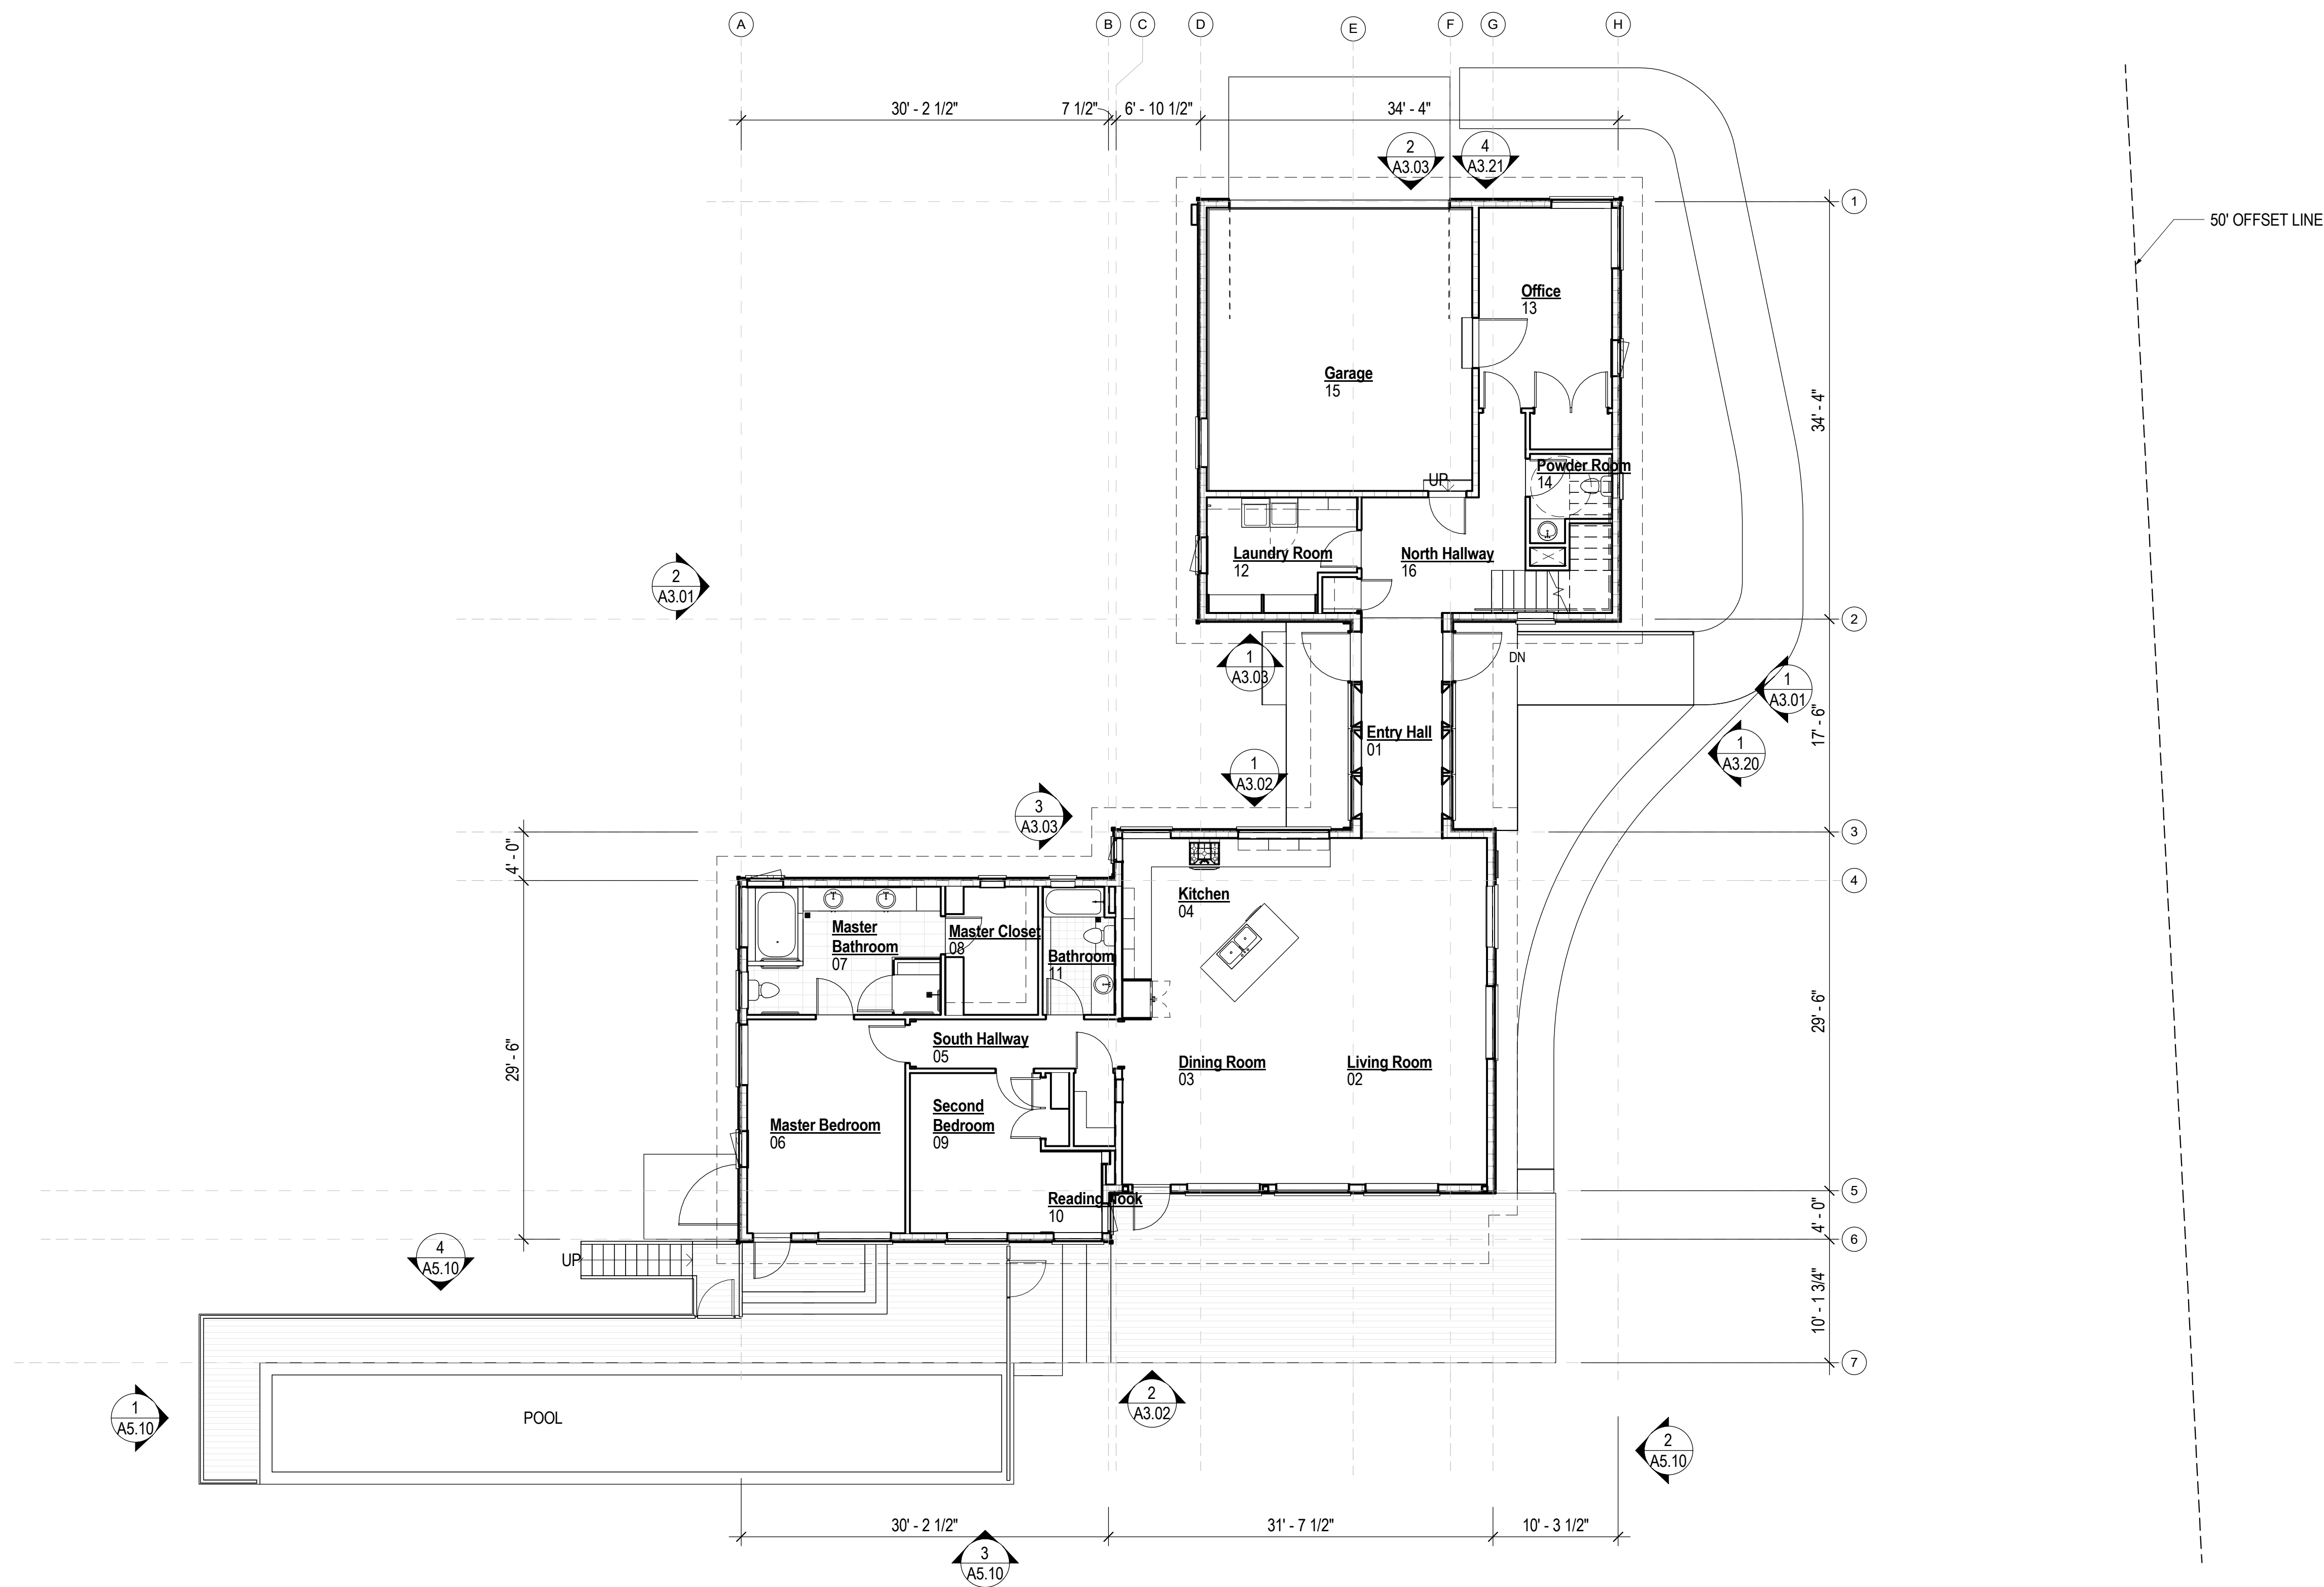

1 PLAN, LEVEL 1
A2.01 1/8" = 1'-0"


BEN FEICHT
ARCHITECT

PLAN, FLOOR - LEVEL 1
BONFIRE HOUSE
BID SET

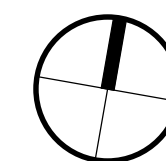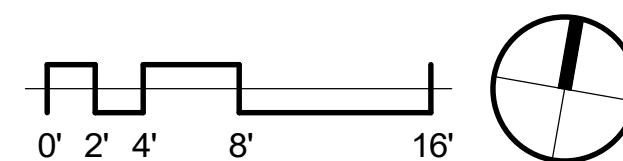


REVISIONS
Revision Date

JOB NO.
18
DATE
10/20/2021
DWG. NO.
A2.01

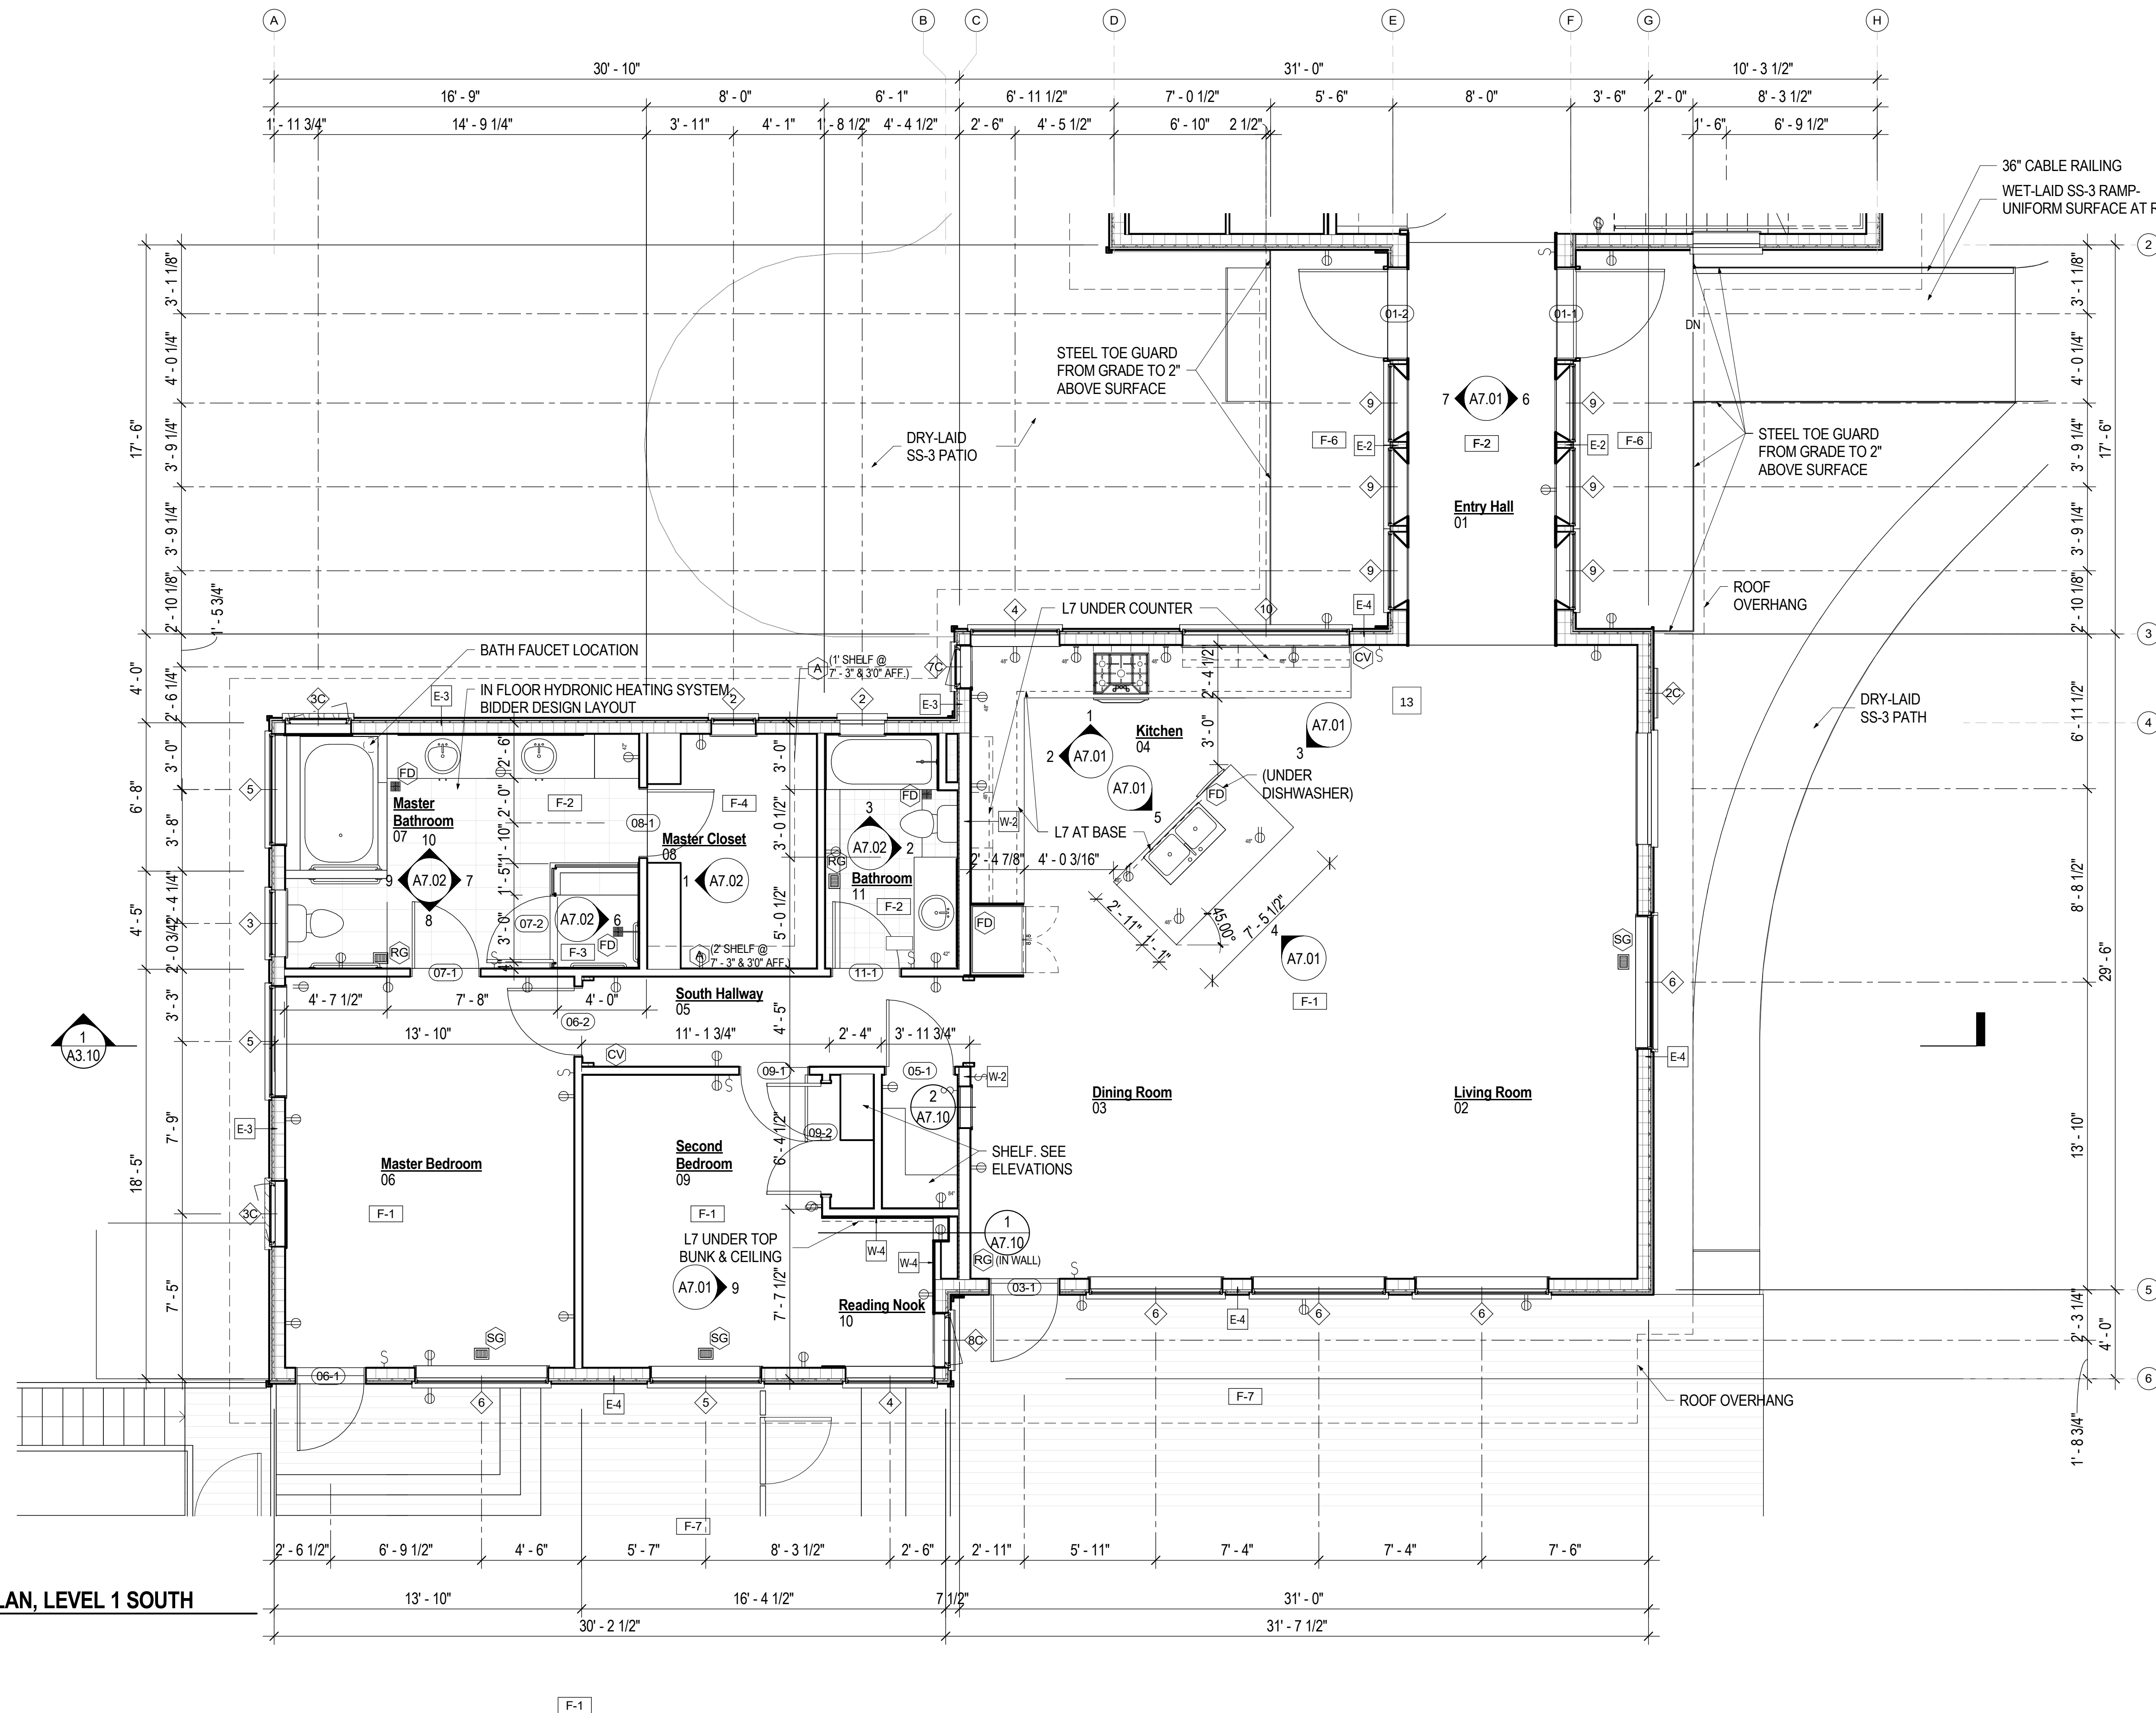


KEYNOTES	
	FLOOR DRAIN
	RETURN GRILLE
	FLUSH IN FLOOR WOOD SUPPLY GRILLE - MATCH FLOORING
	CENTRAL VACUUM SYSTEM WALL FIXTURE
	18" SHELF & 12" POLE AT 6'0" AFF. UNLESS OTHERWISE NOTED.
NOTES	
1. W1 TYPICAL INTERIOR WALL TYPE UNLESS OTHERWISE NOTED.	

1 ENLARGED PLAN, LEVEL 1 SOUTH
A2.01A 1/4" = 1'-0"

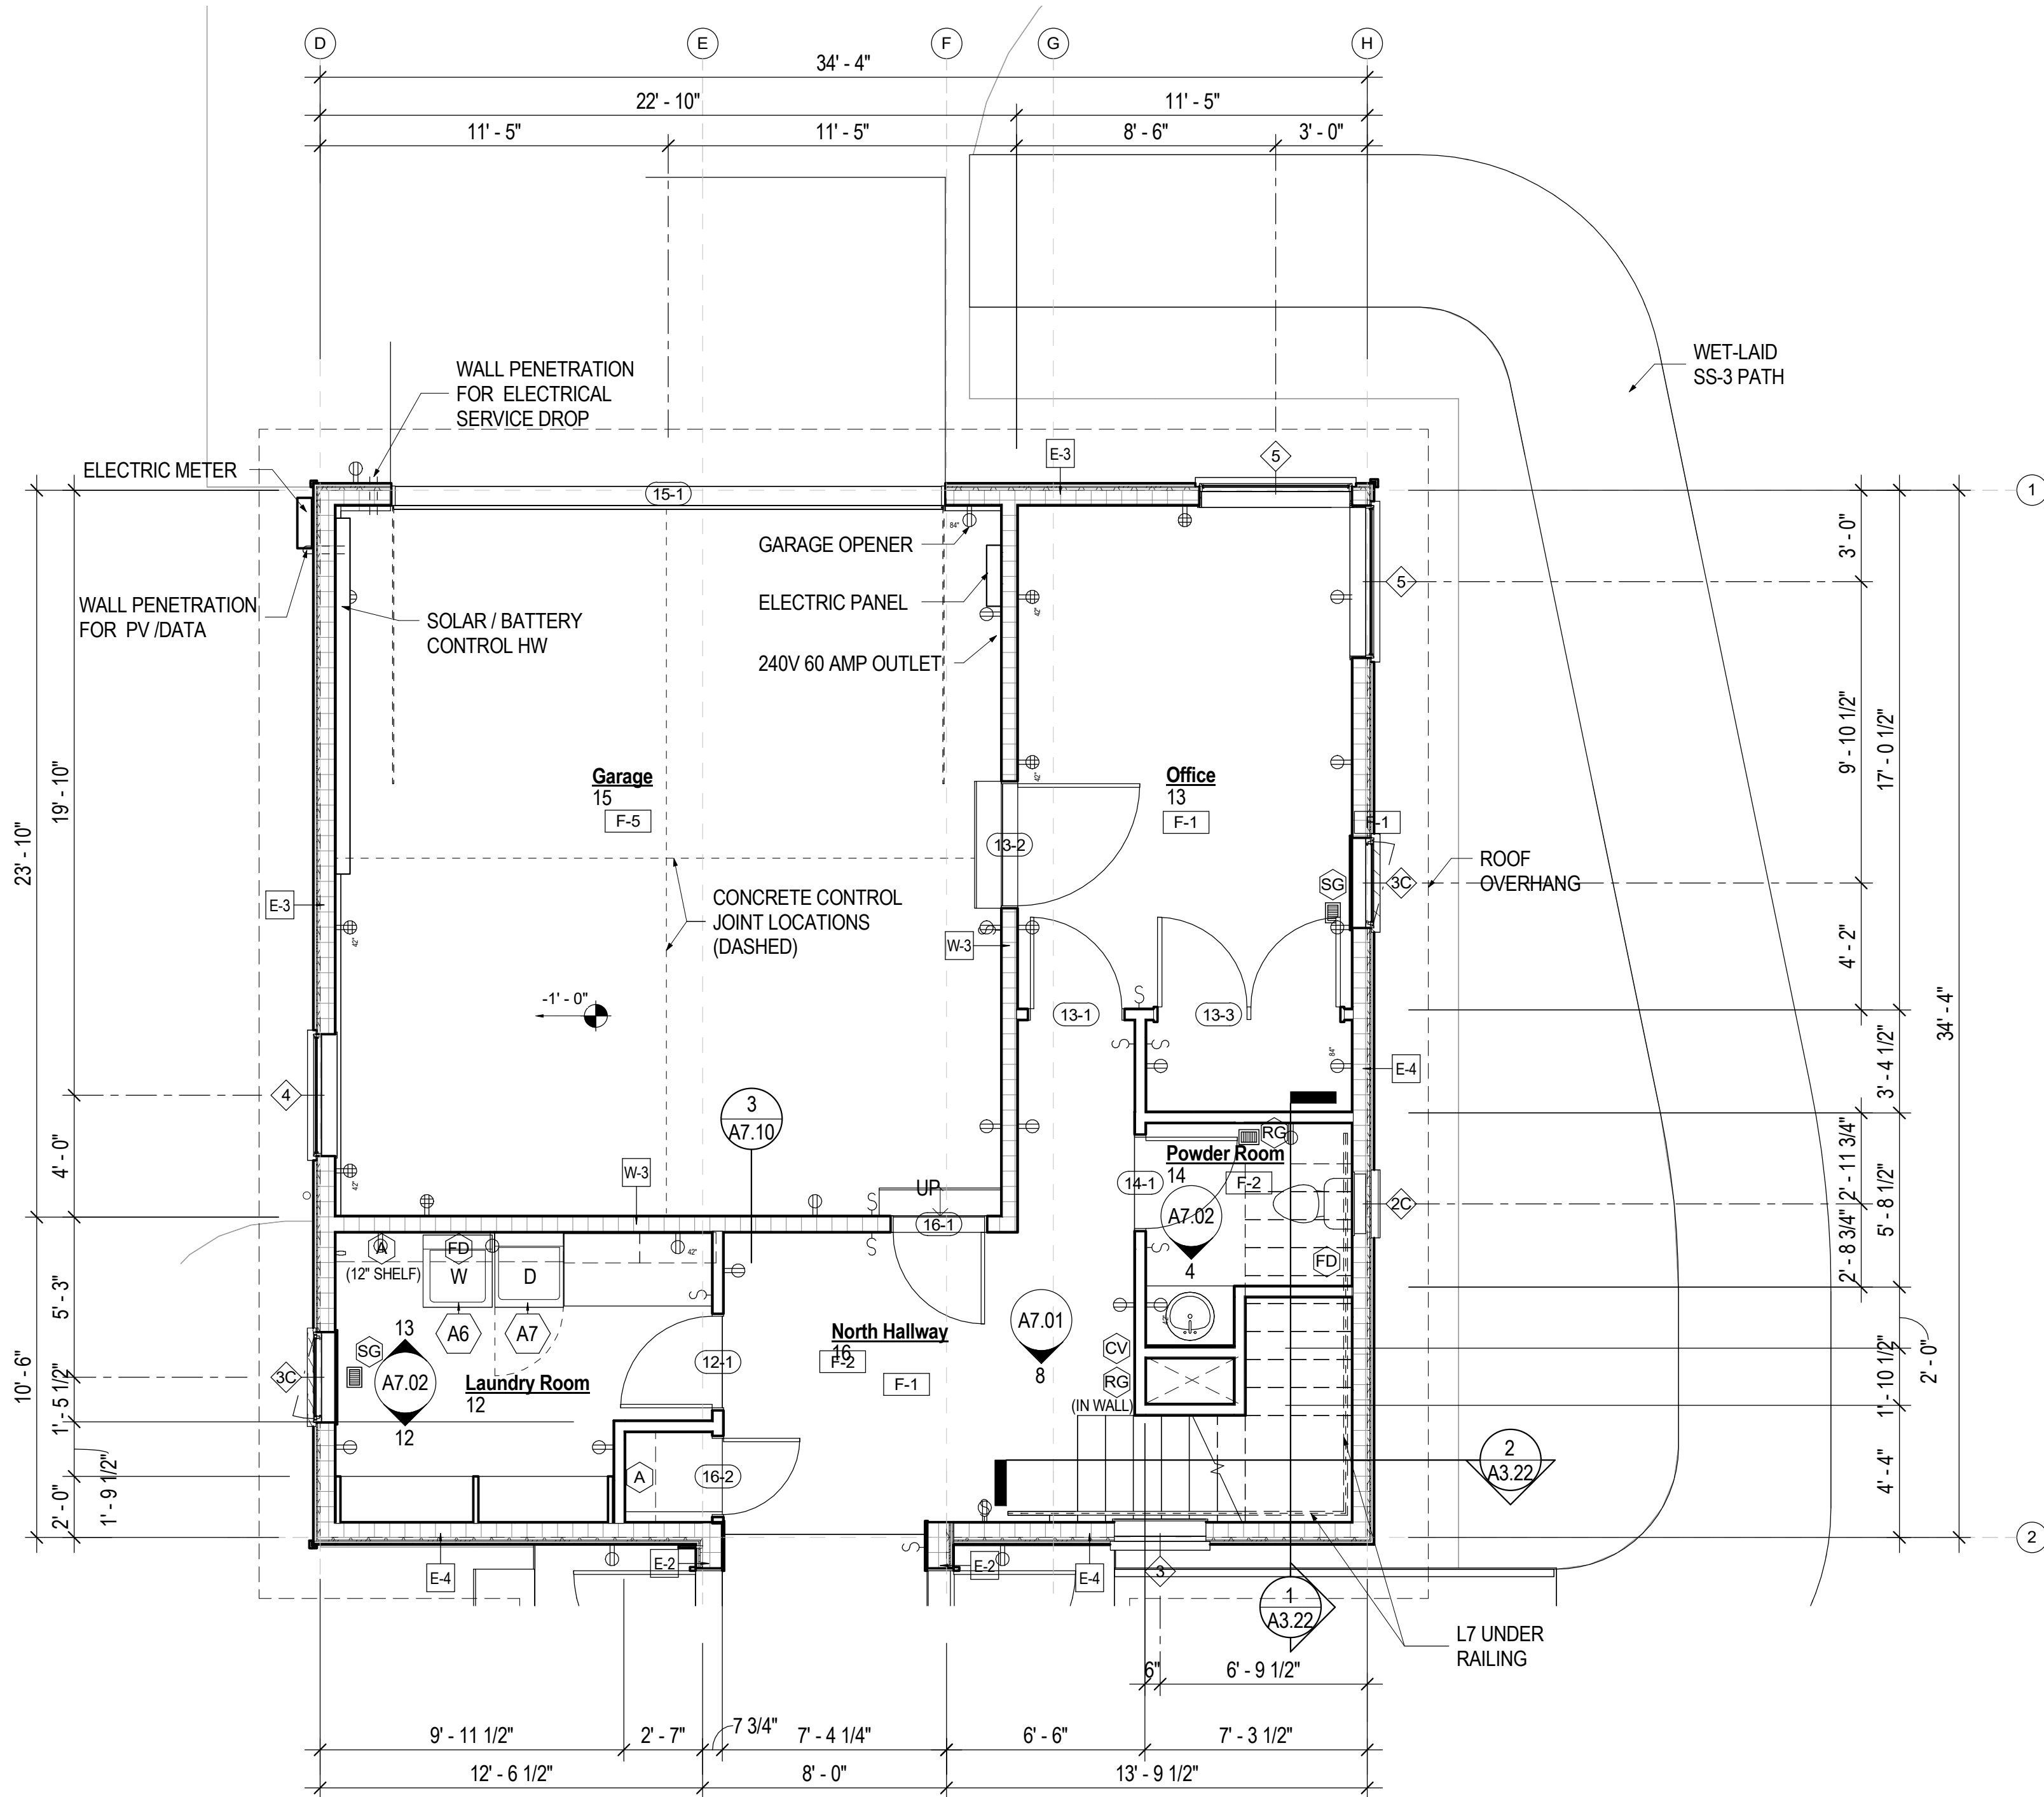



1 ENLARGED PLAN, LEVEL 1 NORTH
A2.01B 1/4" = 1'-0"

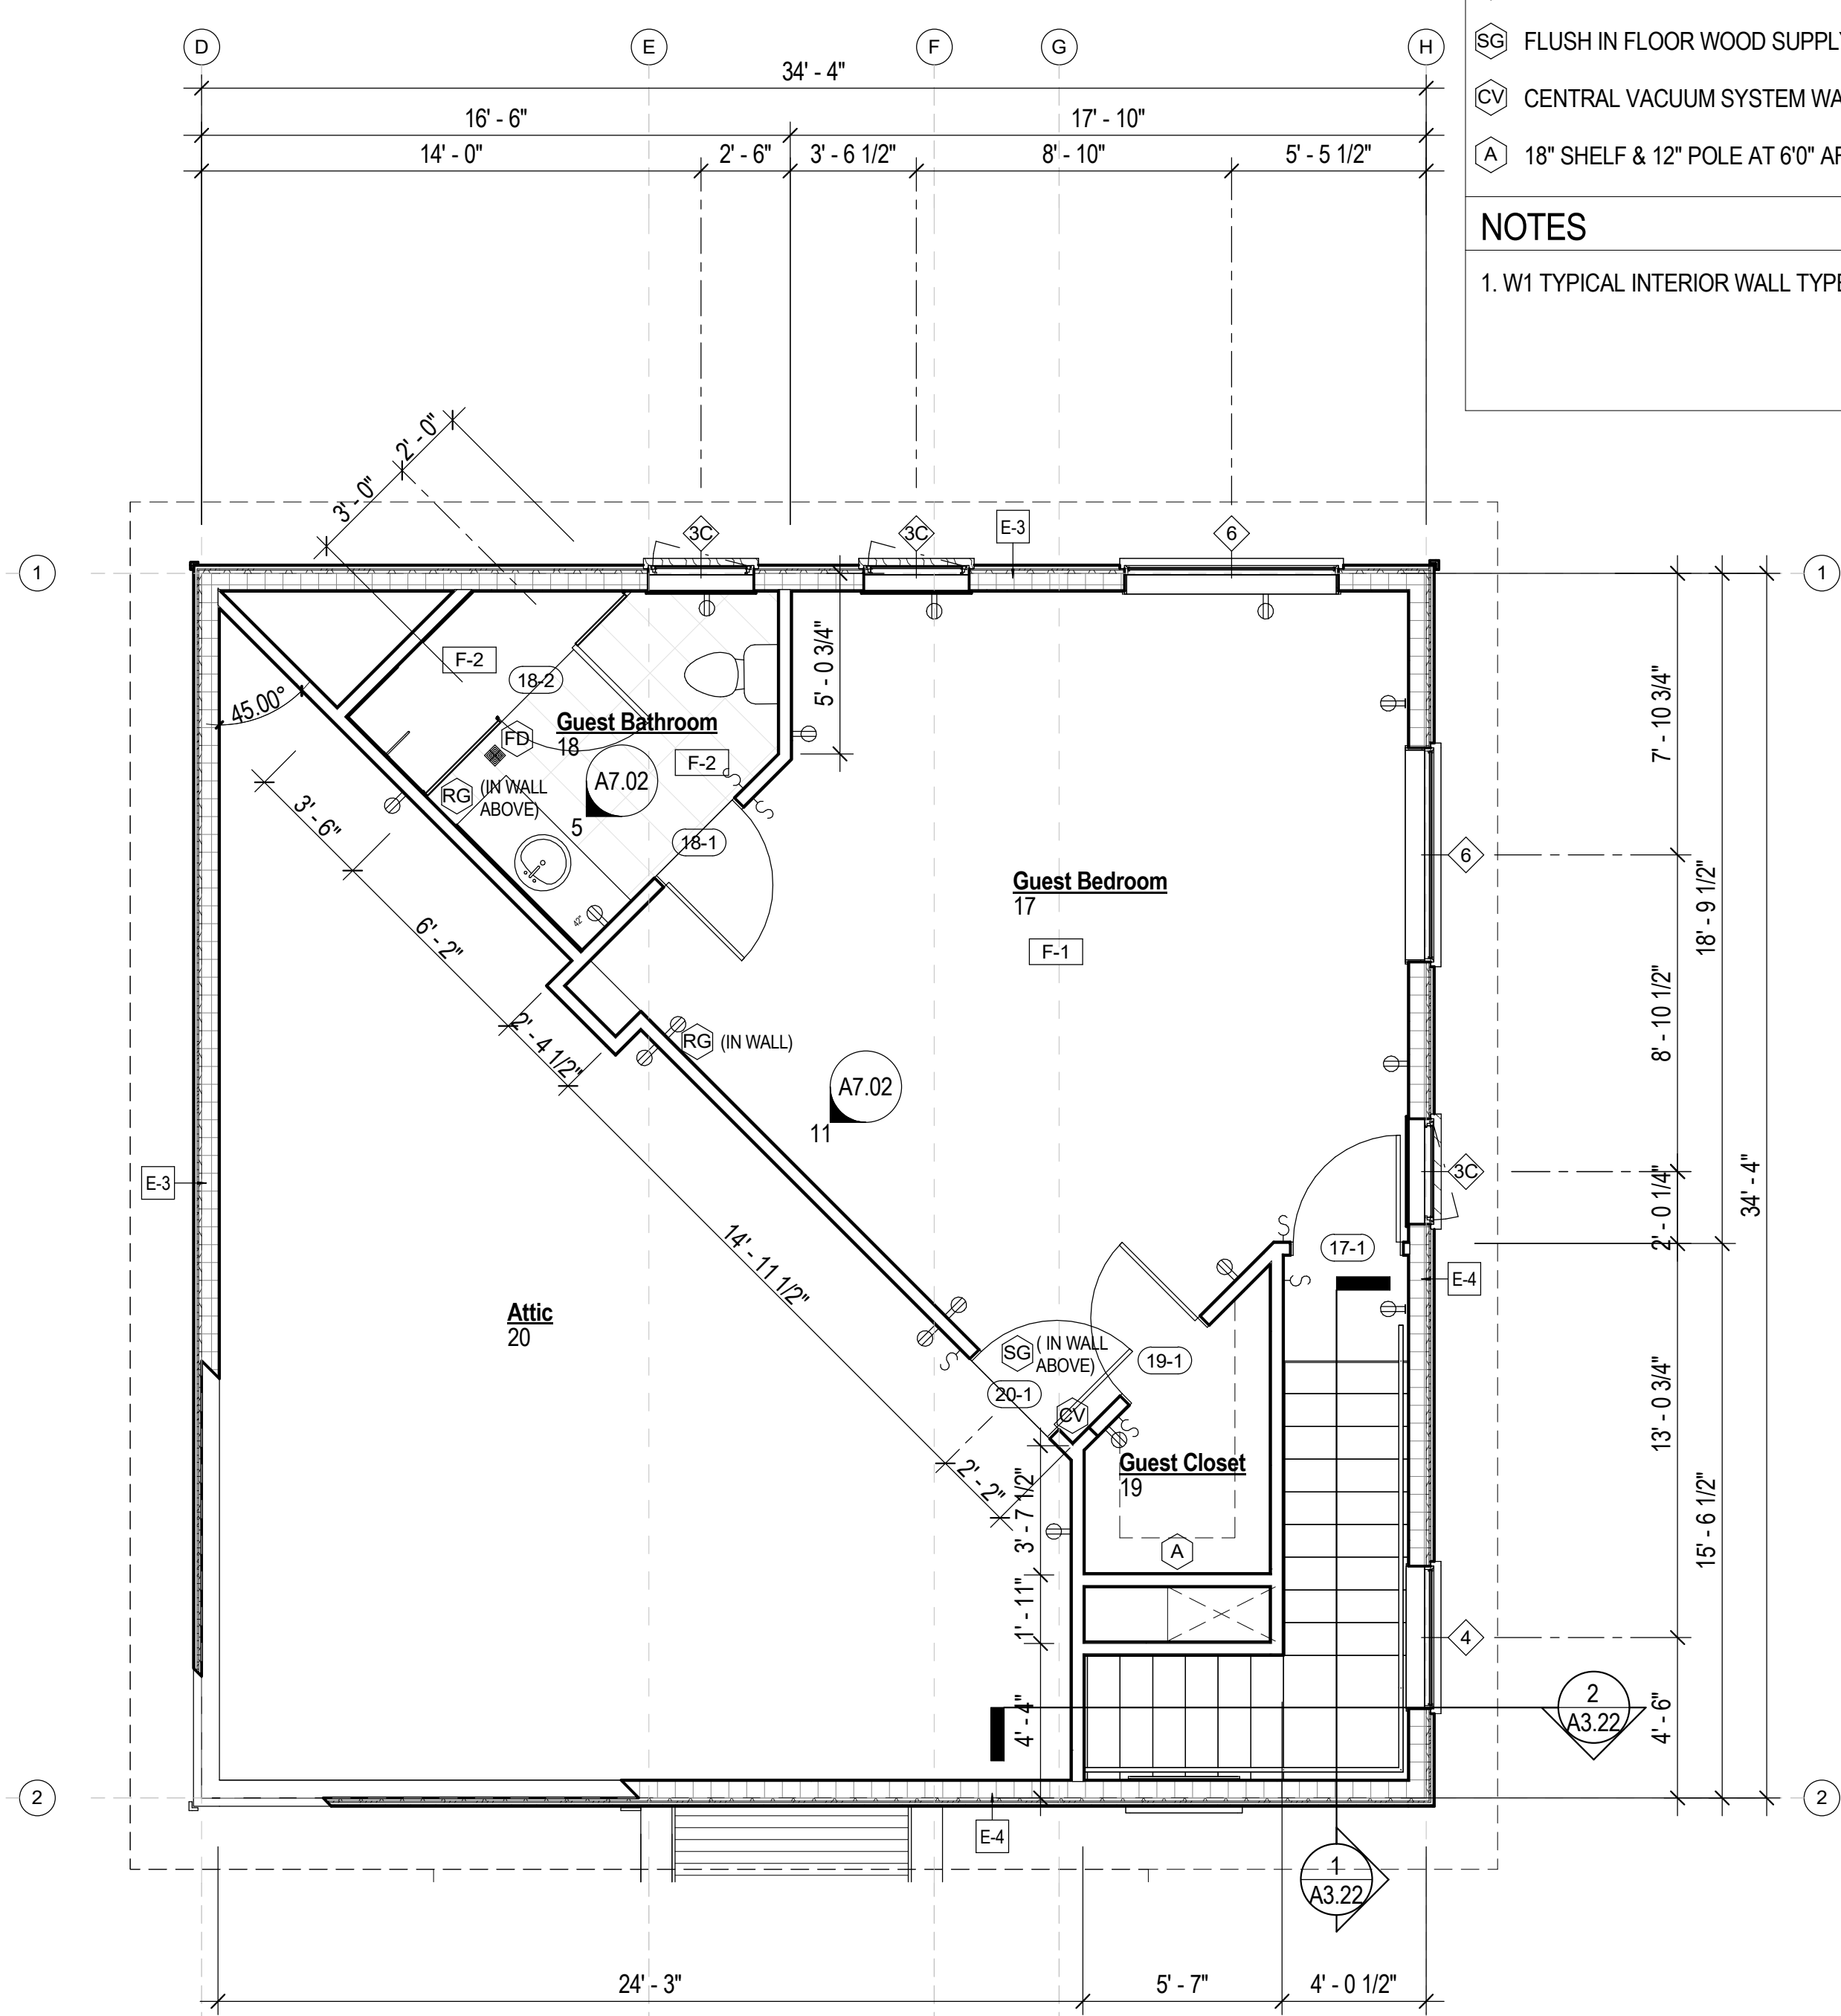

2 ENLARGED PLAN, LEVEL 2 NORTH
A2.01B 1/4" = 1'-0"


KEYNOTES	
	FLOOR DRAIN
	RETURN GRILLE
	FLUSH IN FLOOR WOOD SUPPLY GRILLE - MATCH FLOORING
	CENTRAL VACUUM SYSTEM WALL FIXTURE
	18" SHELF & 12" POLE AT 6'0" AFF. UNLESS OTHERWISE NOTED.
NOTES	
1. W1 TYPICAL INTERIOR WALL TYPE UNLESS OTHERWISE NOTED.	

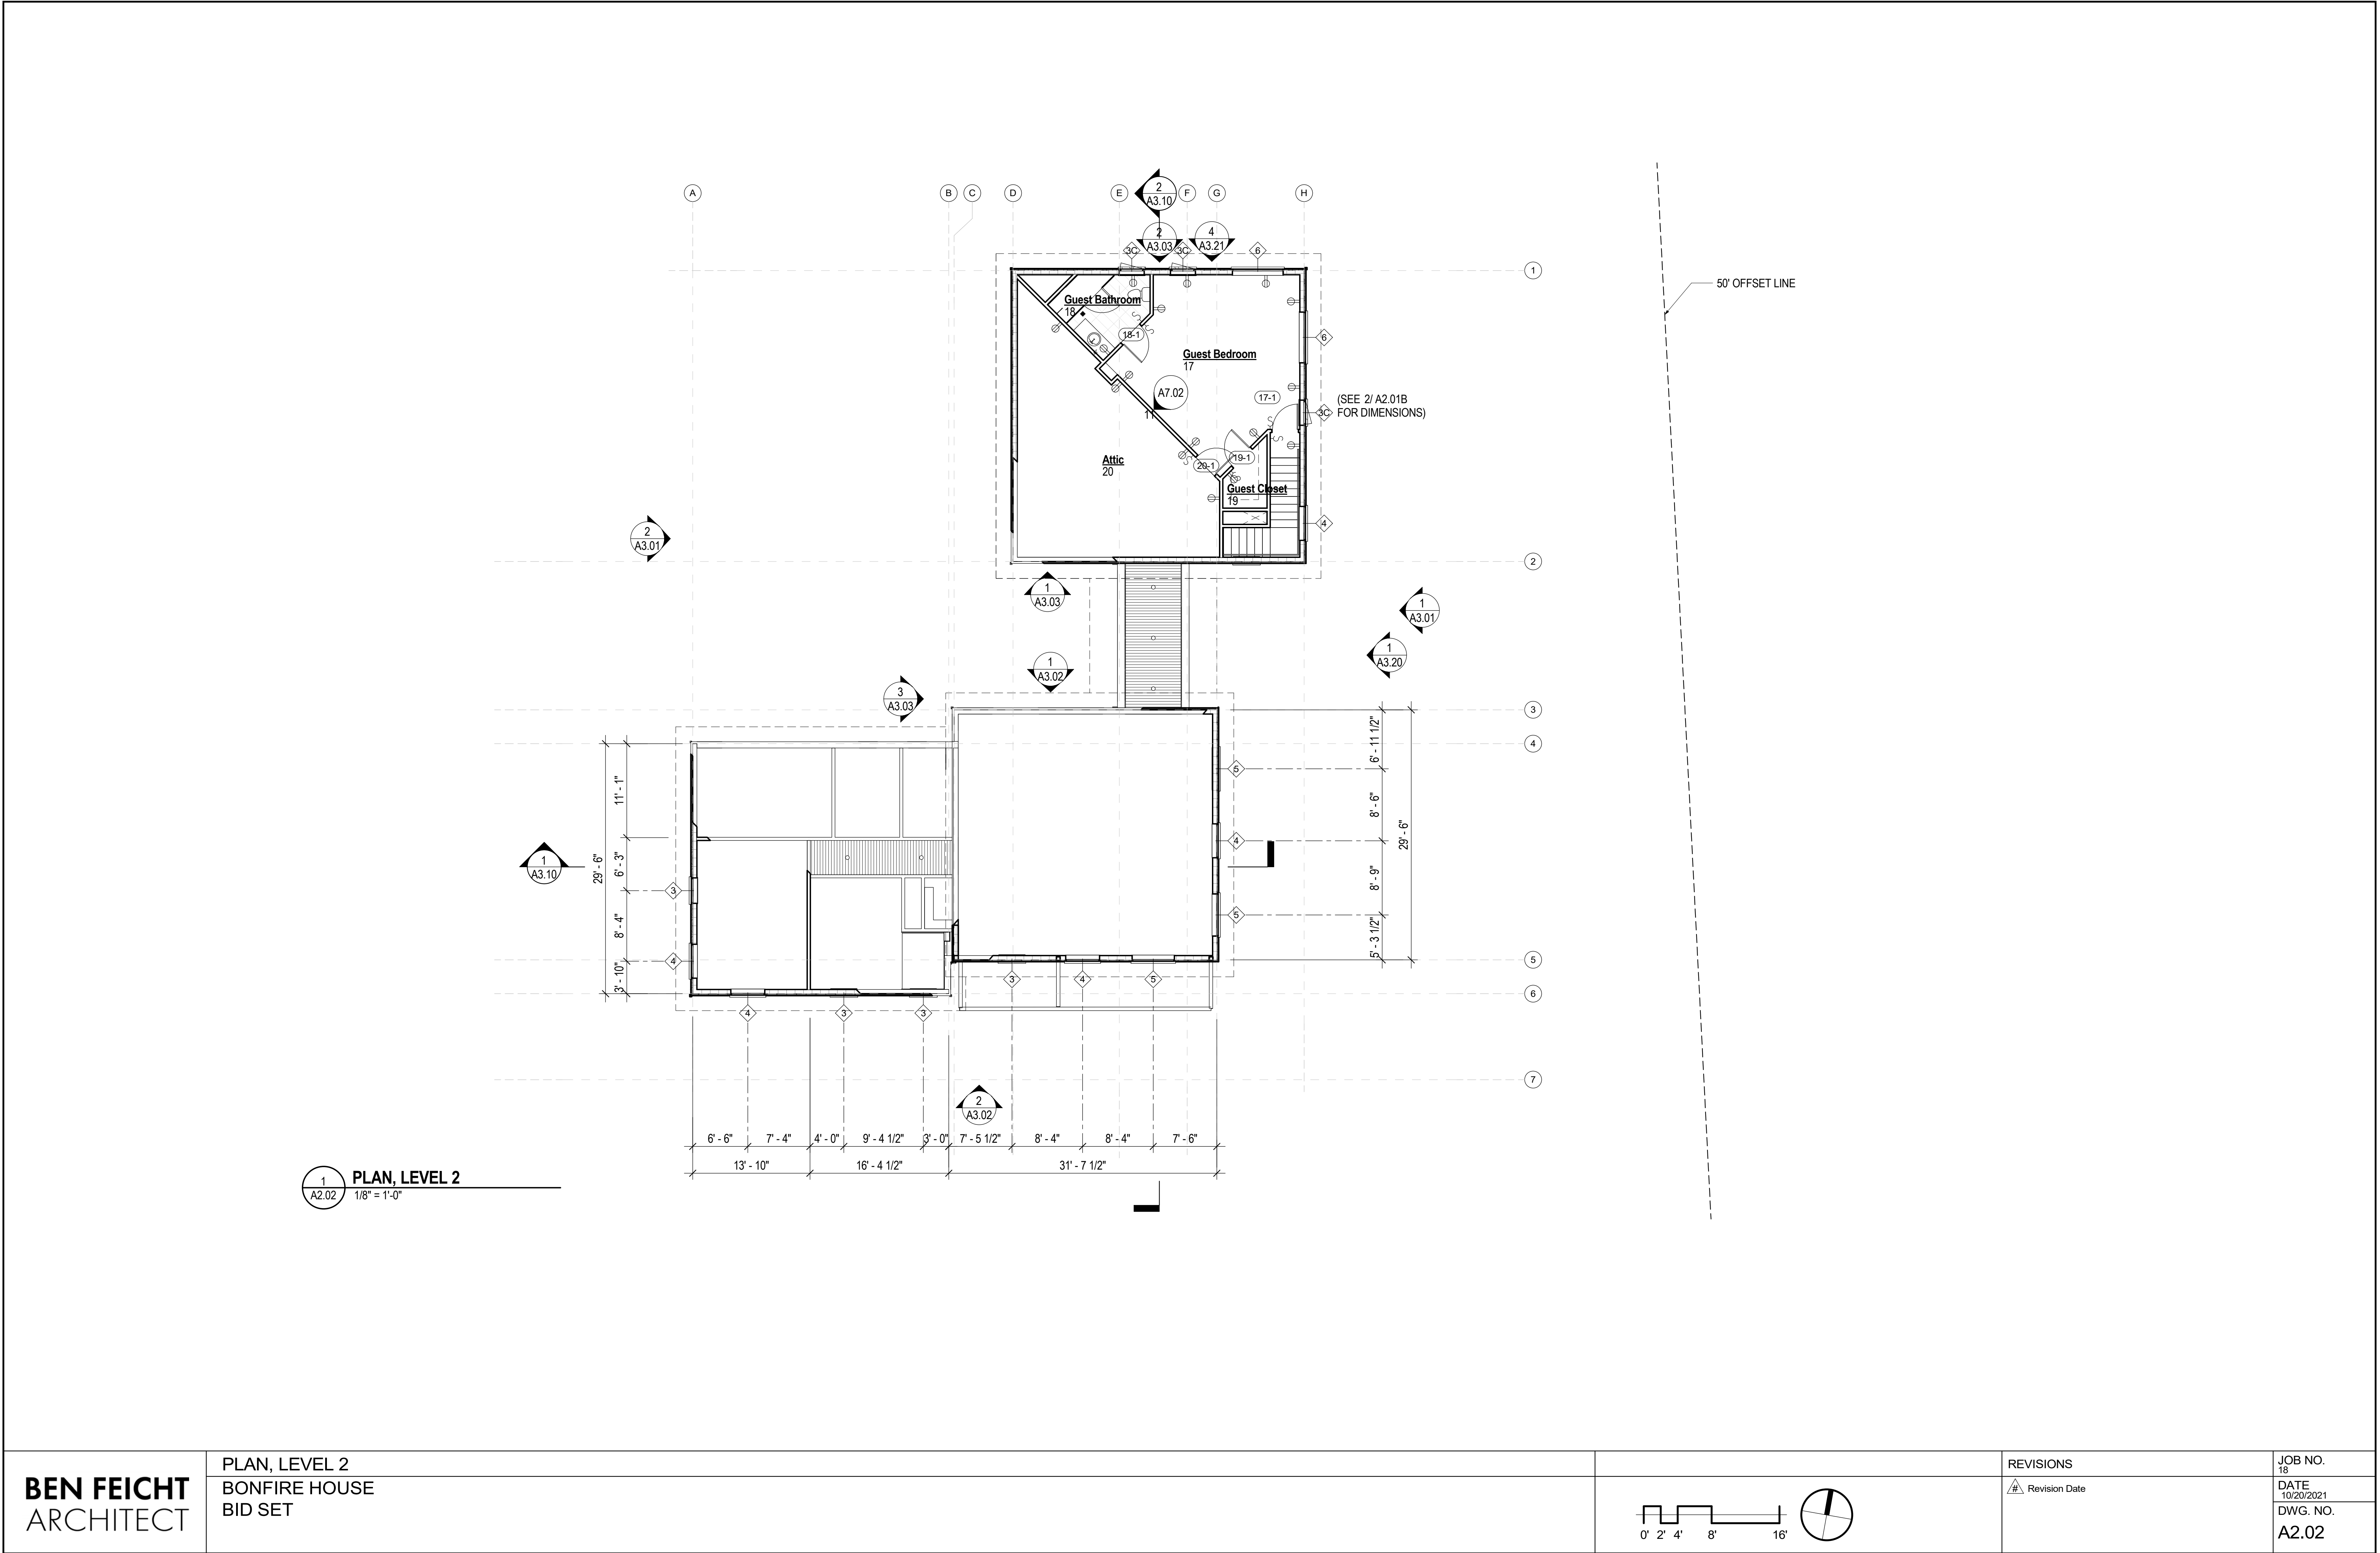

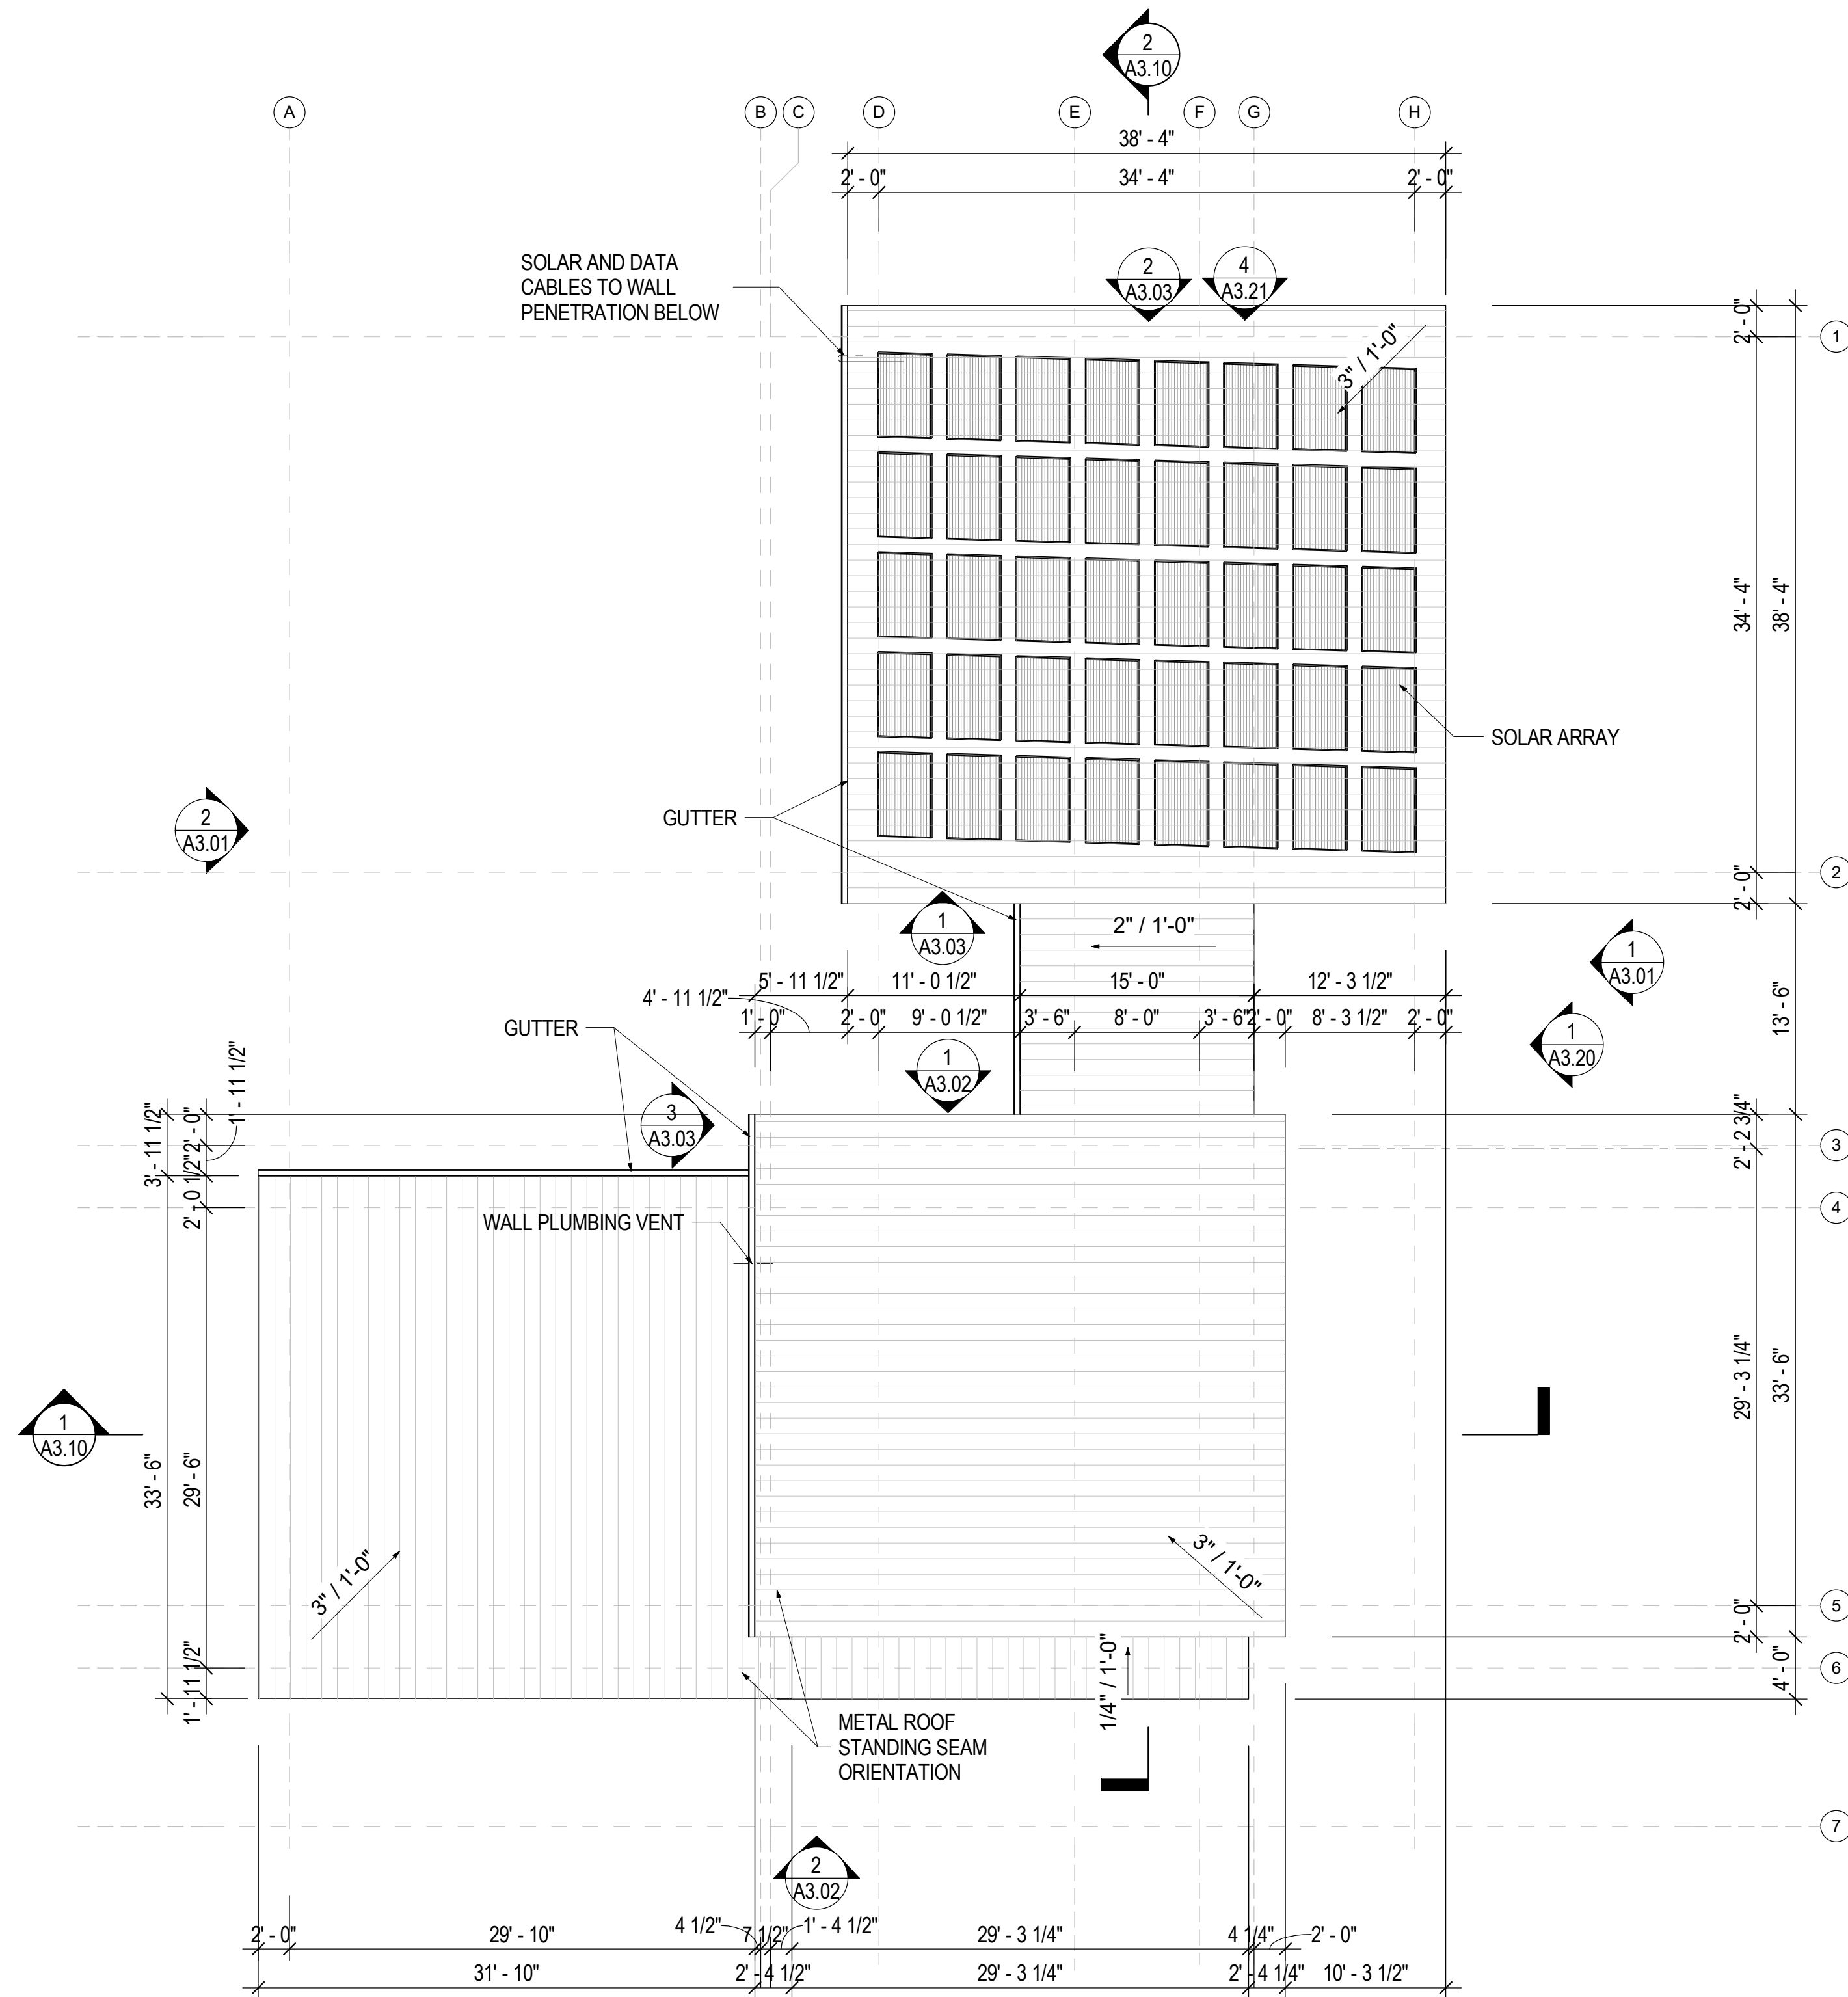


1 PLAN, ROOF
A2.03 1/8" = 1'-0"

NOTES	
1. AT WALL PLUMBING VENTS - VERIFY LOCATION W/ PLUMBER	
2. MINIMIZE ROOF PENETRATIONS, CONSOLIDATE AND COORDINATE W/ ARCHITECT PRIOR TO CONSTRUCTION.	

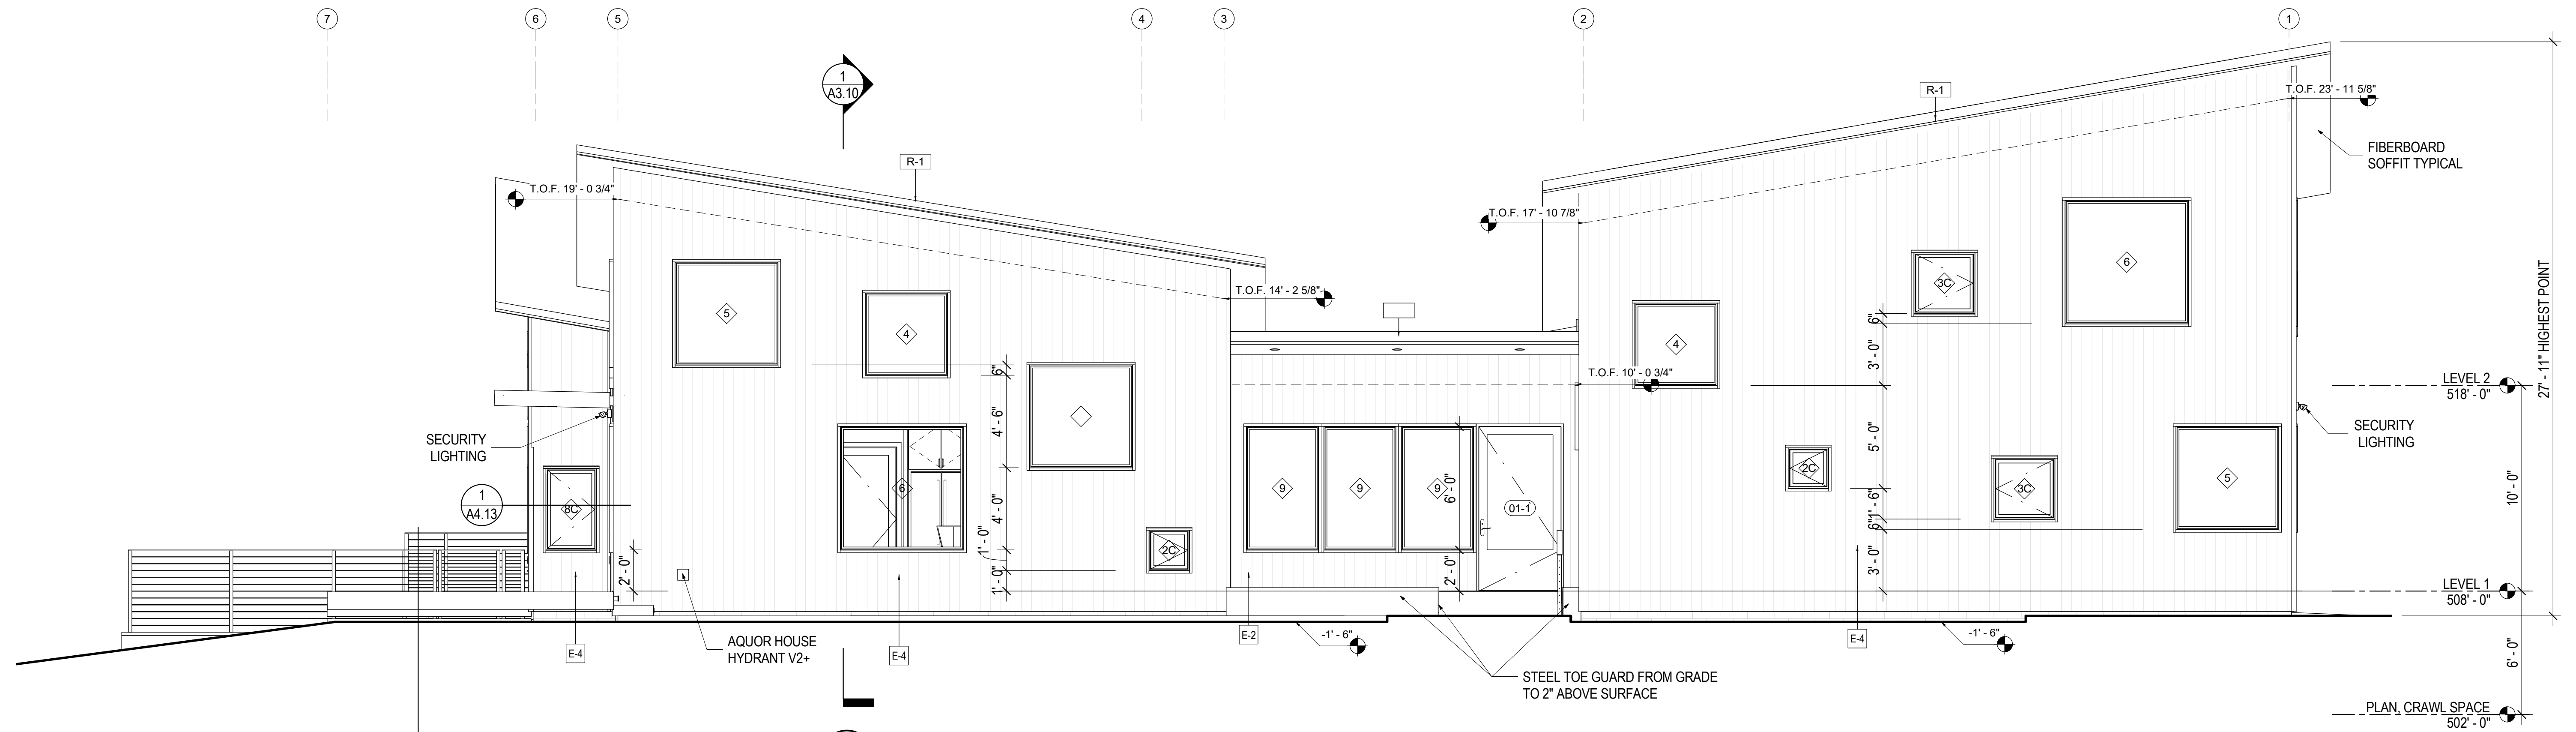


EAST ELEVATION
1
A3.10
1/4" = 1'-0"

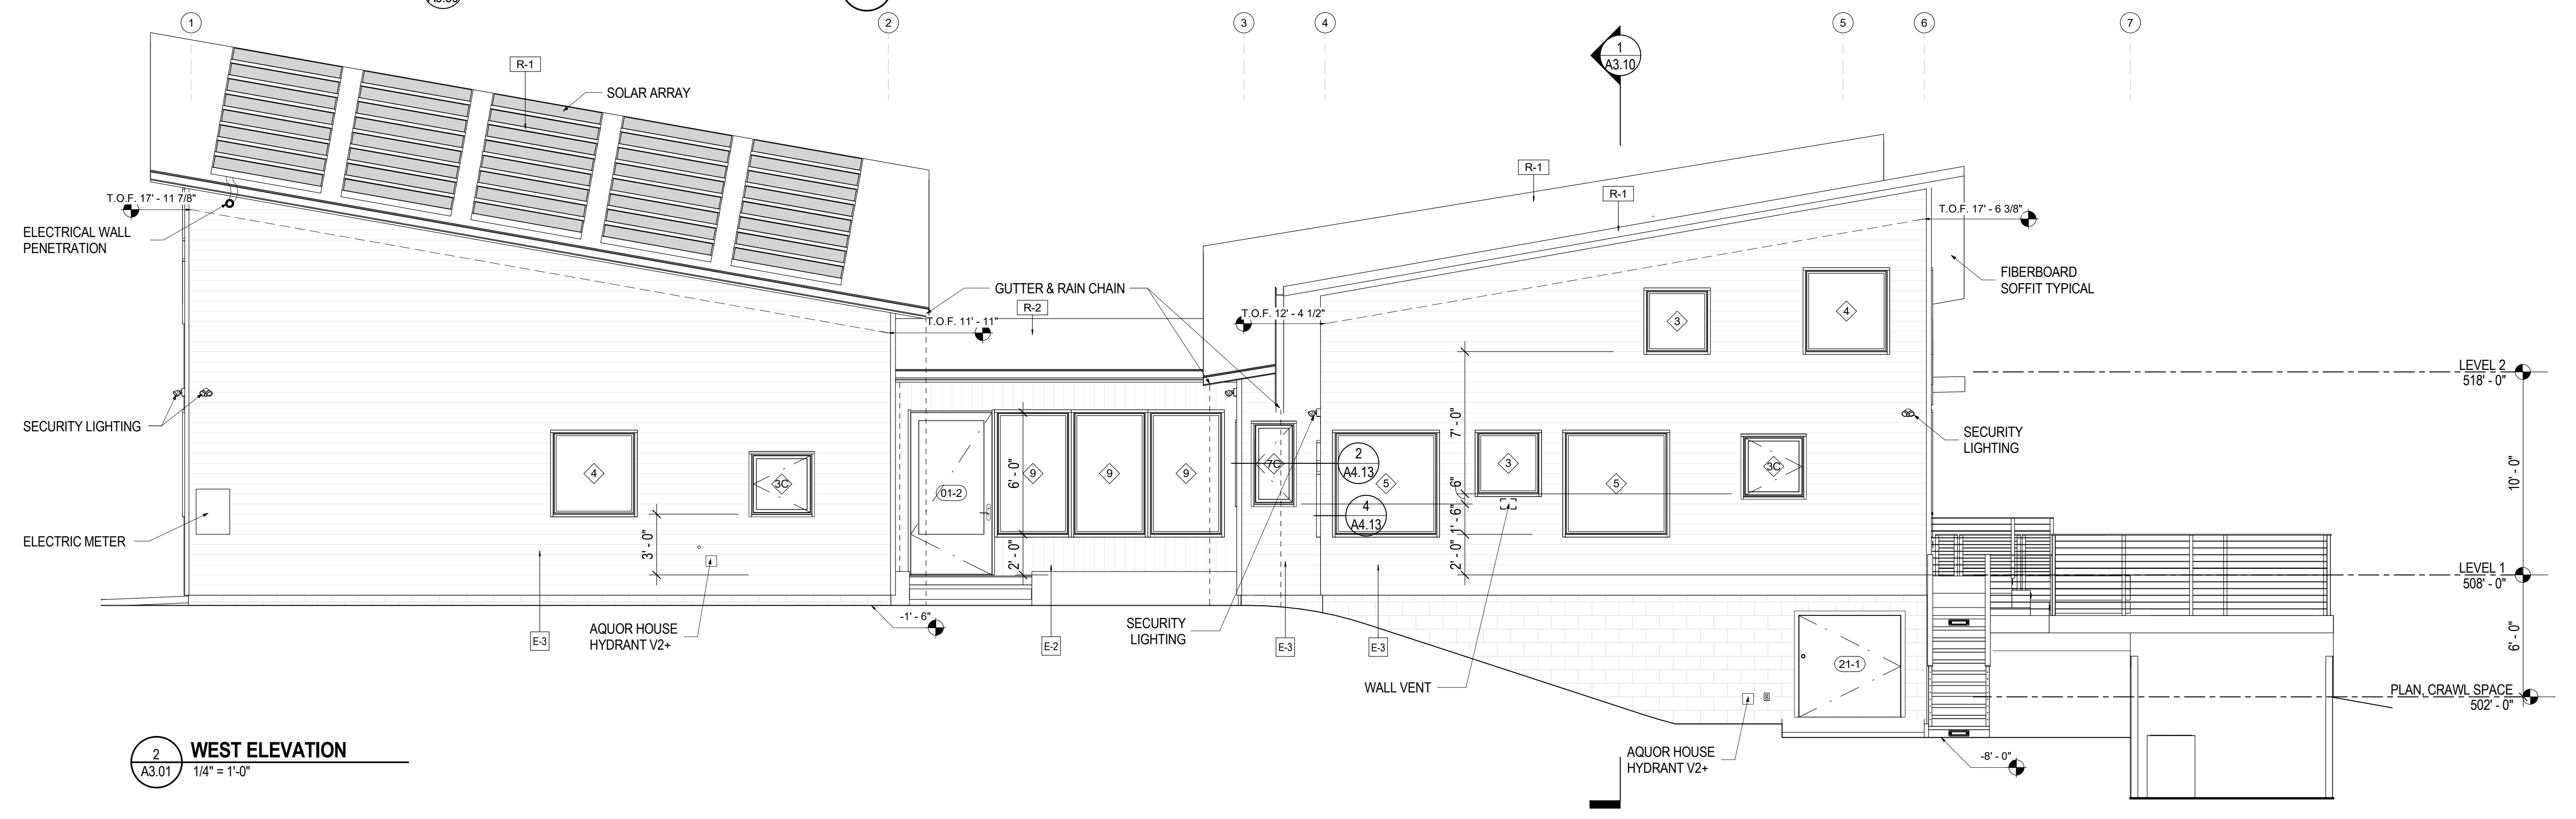

WEST ELEVATION
2
A3.01
1/4" = 1'-0"


BEN FEICHT
ARCHITECT

ELEVATIONS, EXTERIOR, EAST & WEST
BONFIRE HOUSE
BID SET

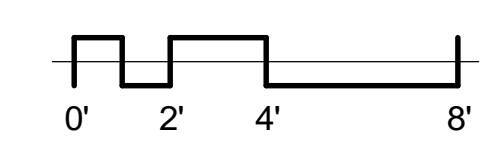


REVISIONS
Revision Date


JOB NO.
18
DATE
10/20/2021
DWG. NO.
A3.01

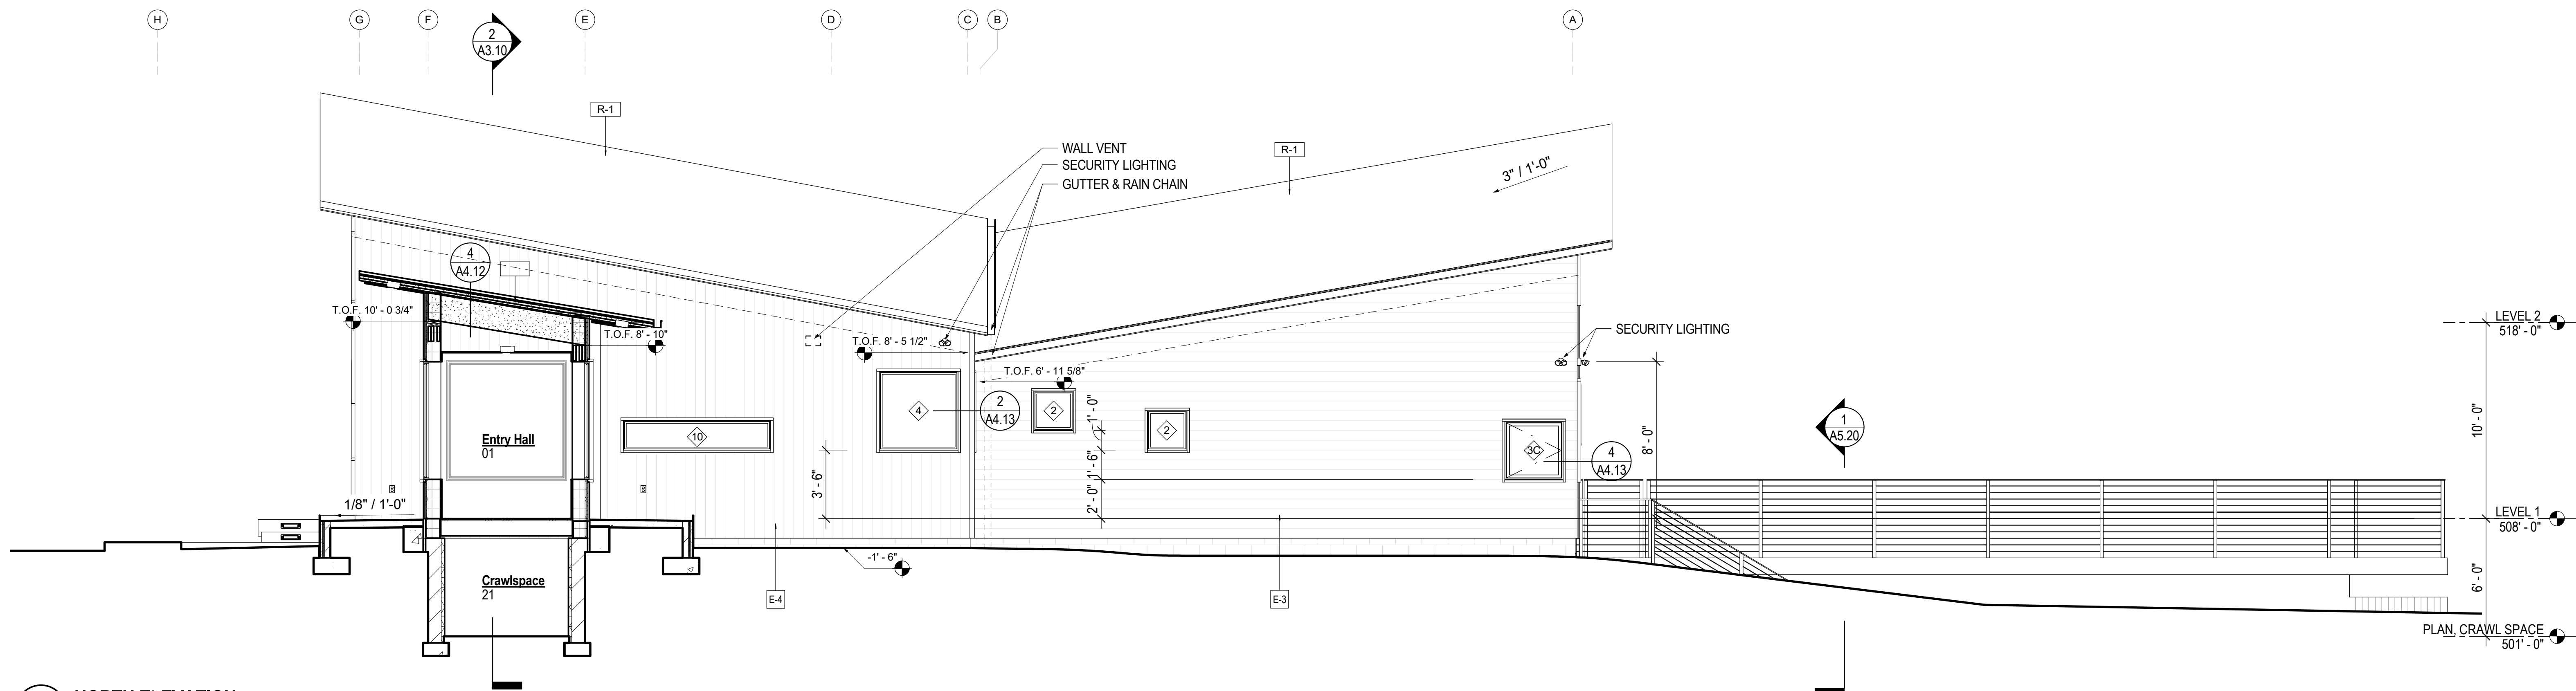


1 NORTH ELEVATION
A3.02
1/4" = 1'-0"

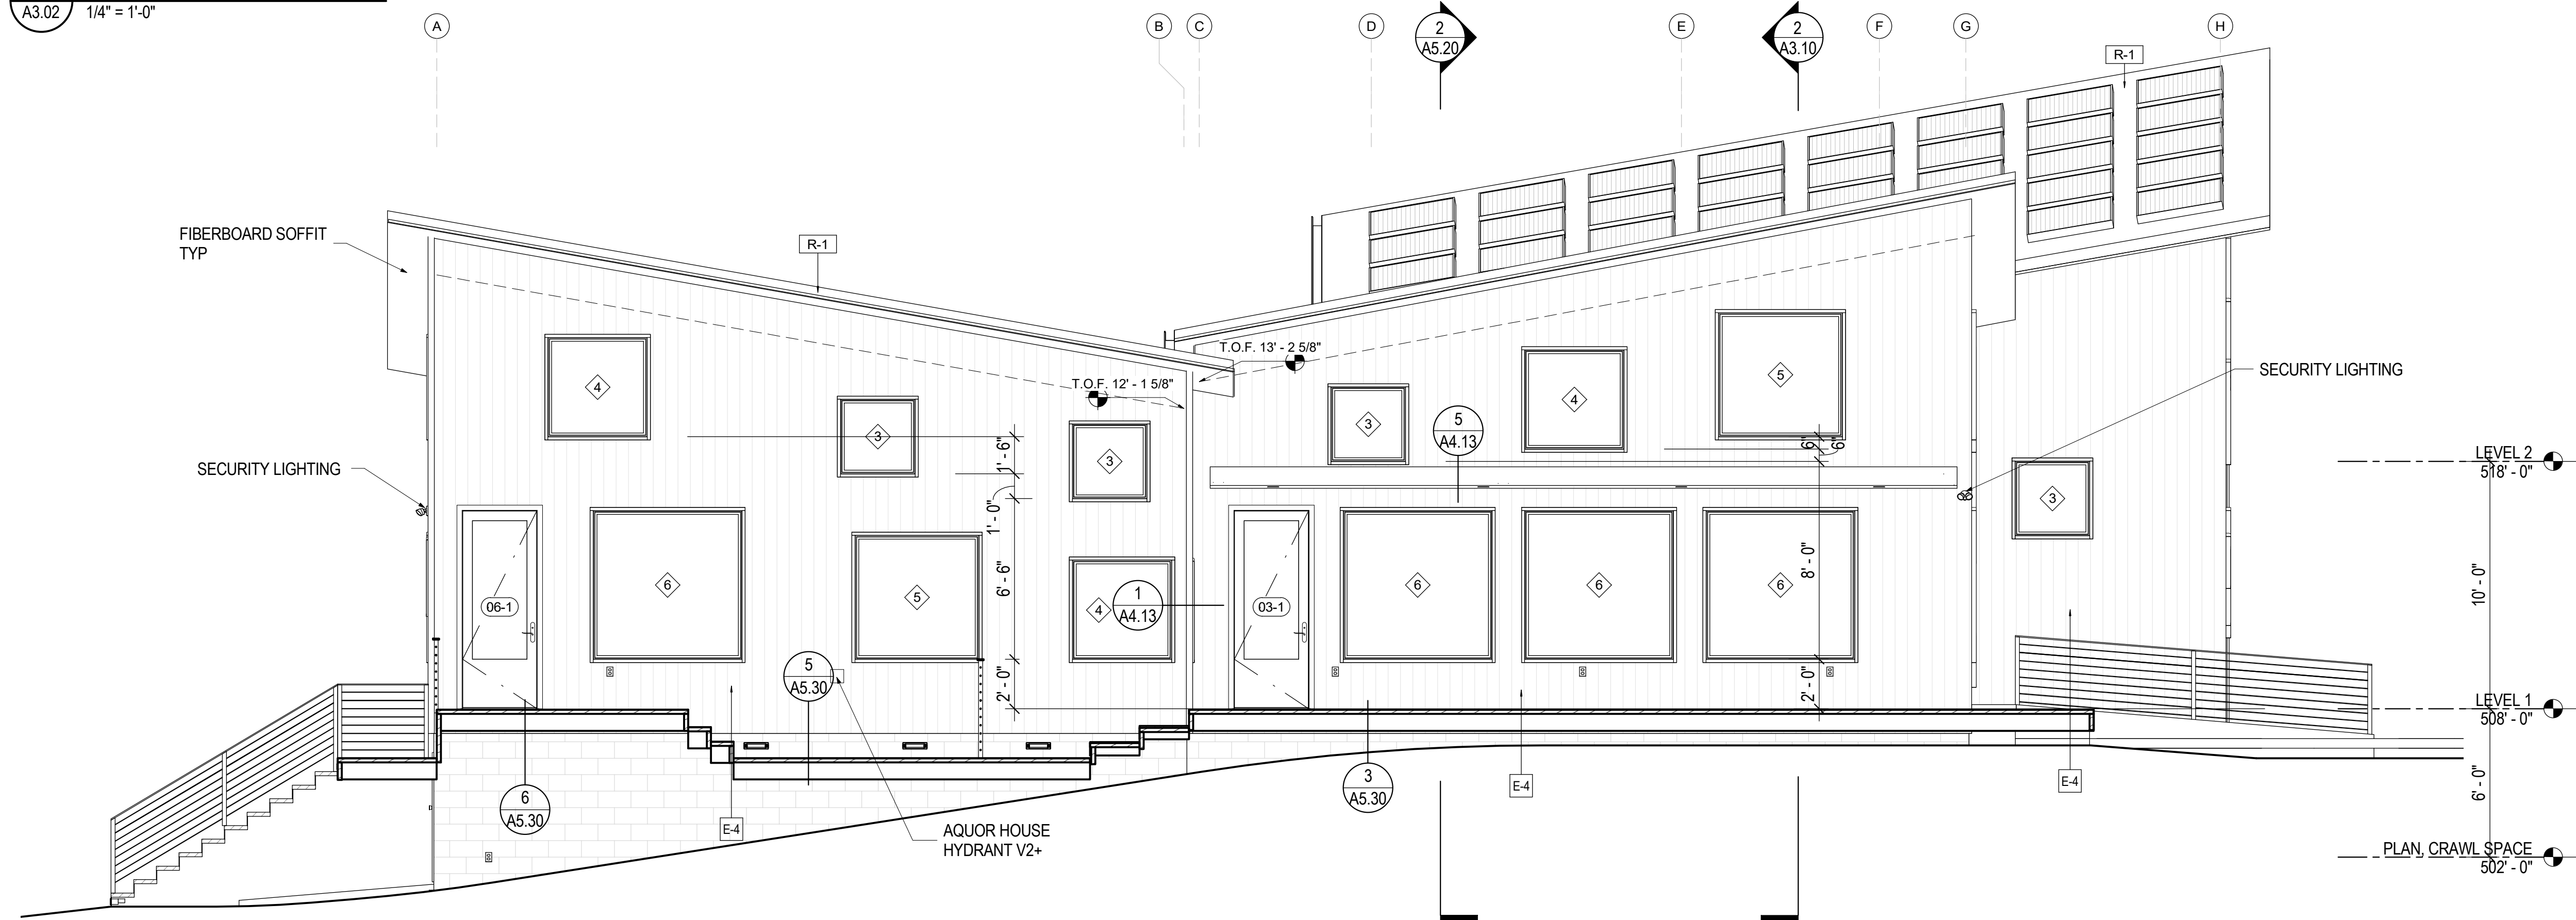


2 SOUTH ELEVATION
A3.02
1/4" = 1'-0"

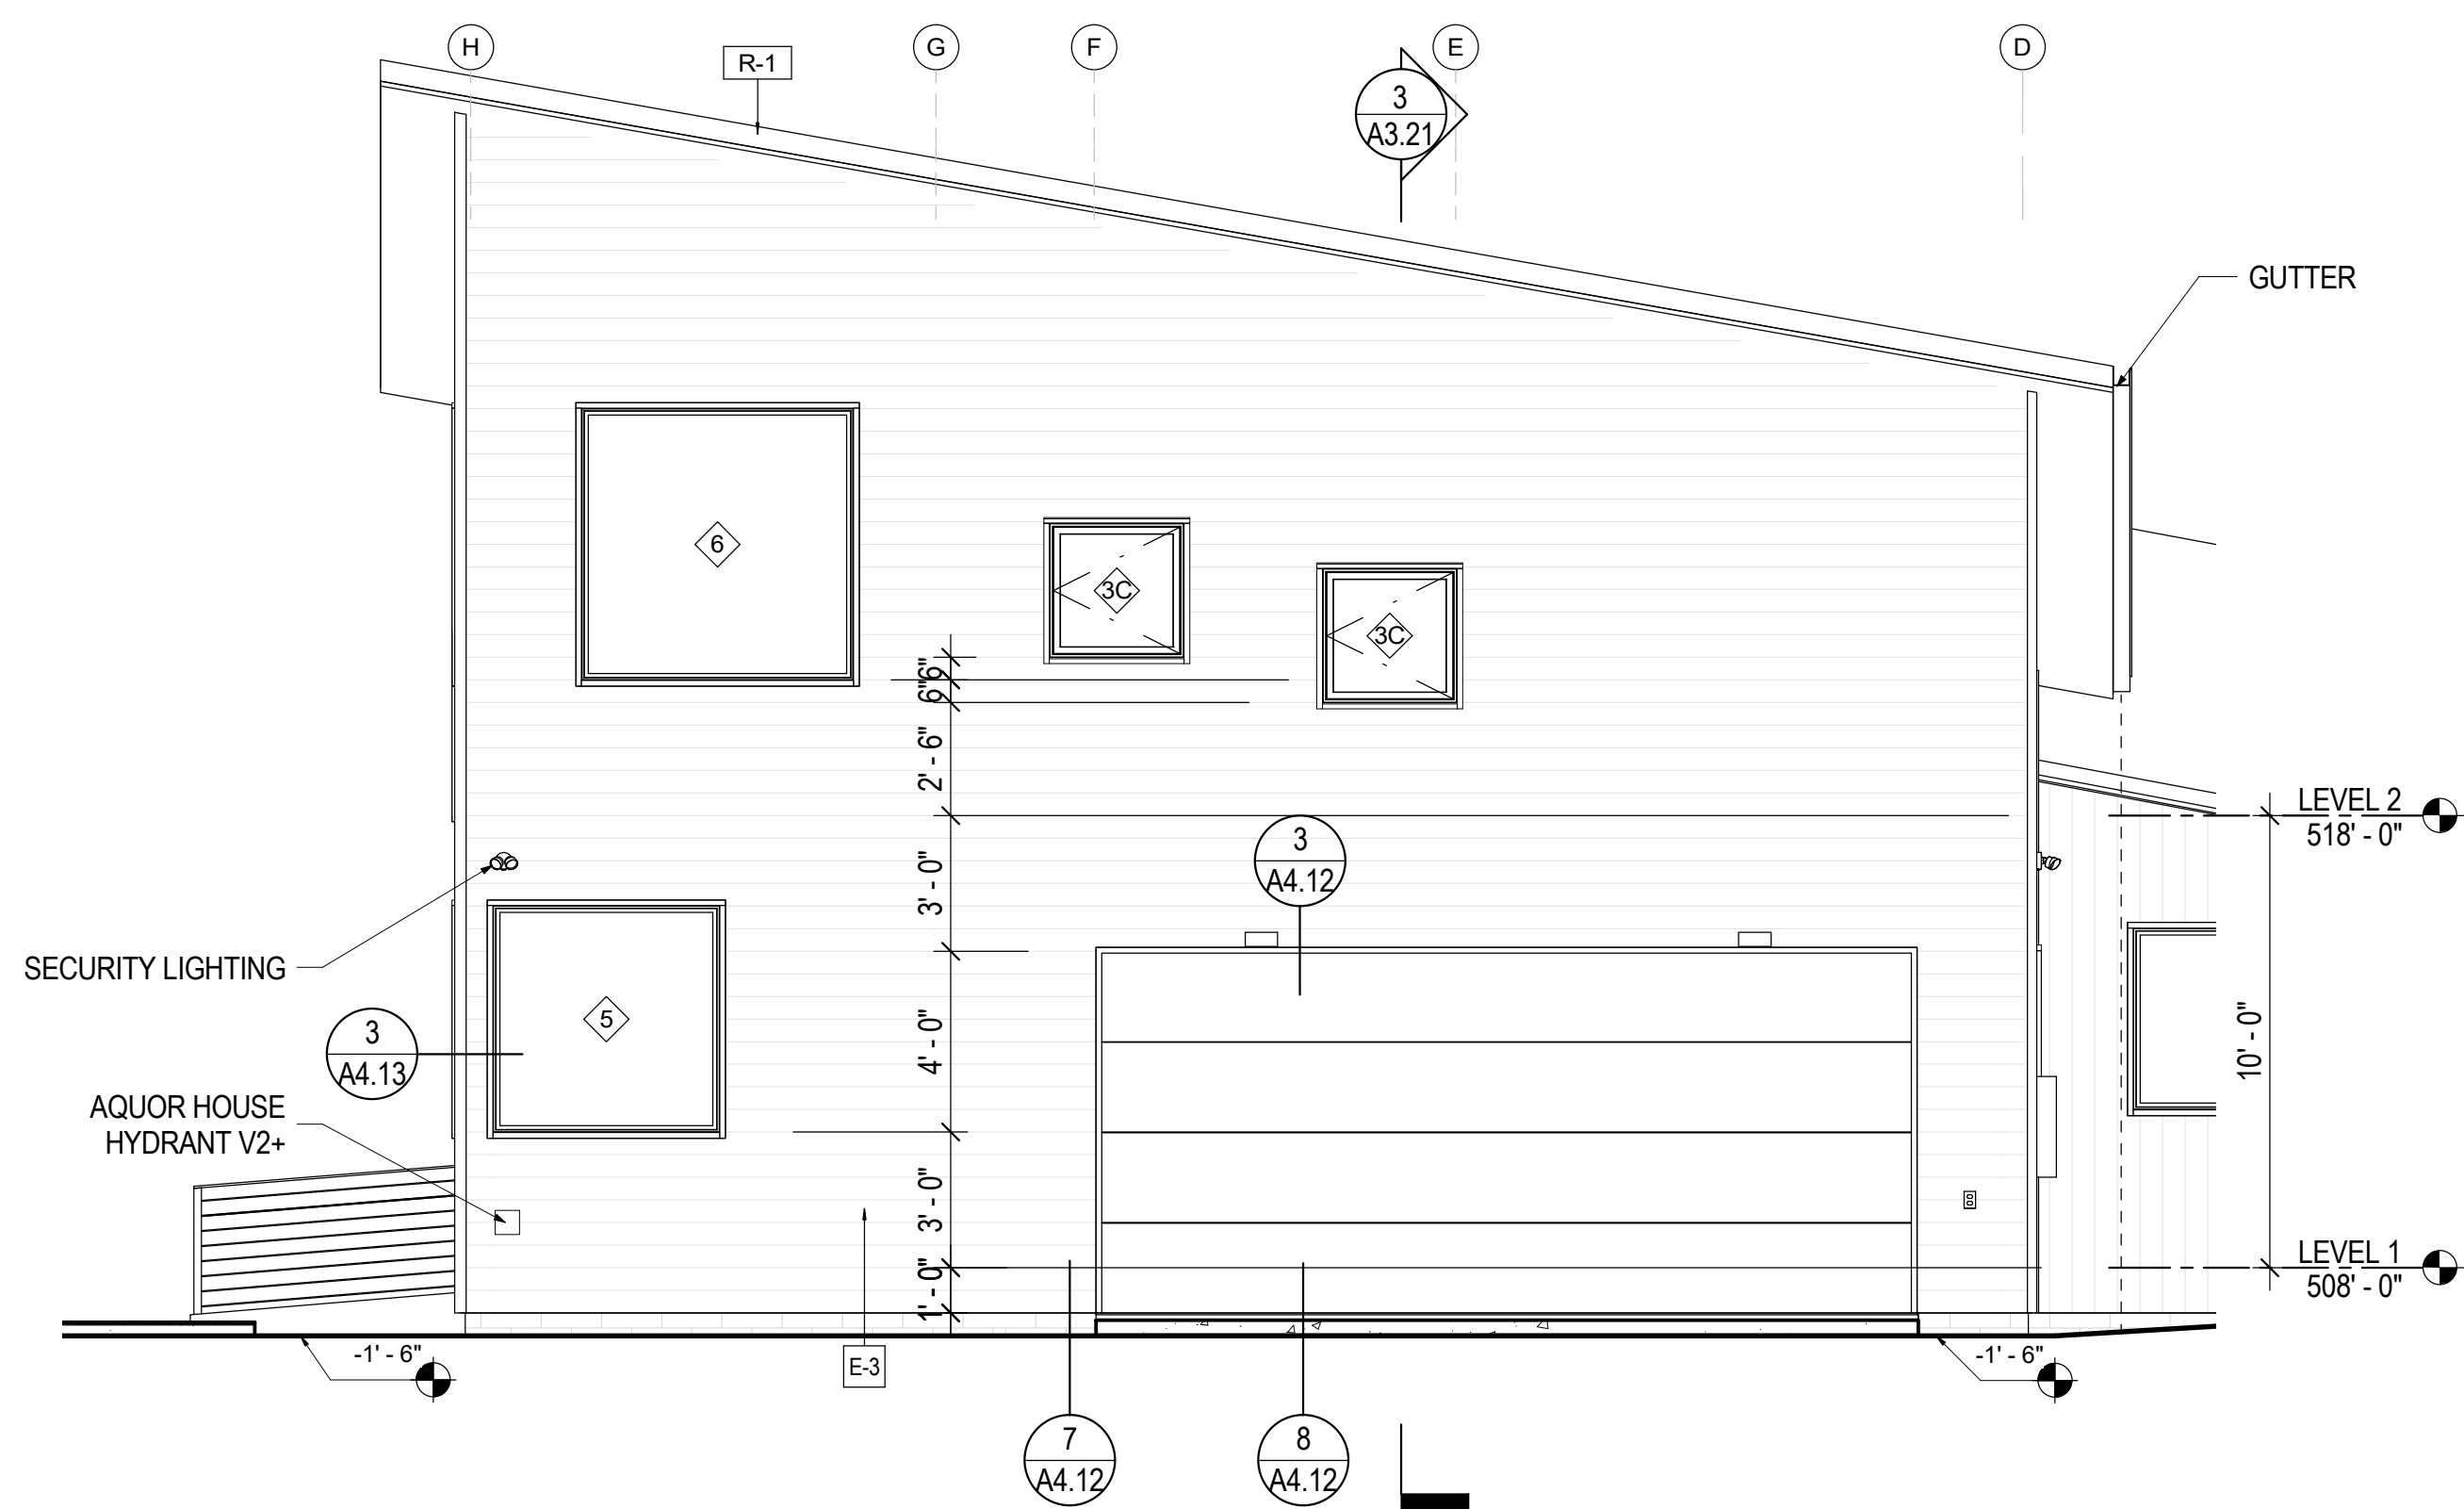


2 NORTH ELEVATION, GARAGE FACADE
A3.03 1/4" = 1'-0"

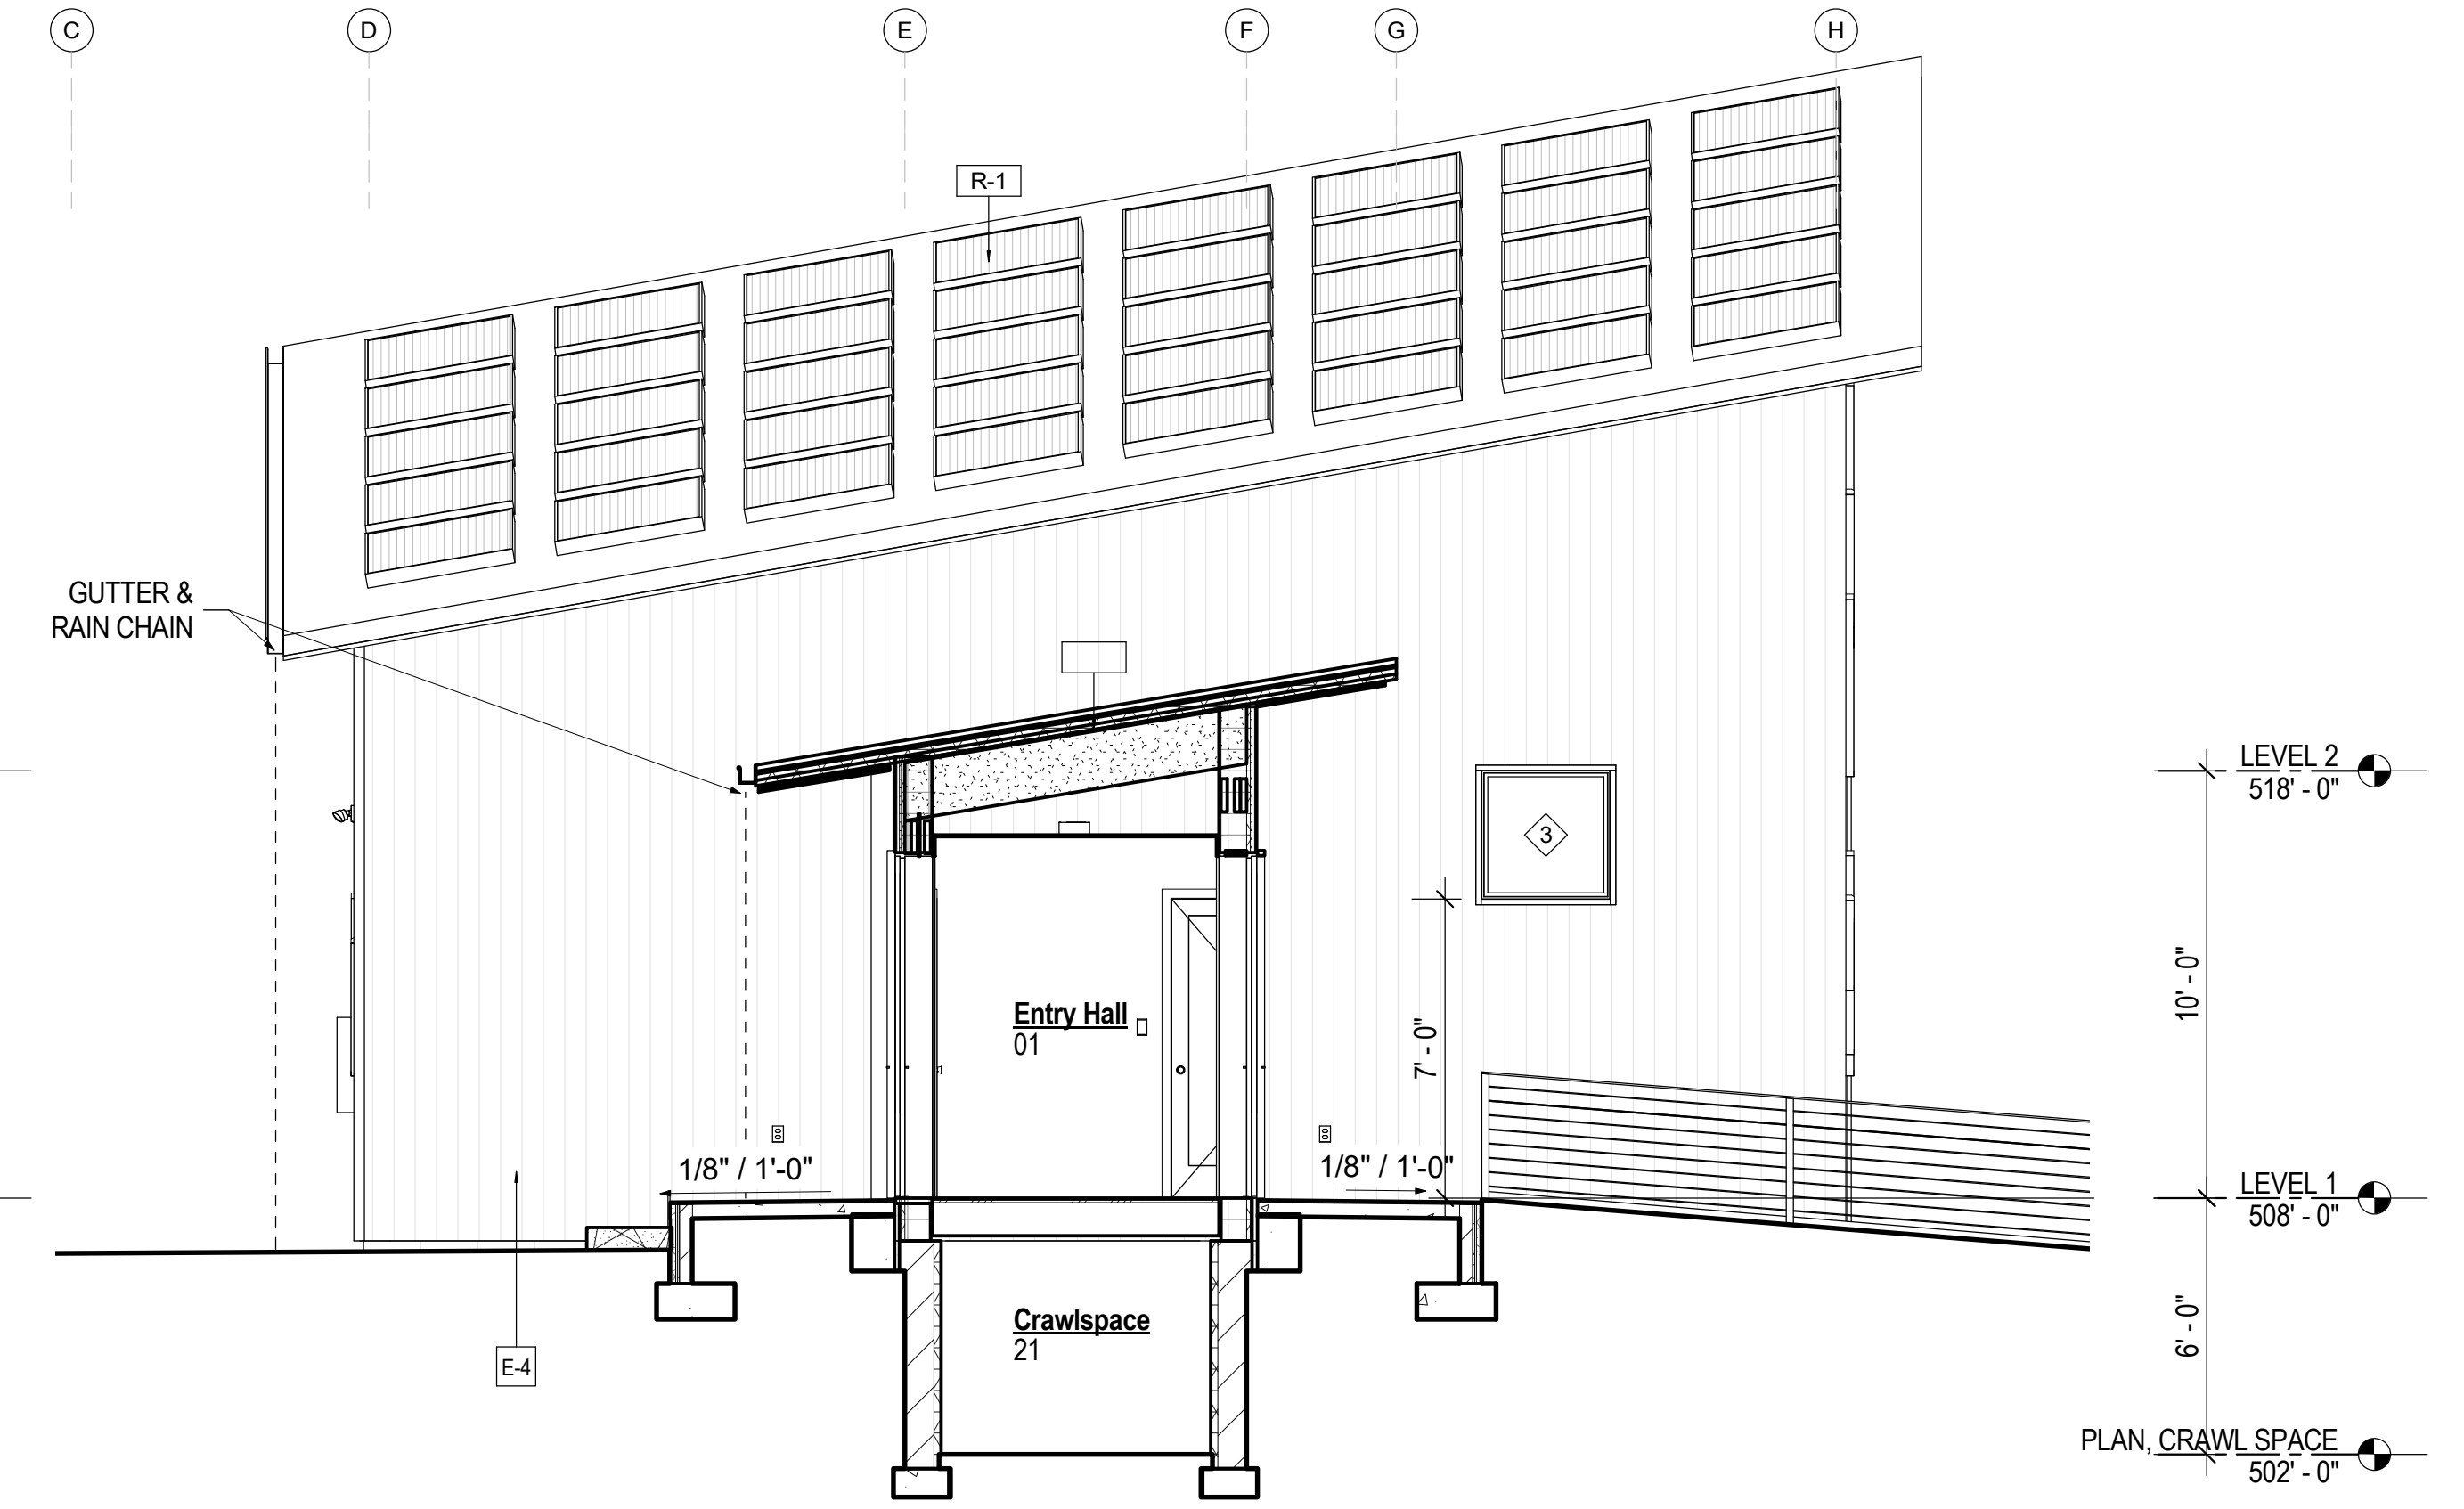


1 SOUTH ELEVATION, LAUNDRY / GUEST BED FACADE
A3.03 1/4" = 1'-0"

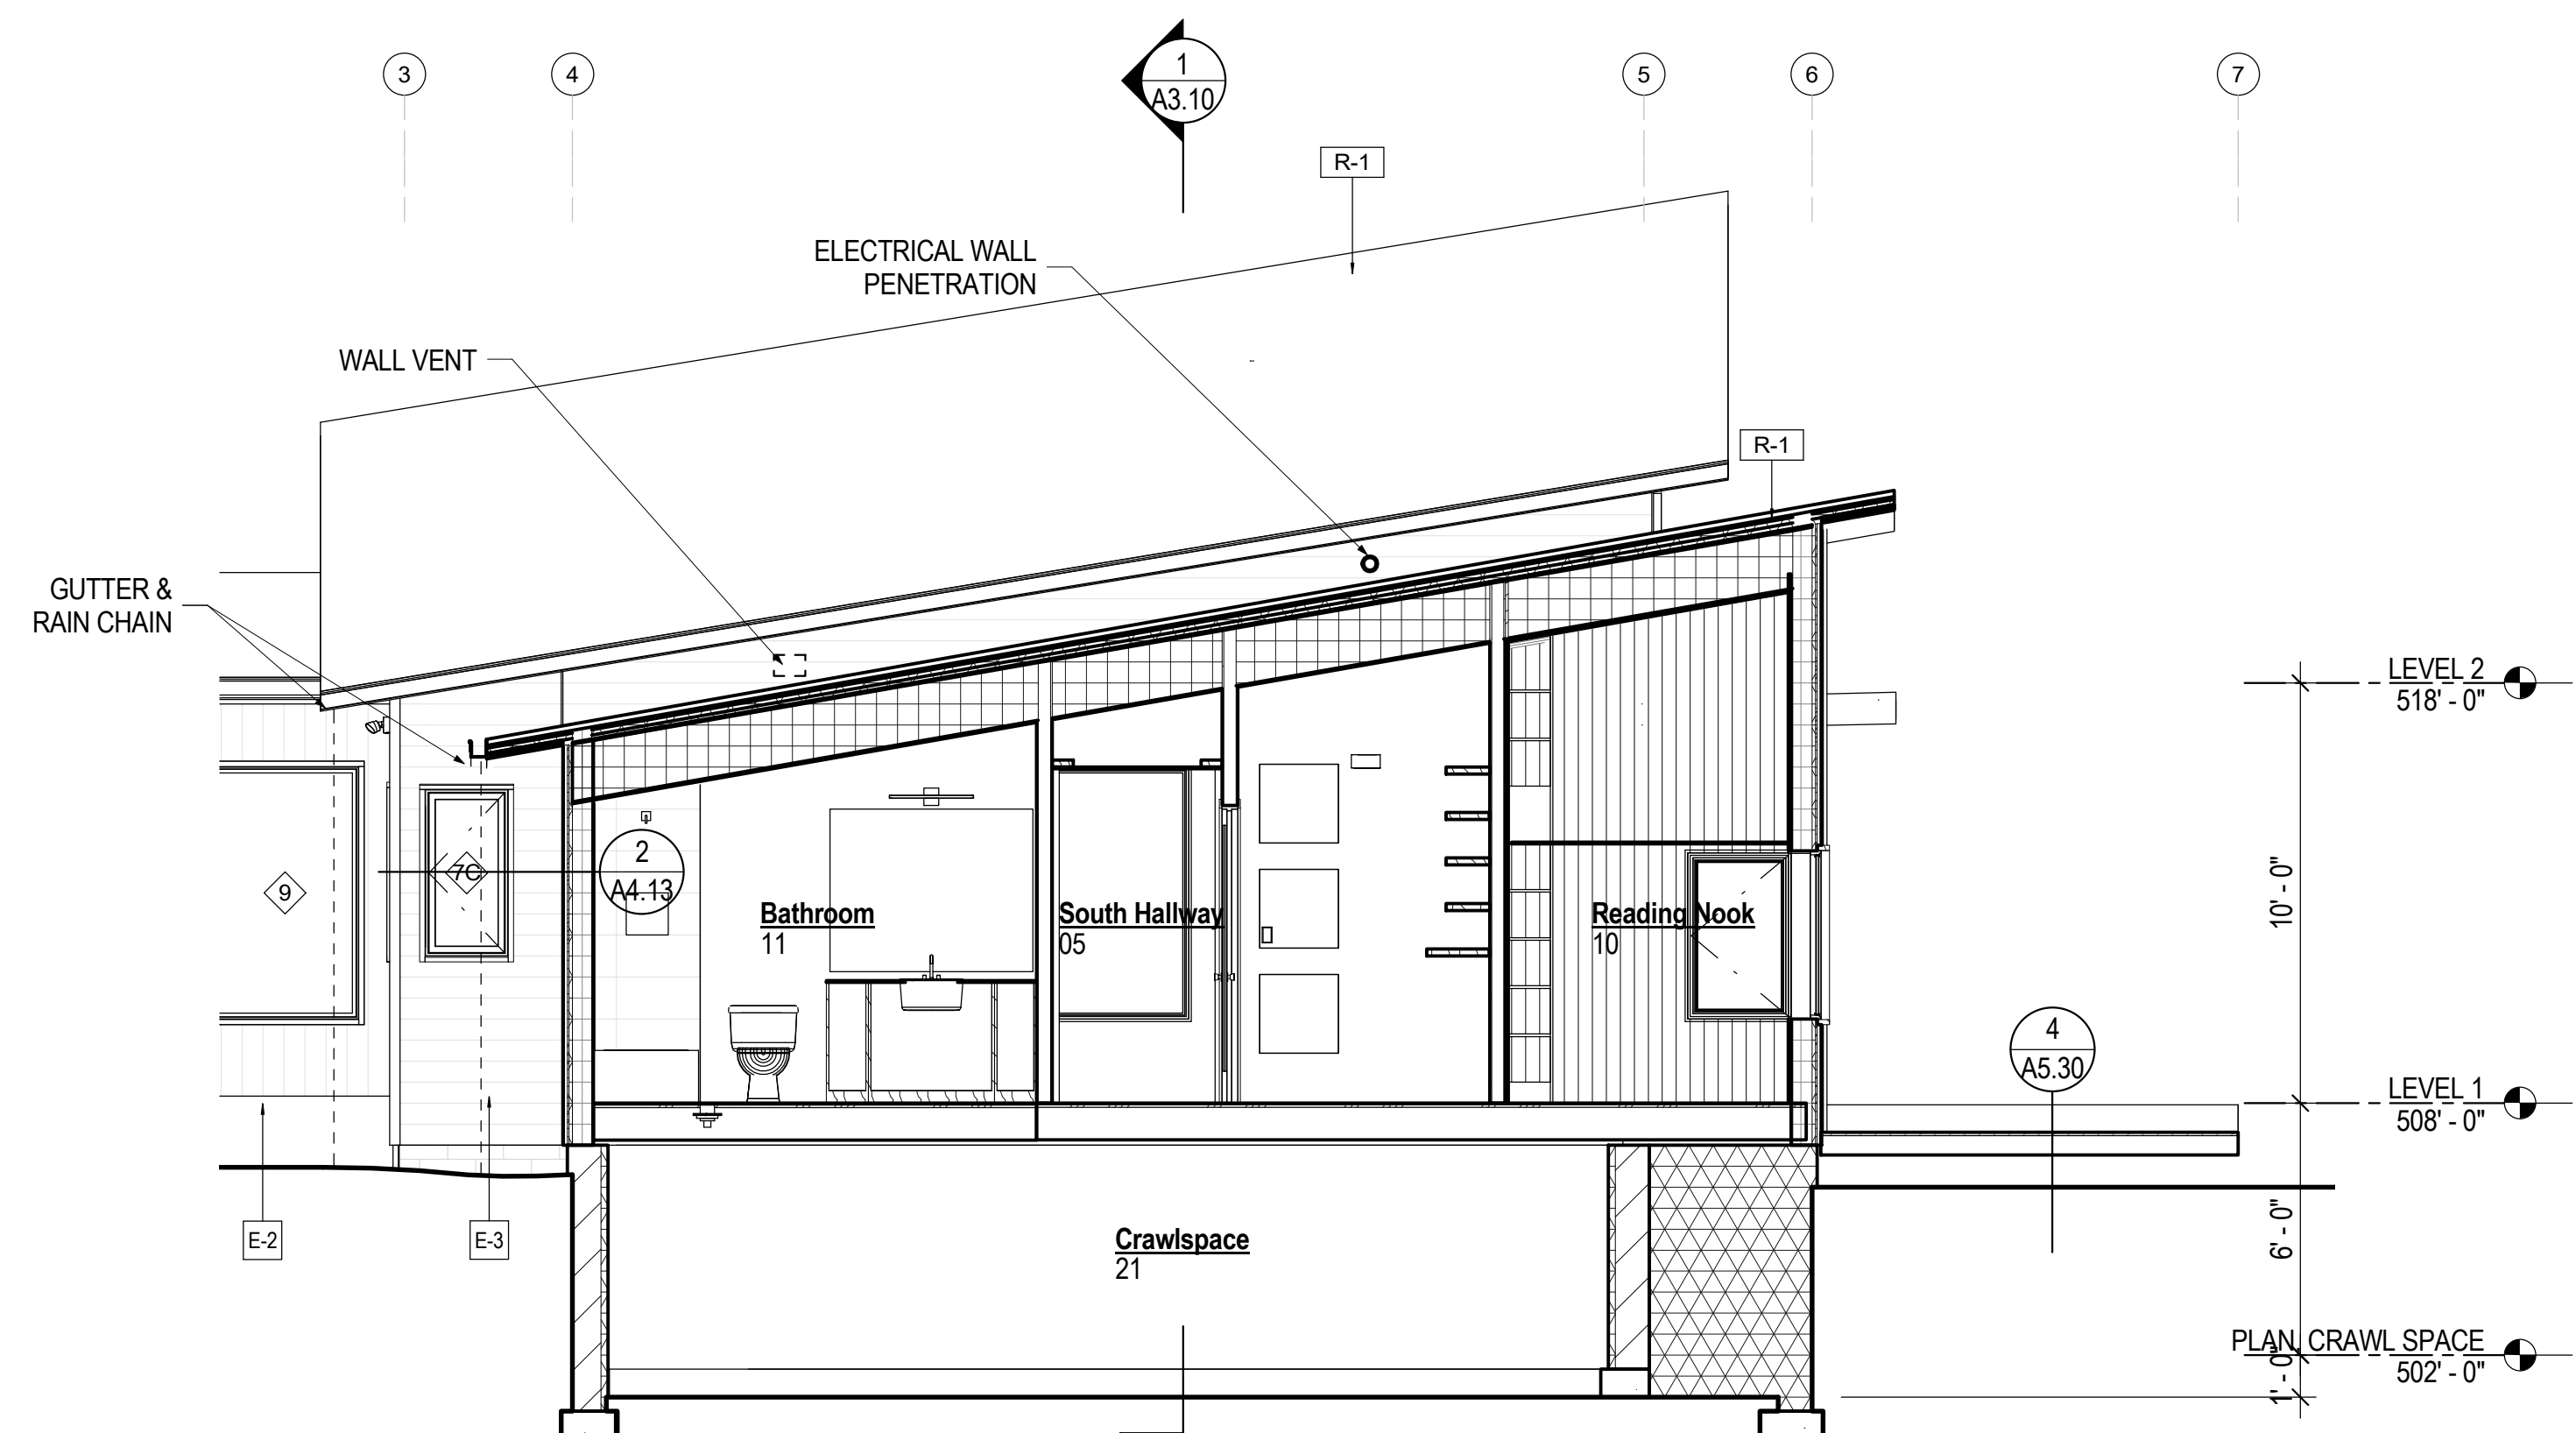


3 WEST ELEVATION, PARTIAL, LIVING ROOM
A3.03 1/4" = 1'-0"

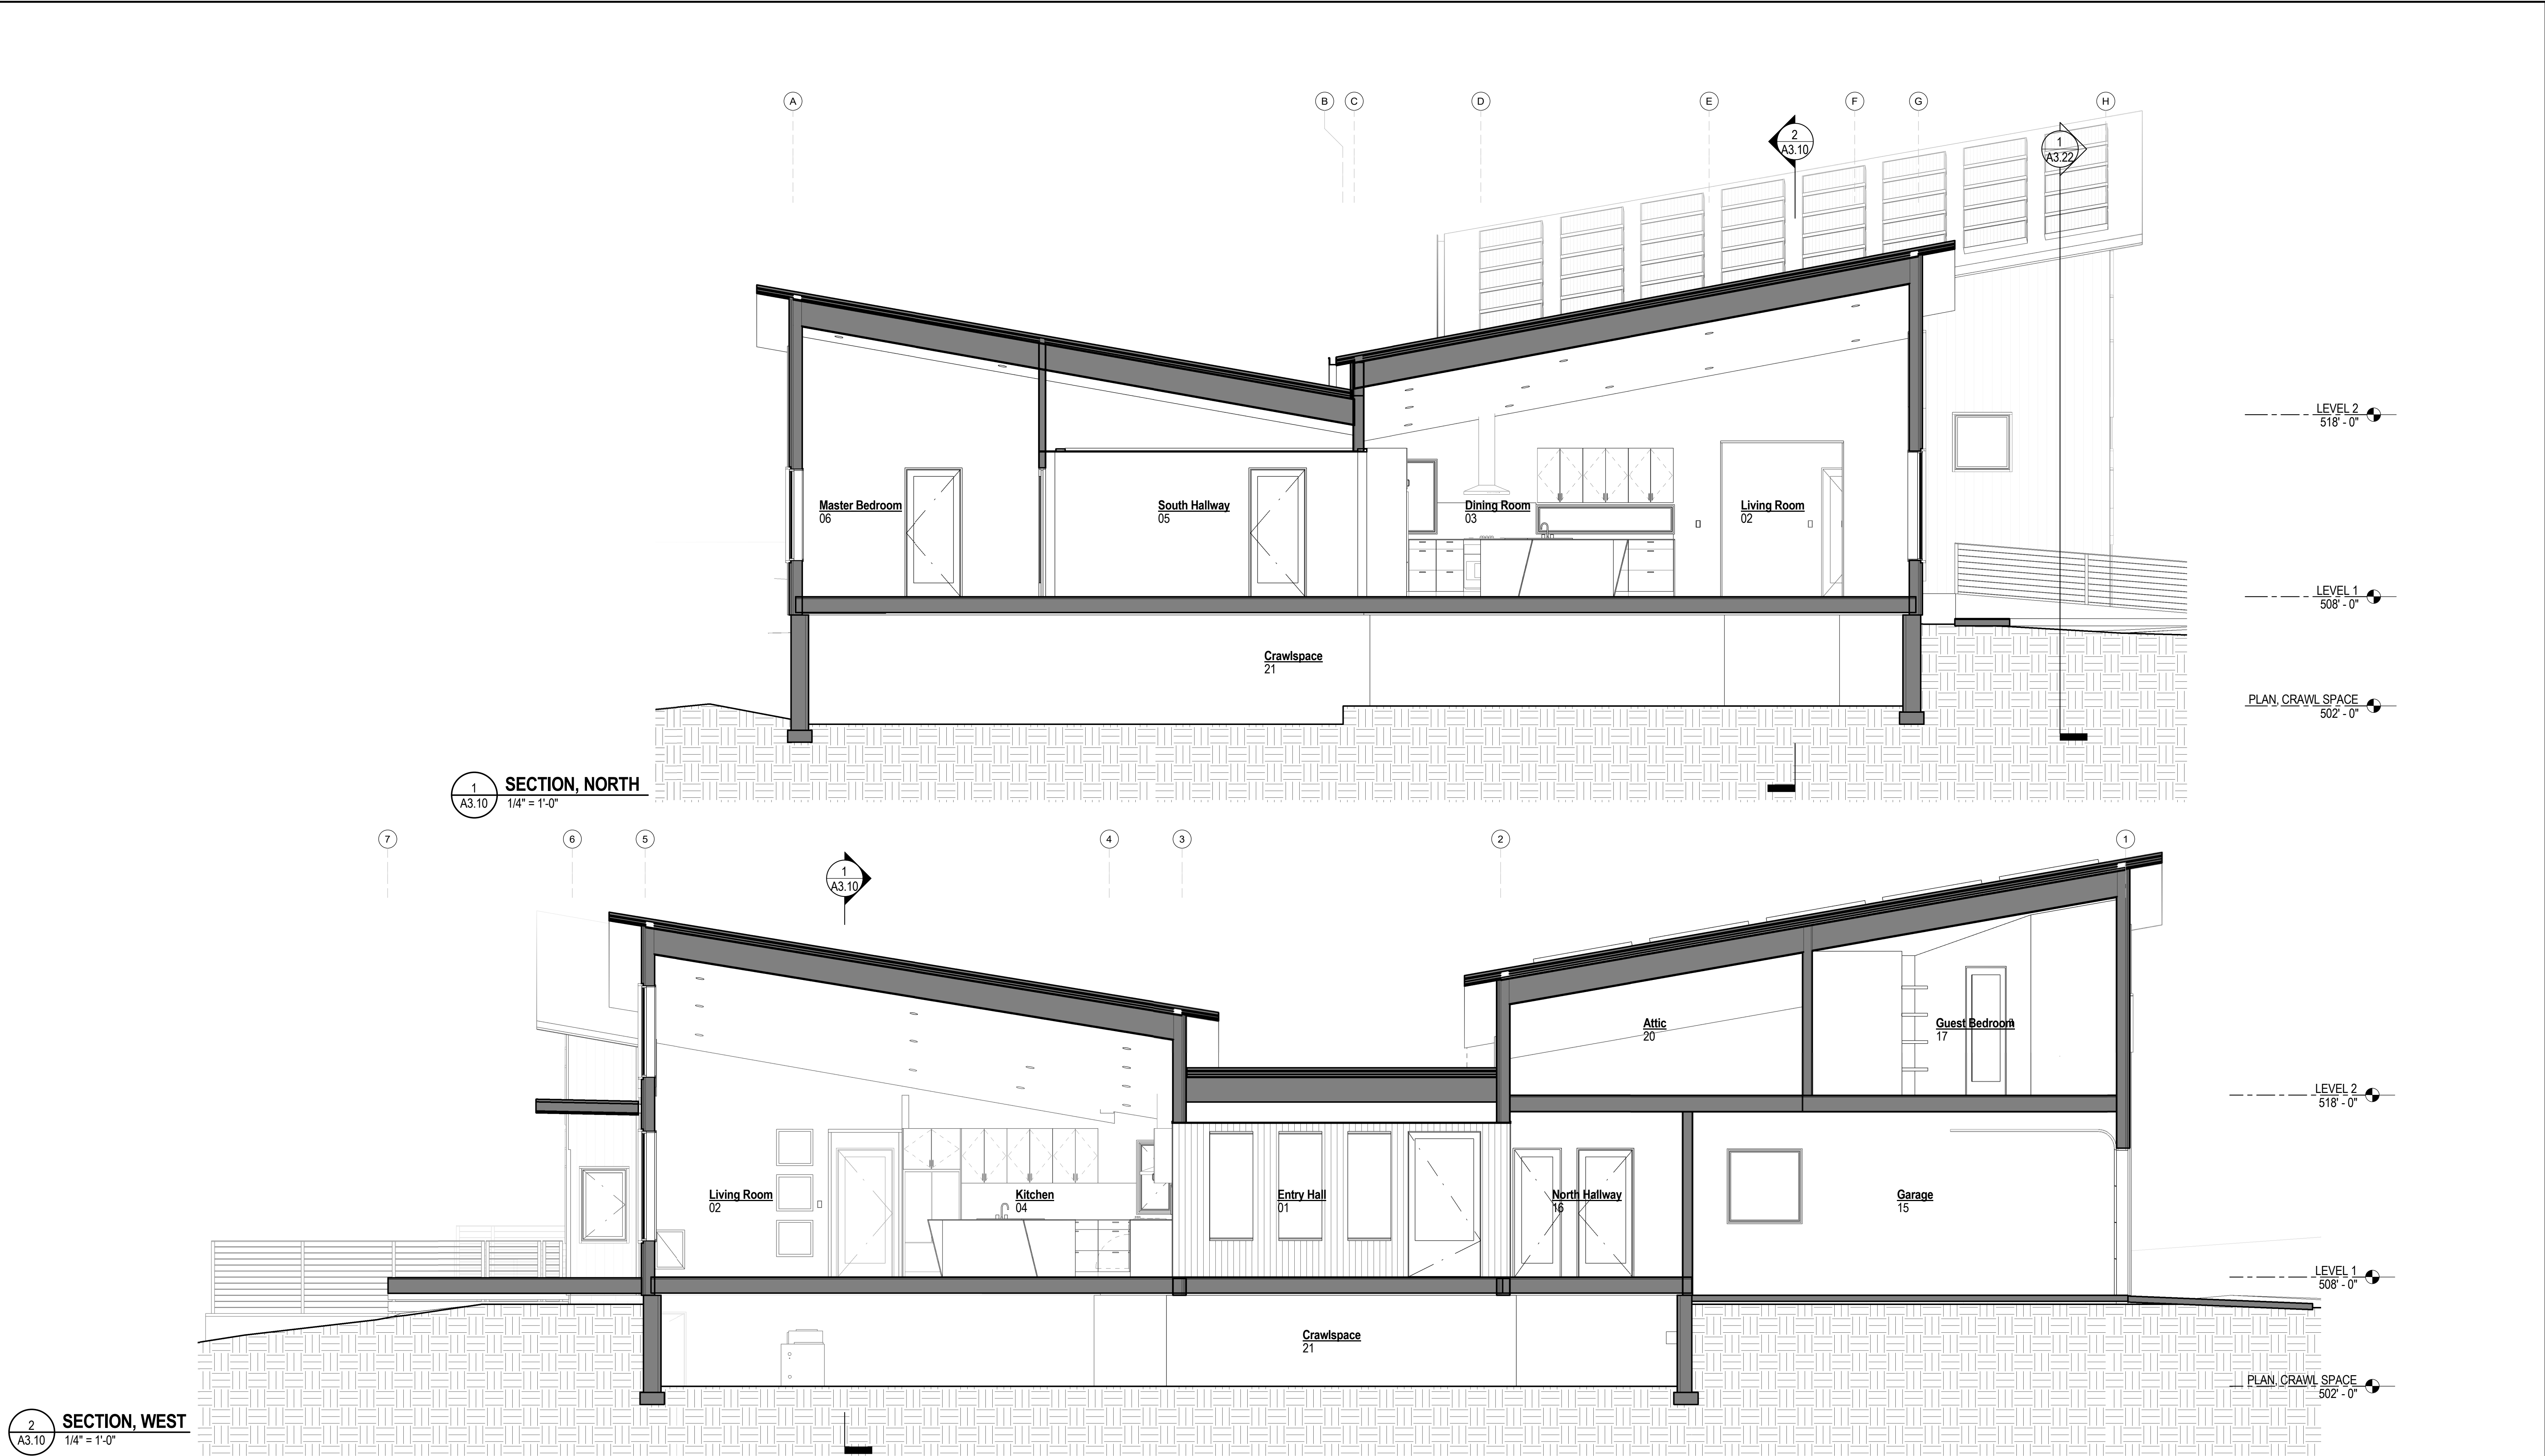


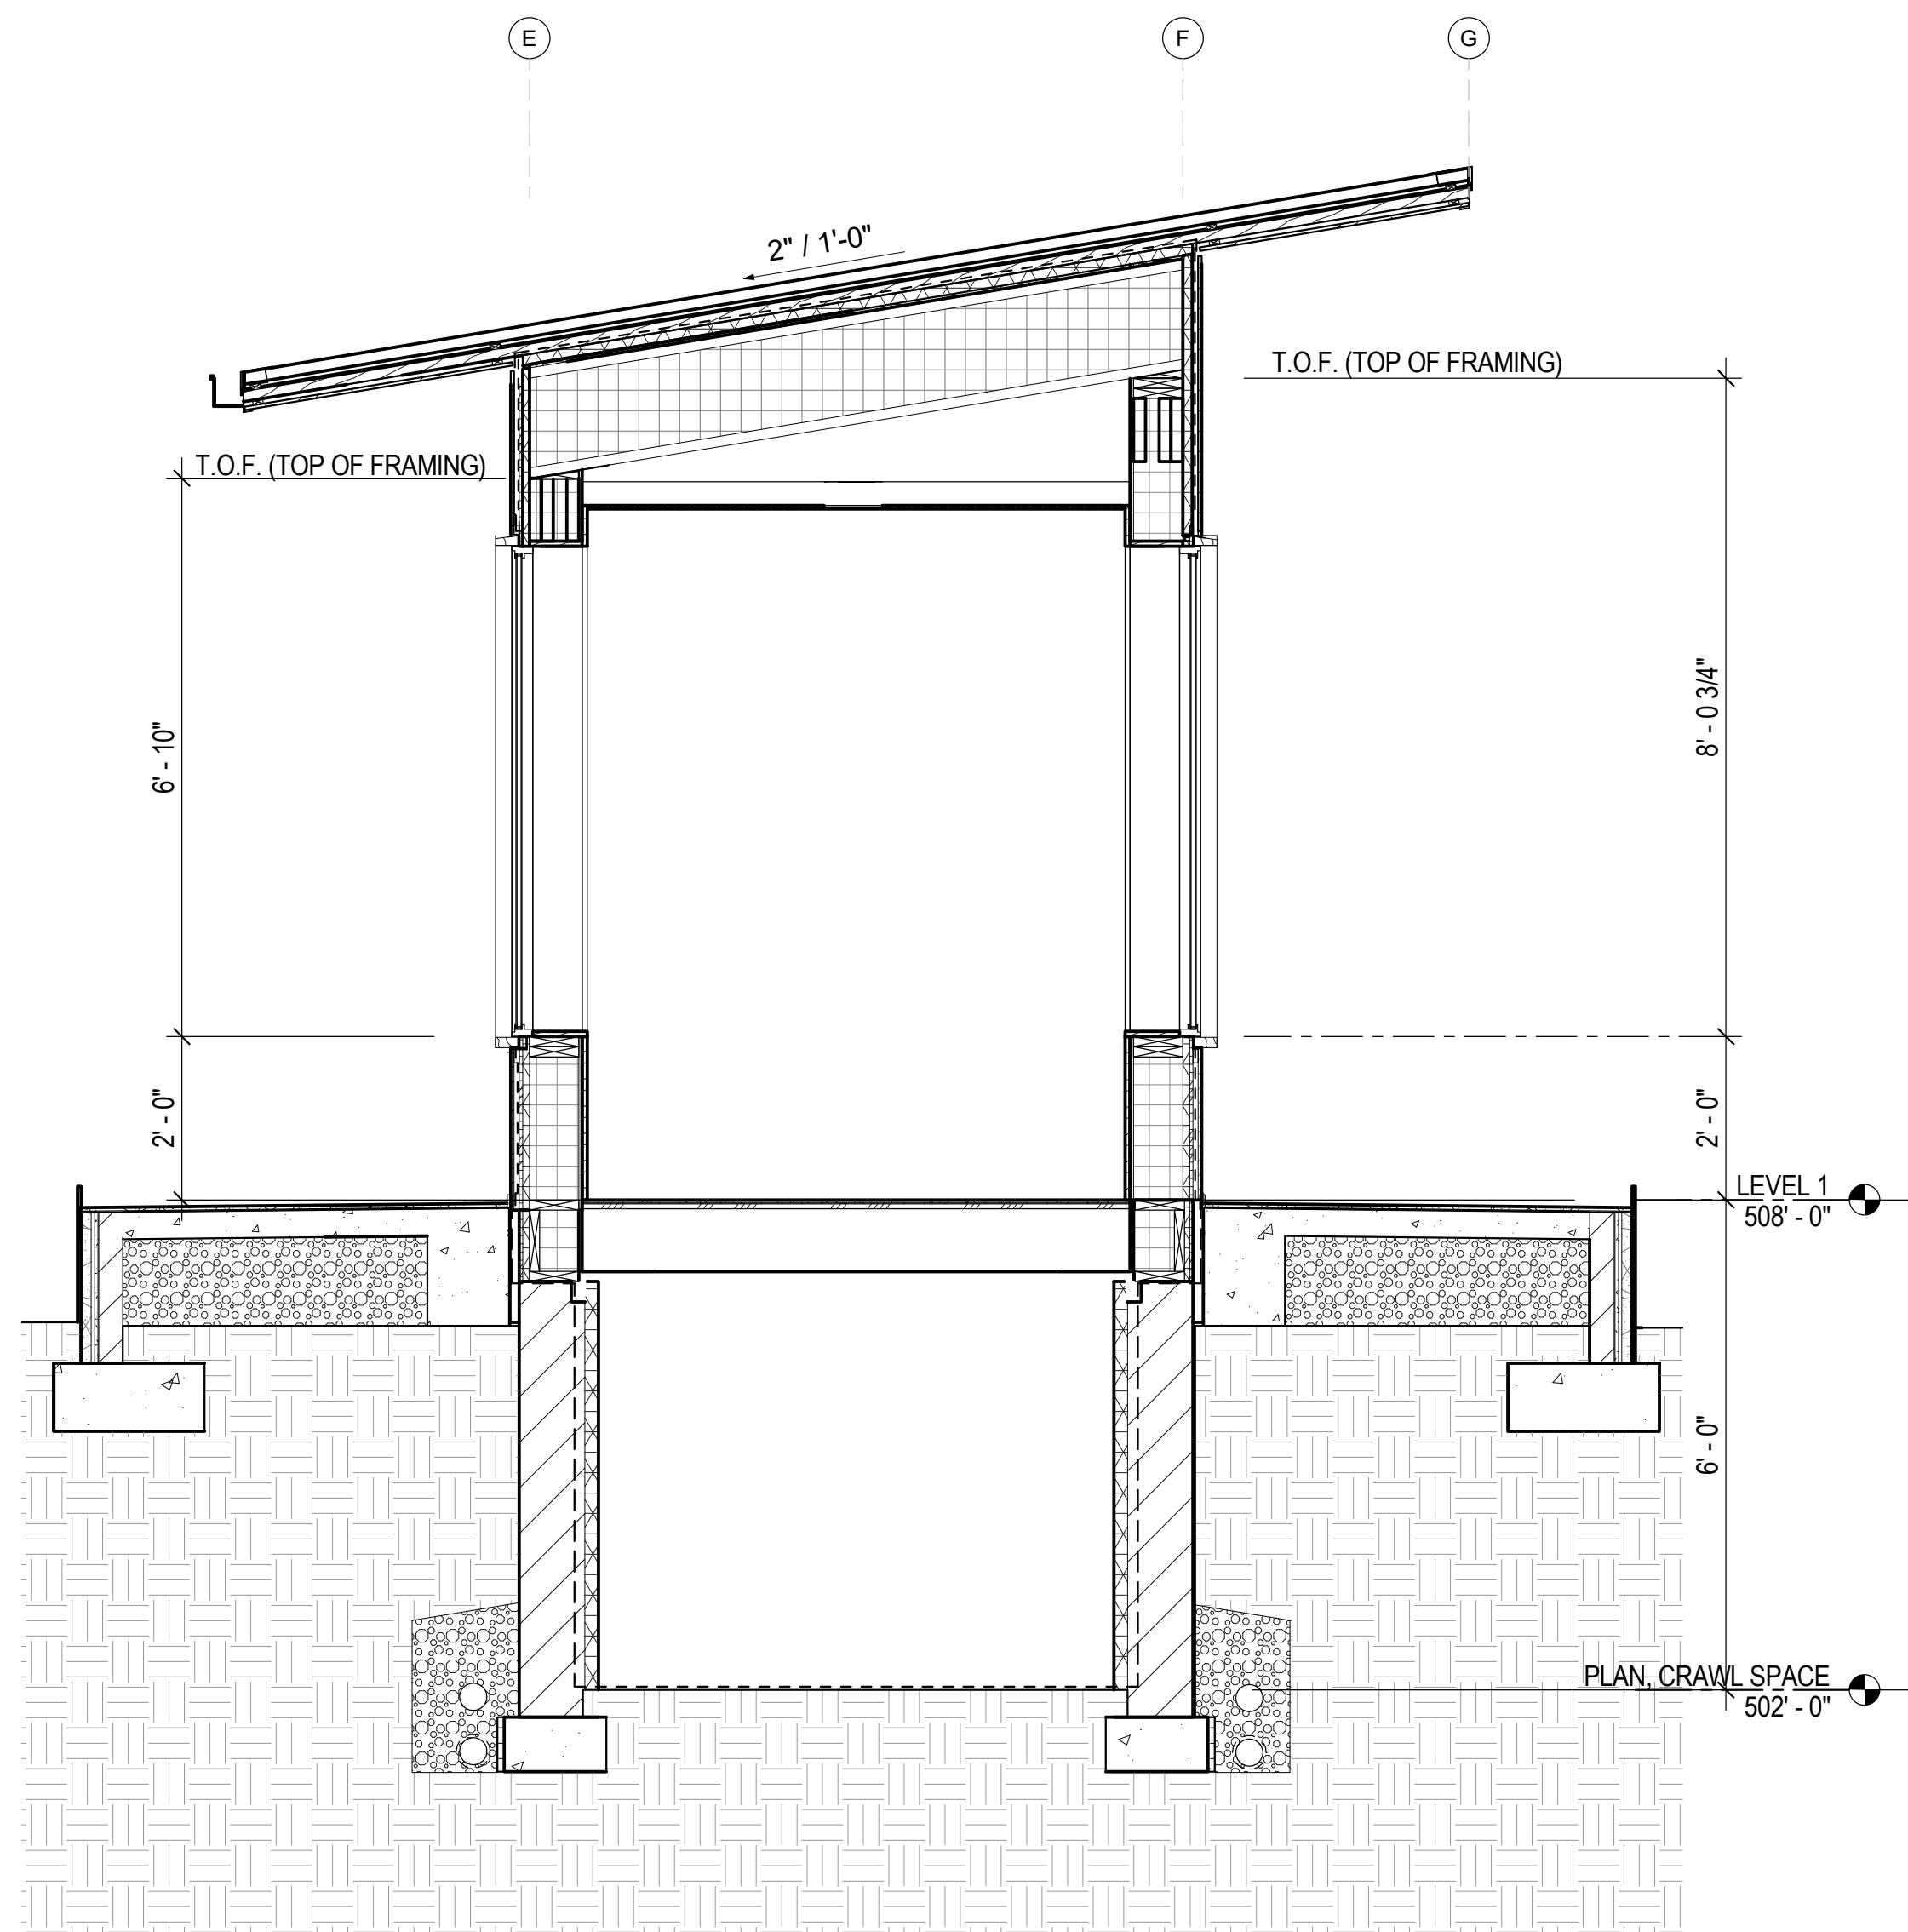


3 SECTION, ENTRY HALL
A3.20 1/2" = 1'-0"

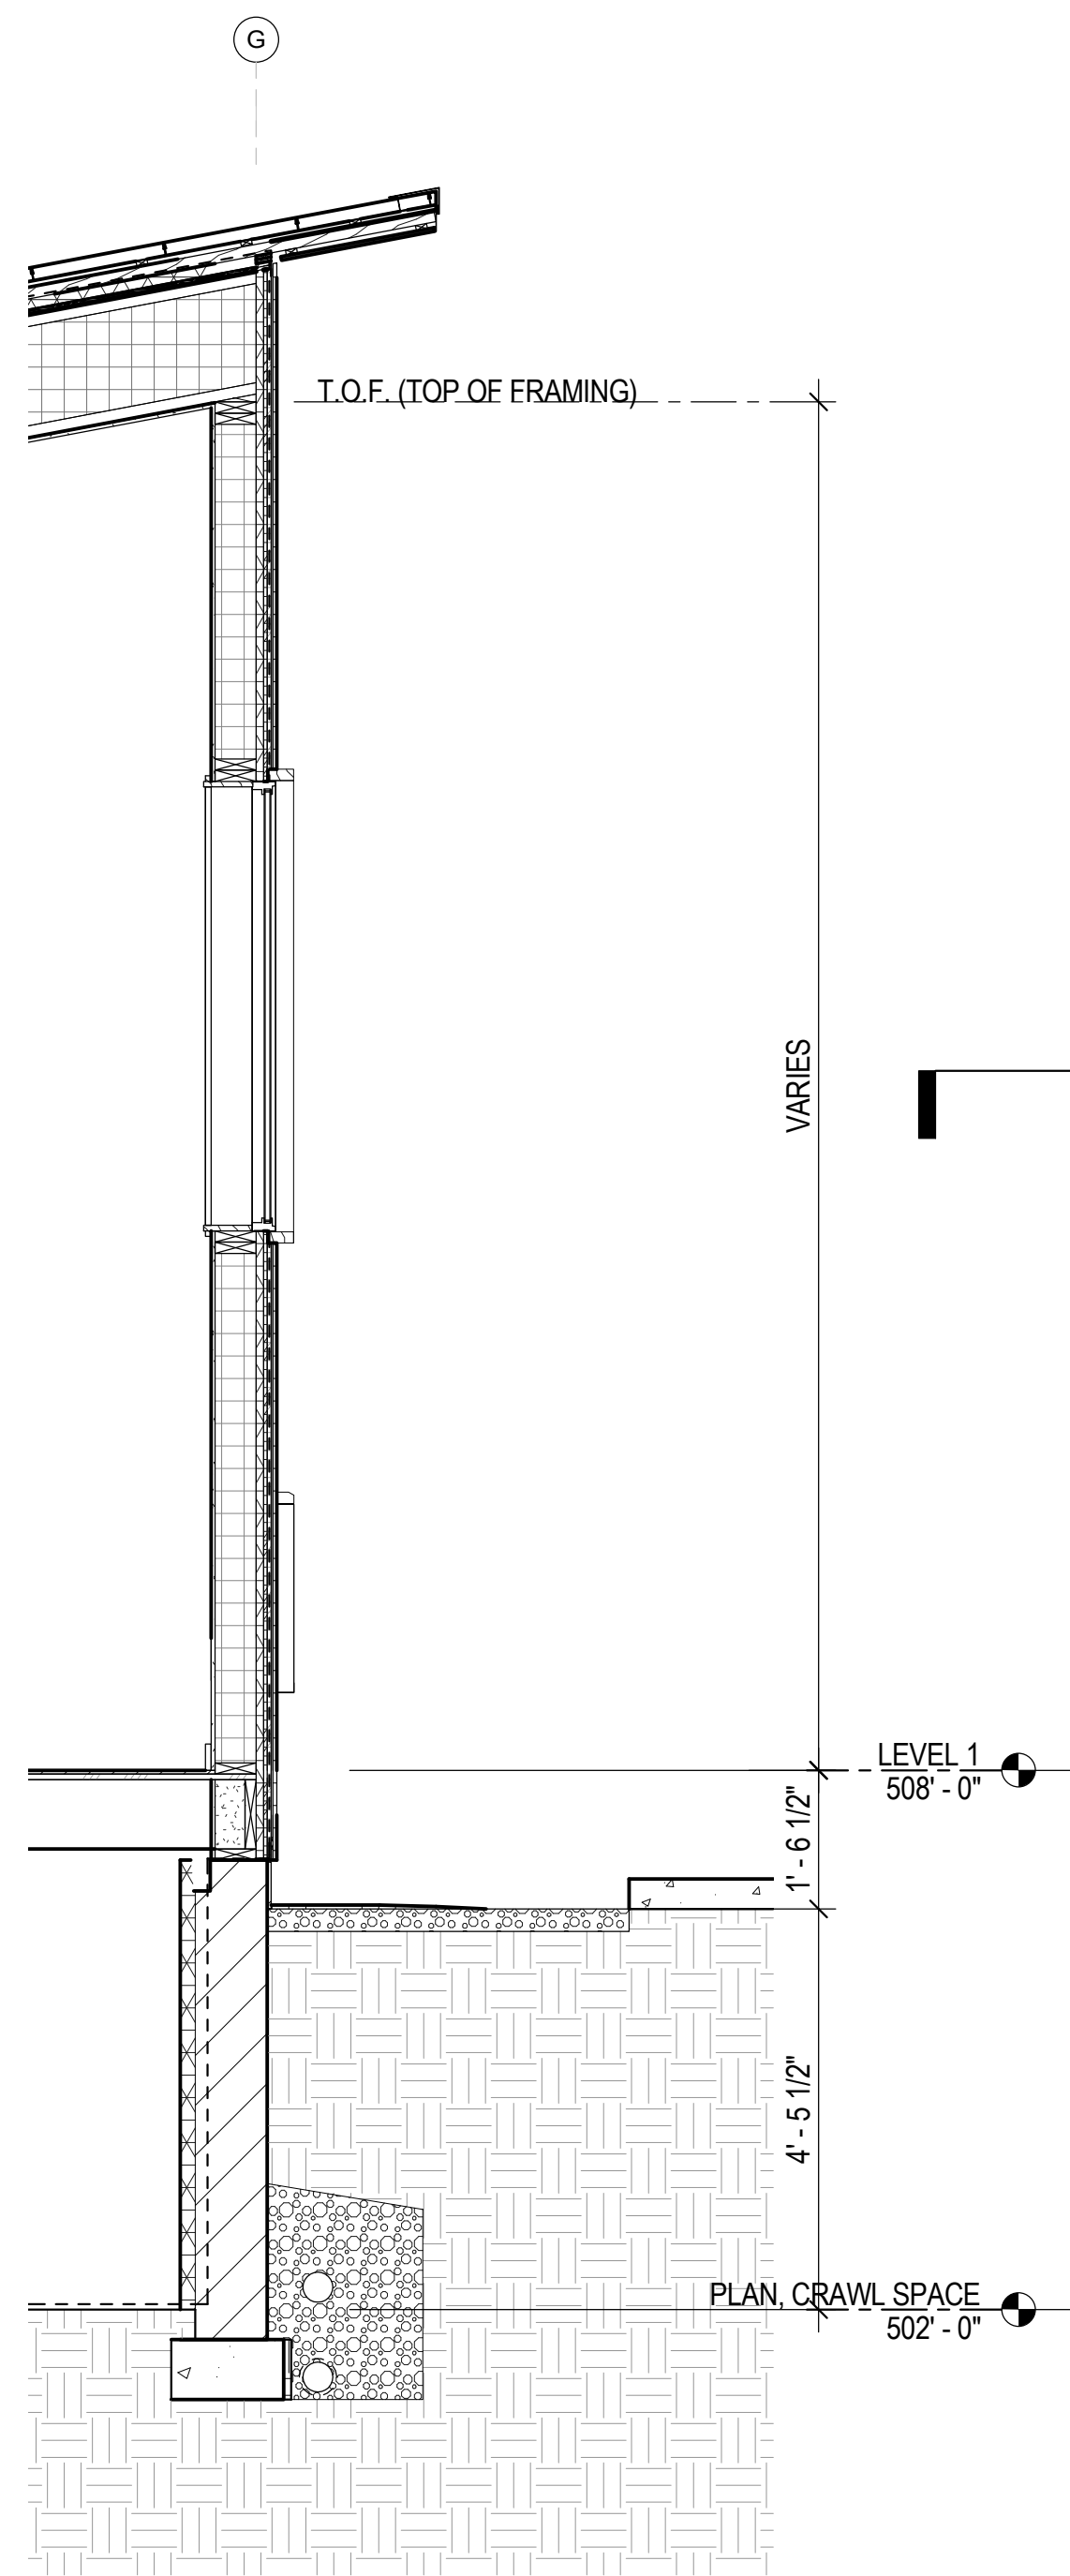


4 SECTION, TYPICAL
A3.20 1/2" = 1'-0"

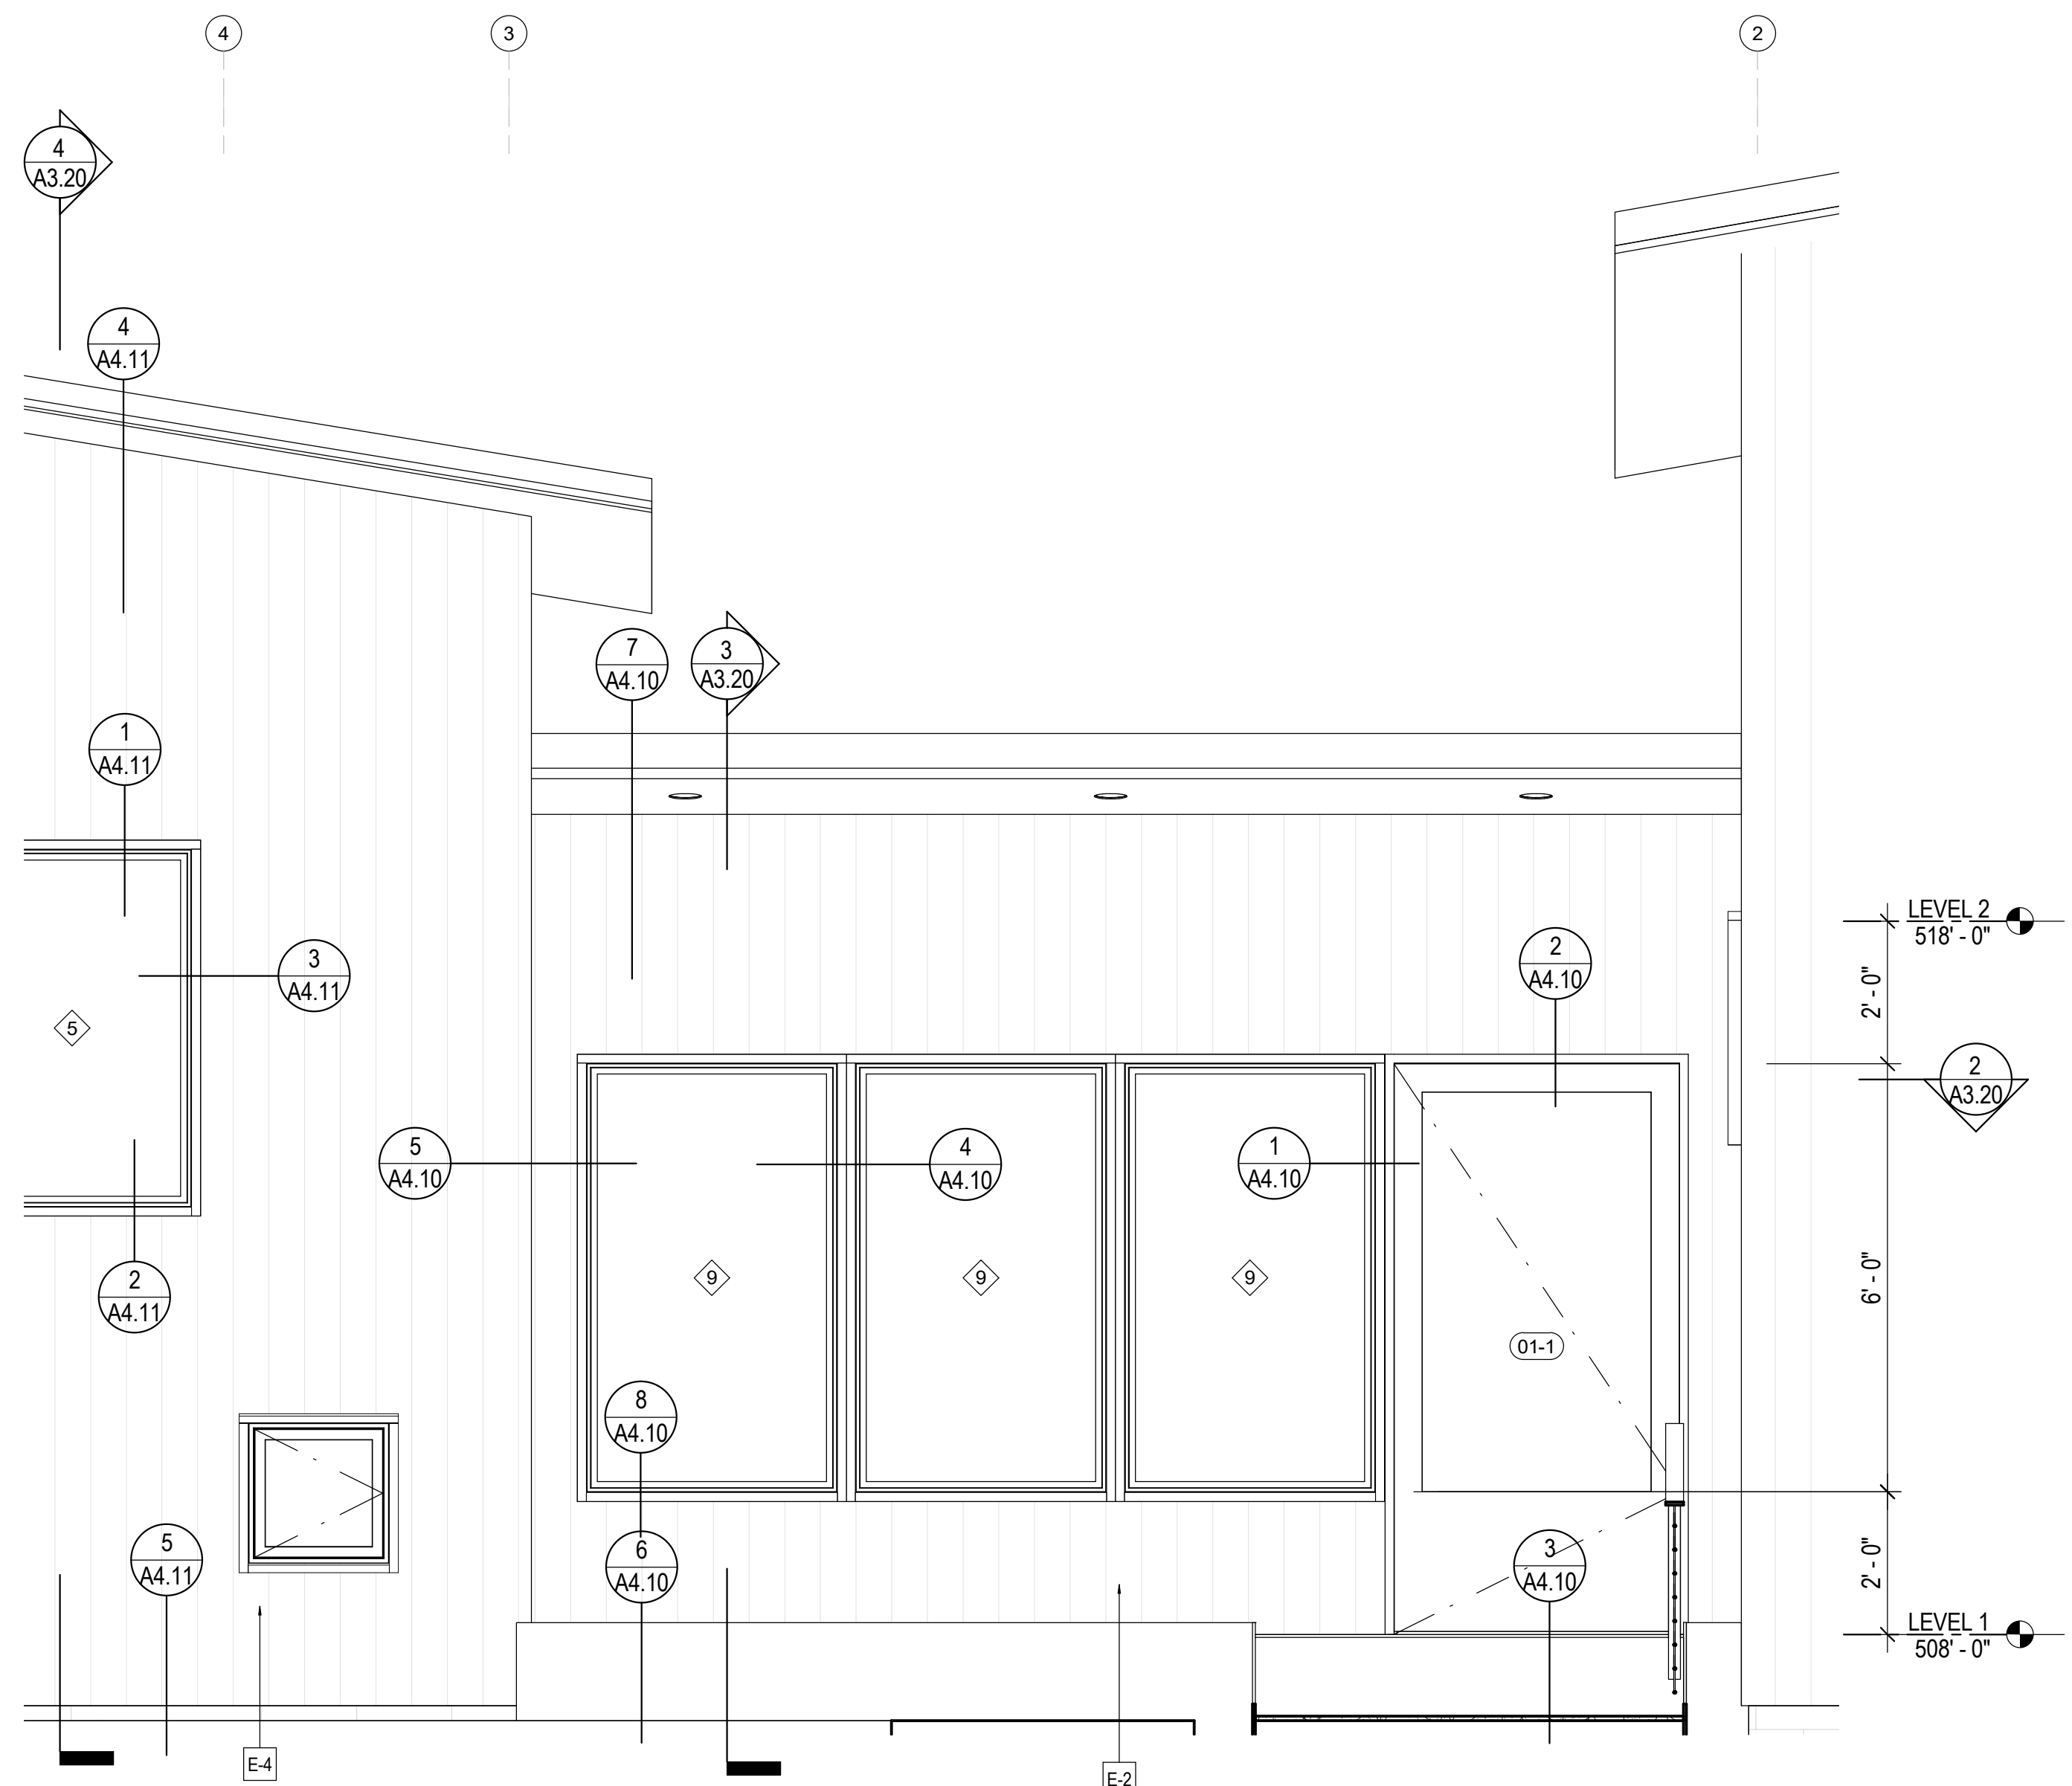


1 PARTIAL ELEVATION, ENTRY HALL, EAST
A3.20 1/2" = 1'-0"

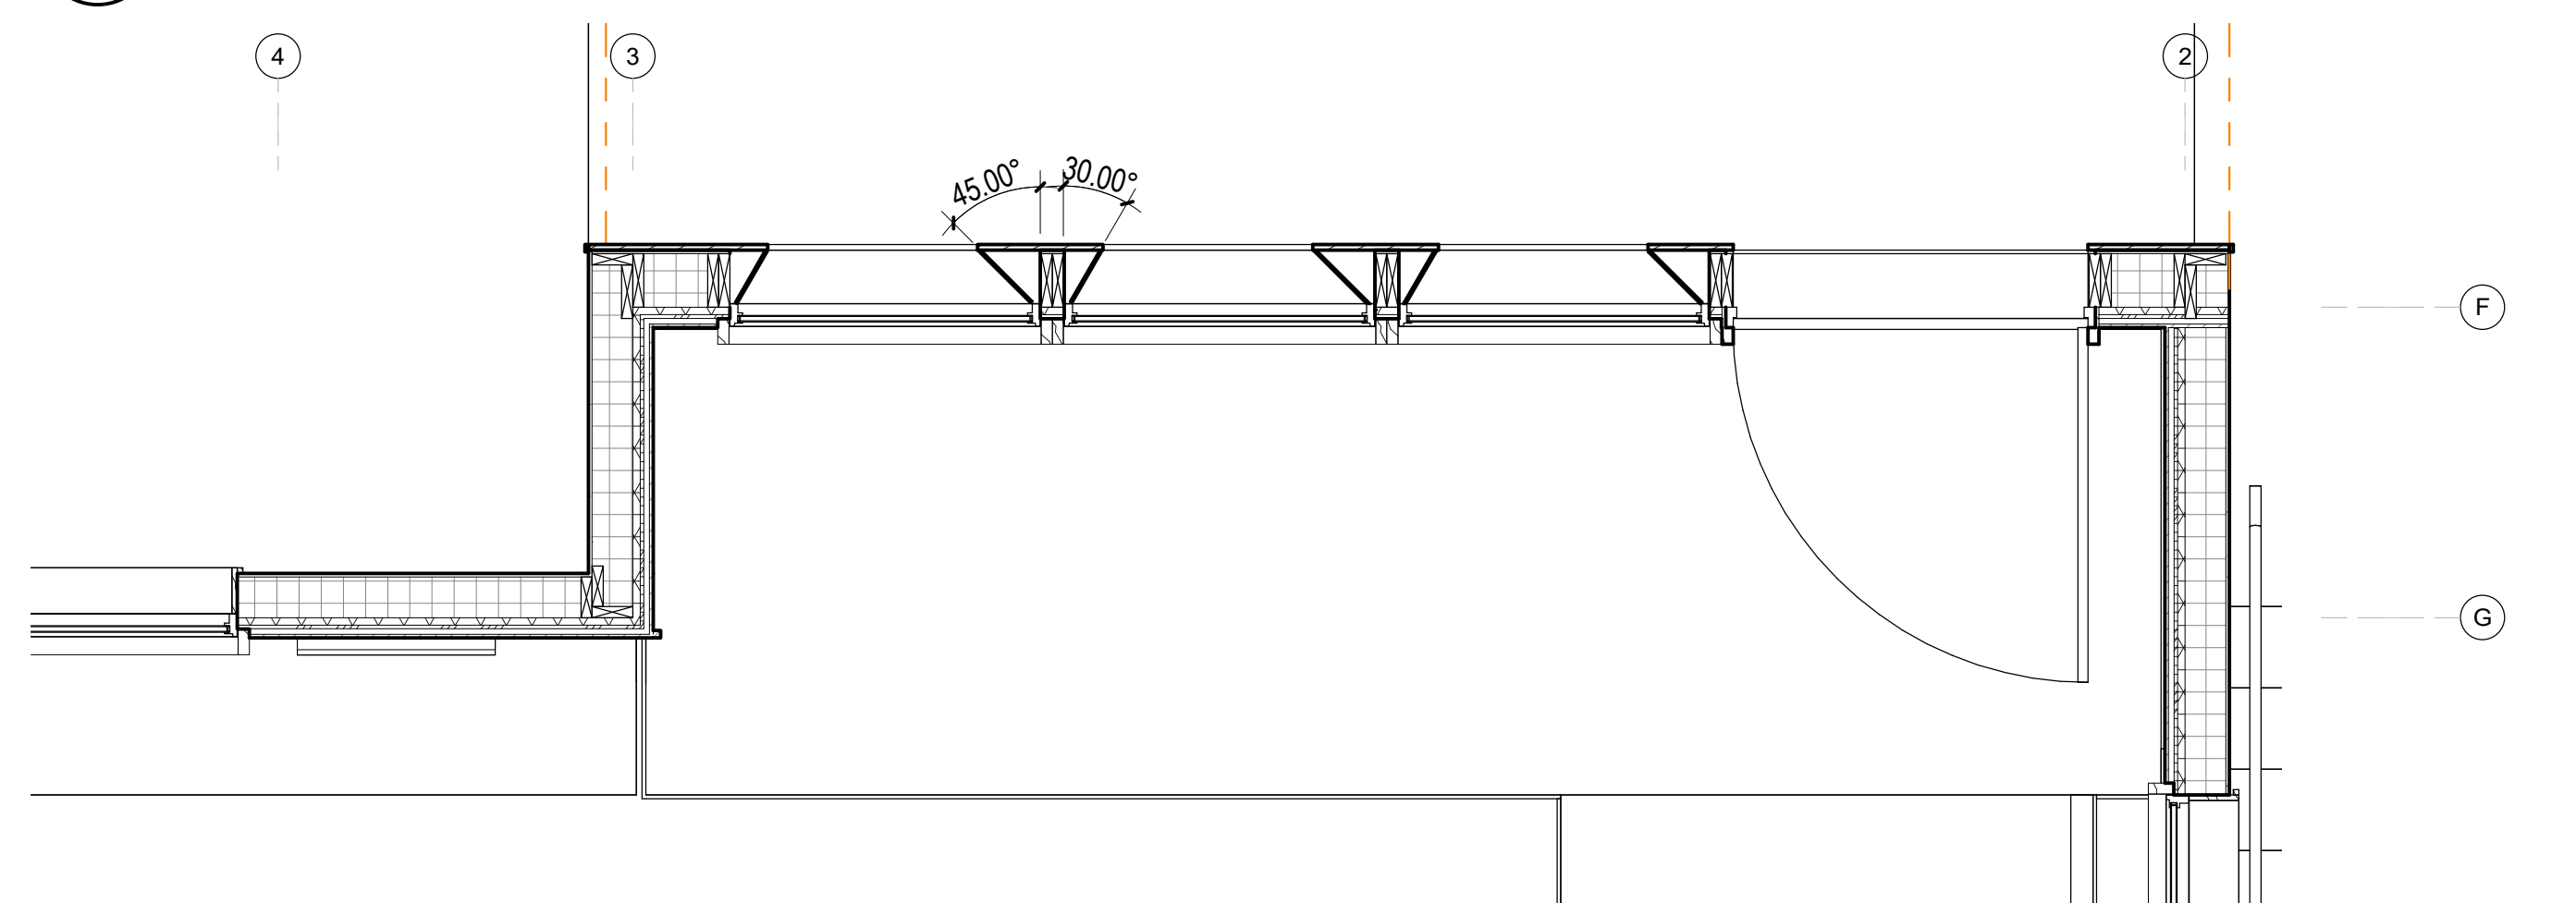


2 PLAN, ENLARGED, ENTRY HALL, EAST
A3.20 1/2" = 1'-0"

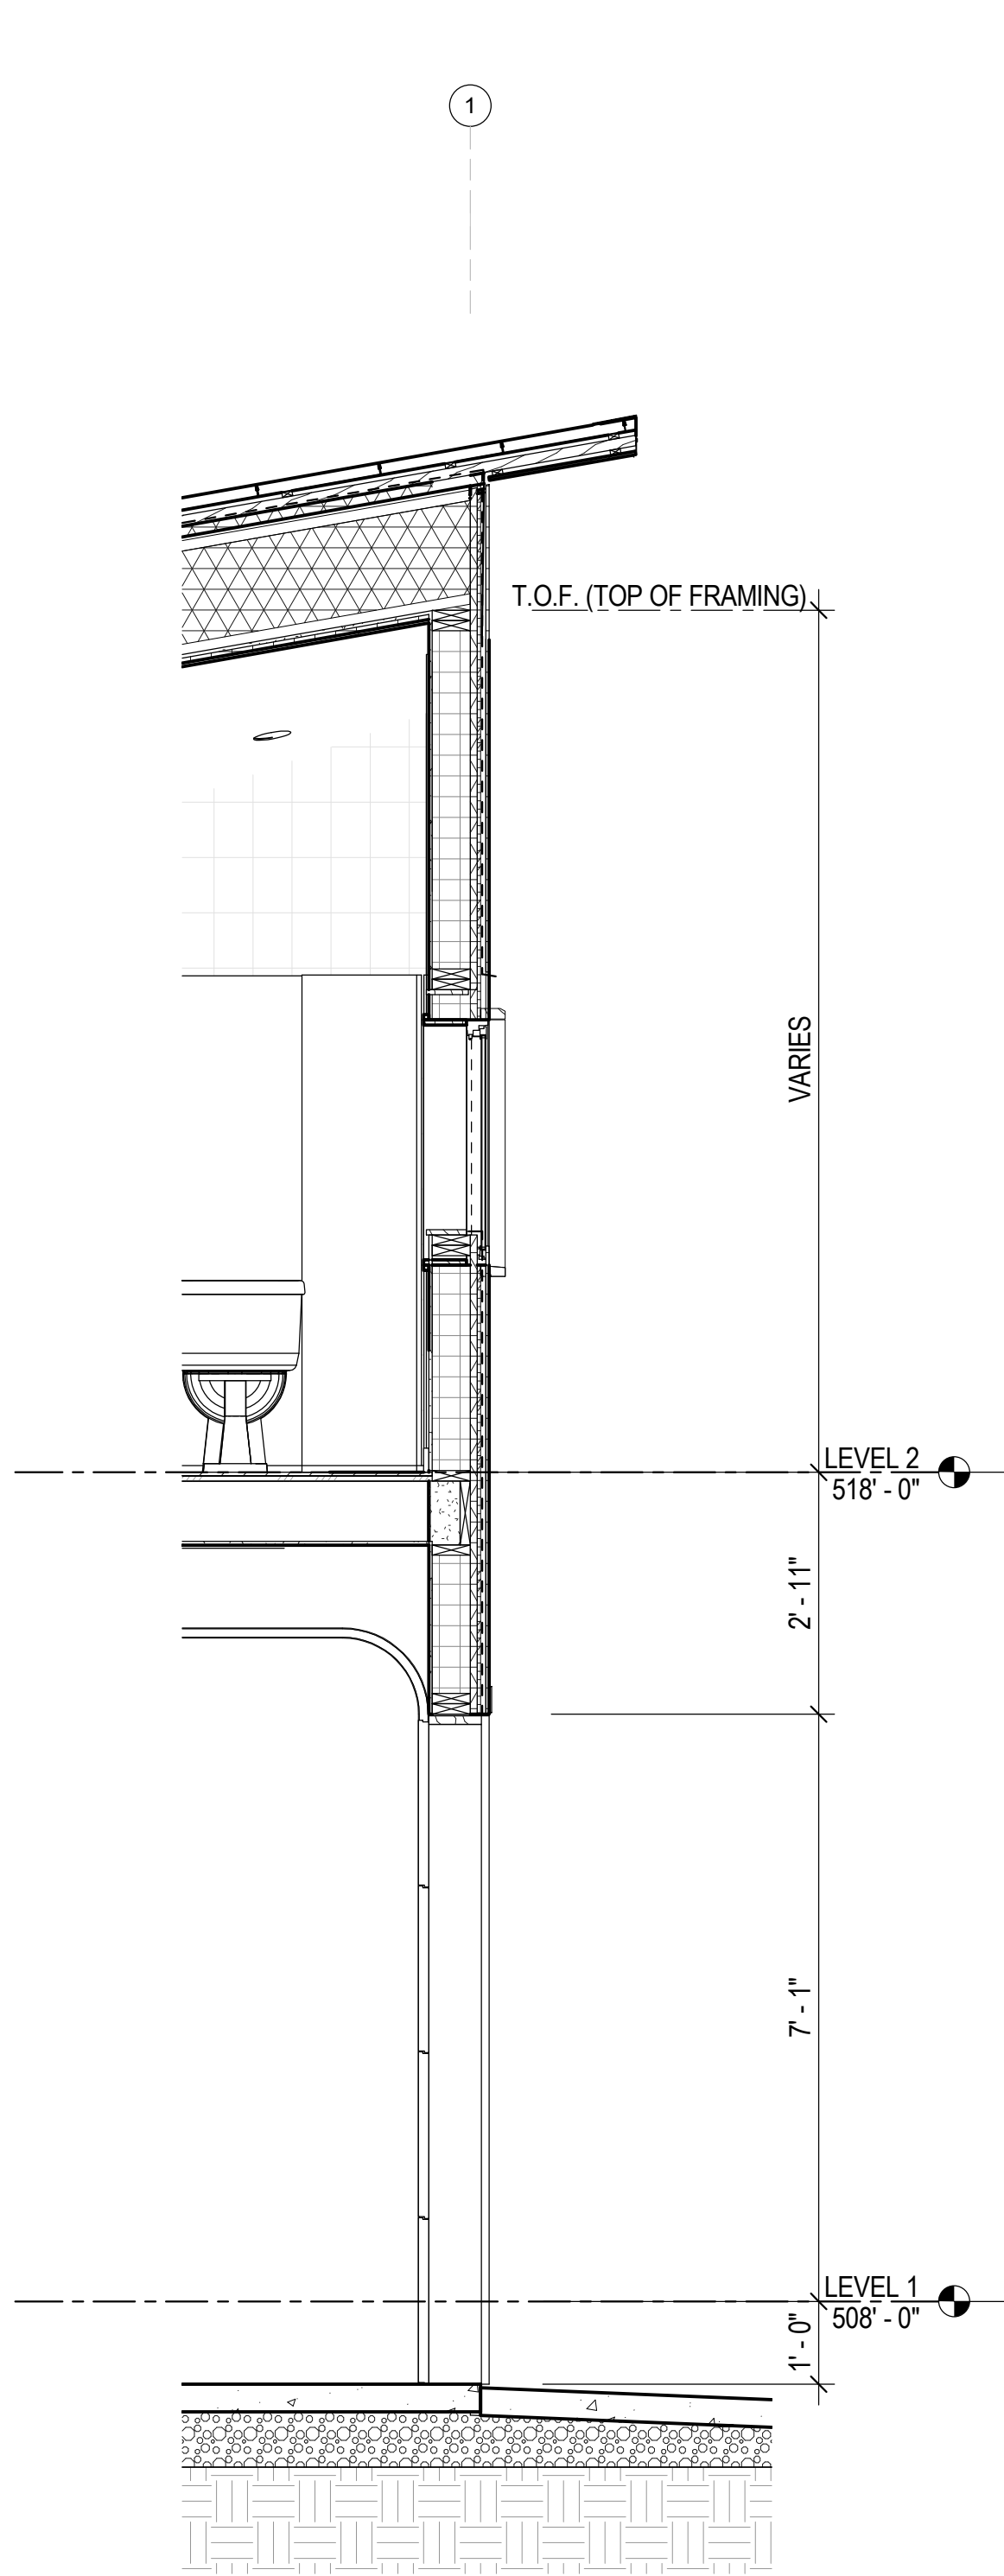


3 SECTION, GARAGE
A3.21 1/2" = 1'-0"

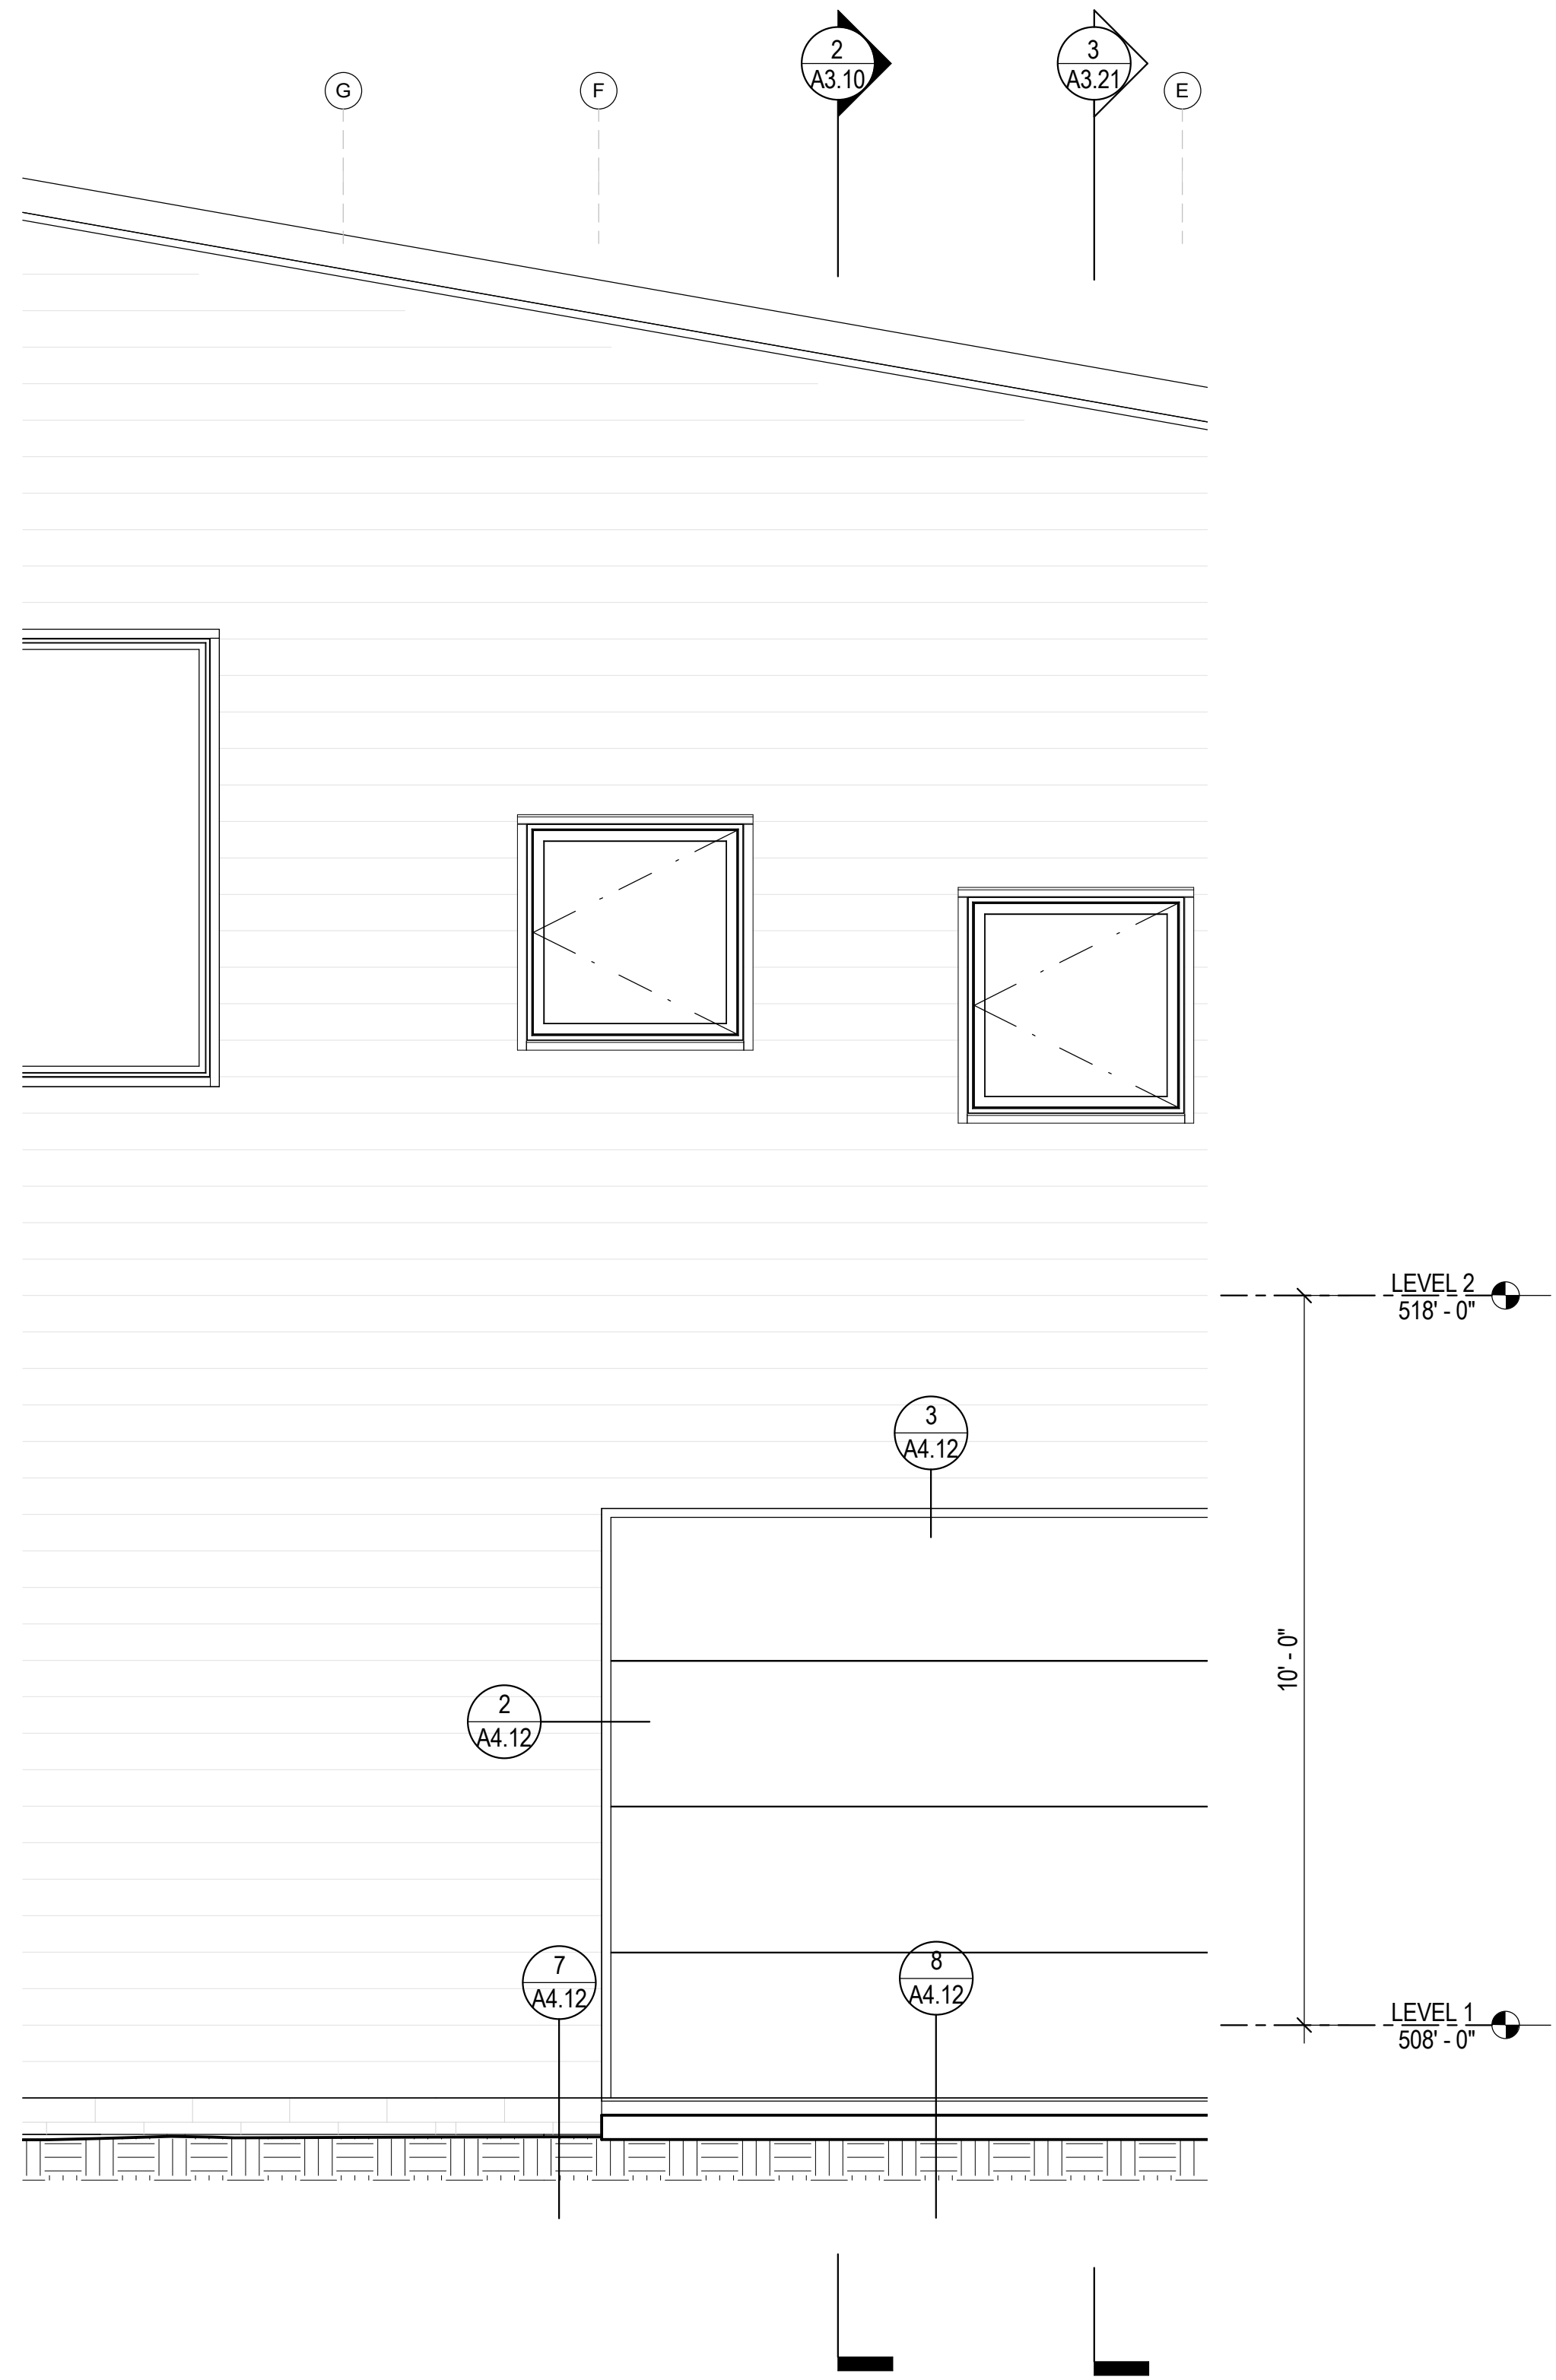


4 PARTIAL ELEVATION, GARAGE
A3.21 1/2" = 1'-0"

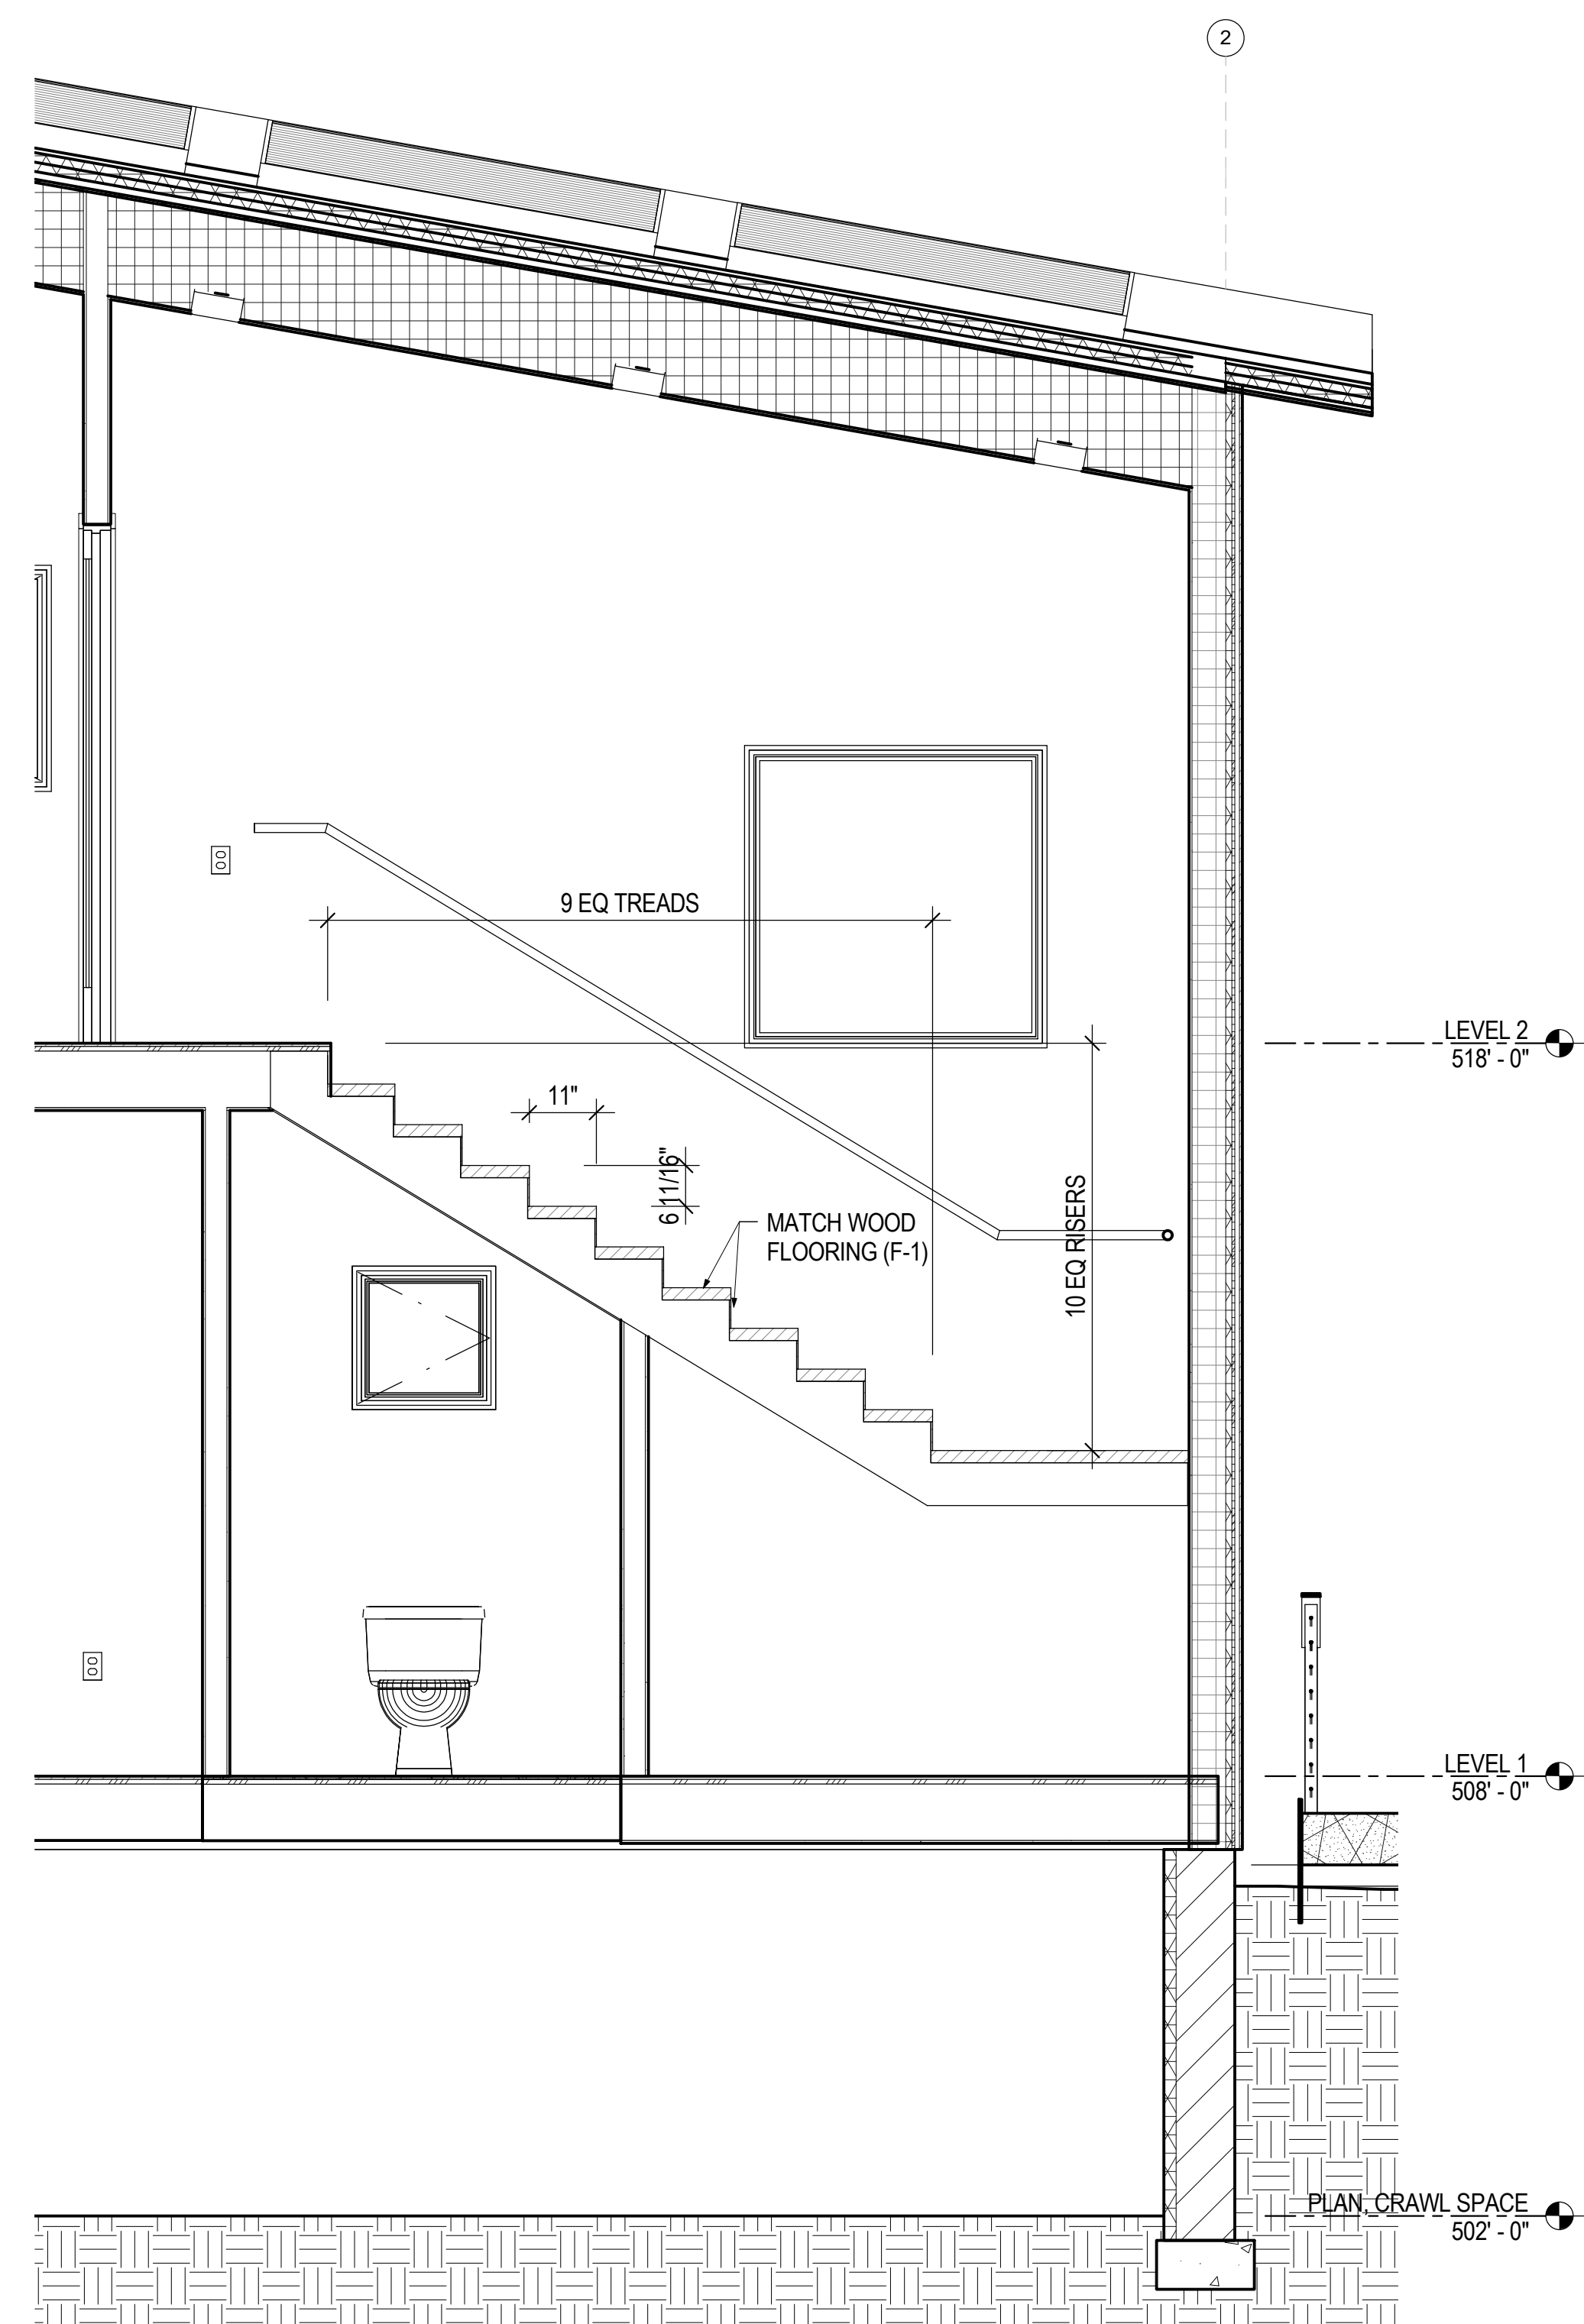


1
A3.22
SECTION, STAIRS EAST
1/2" = 1'-0"

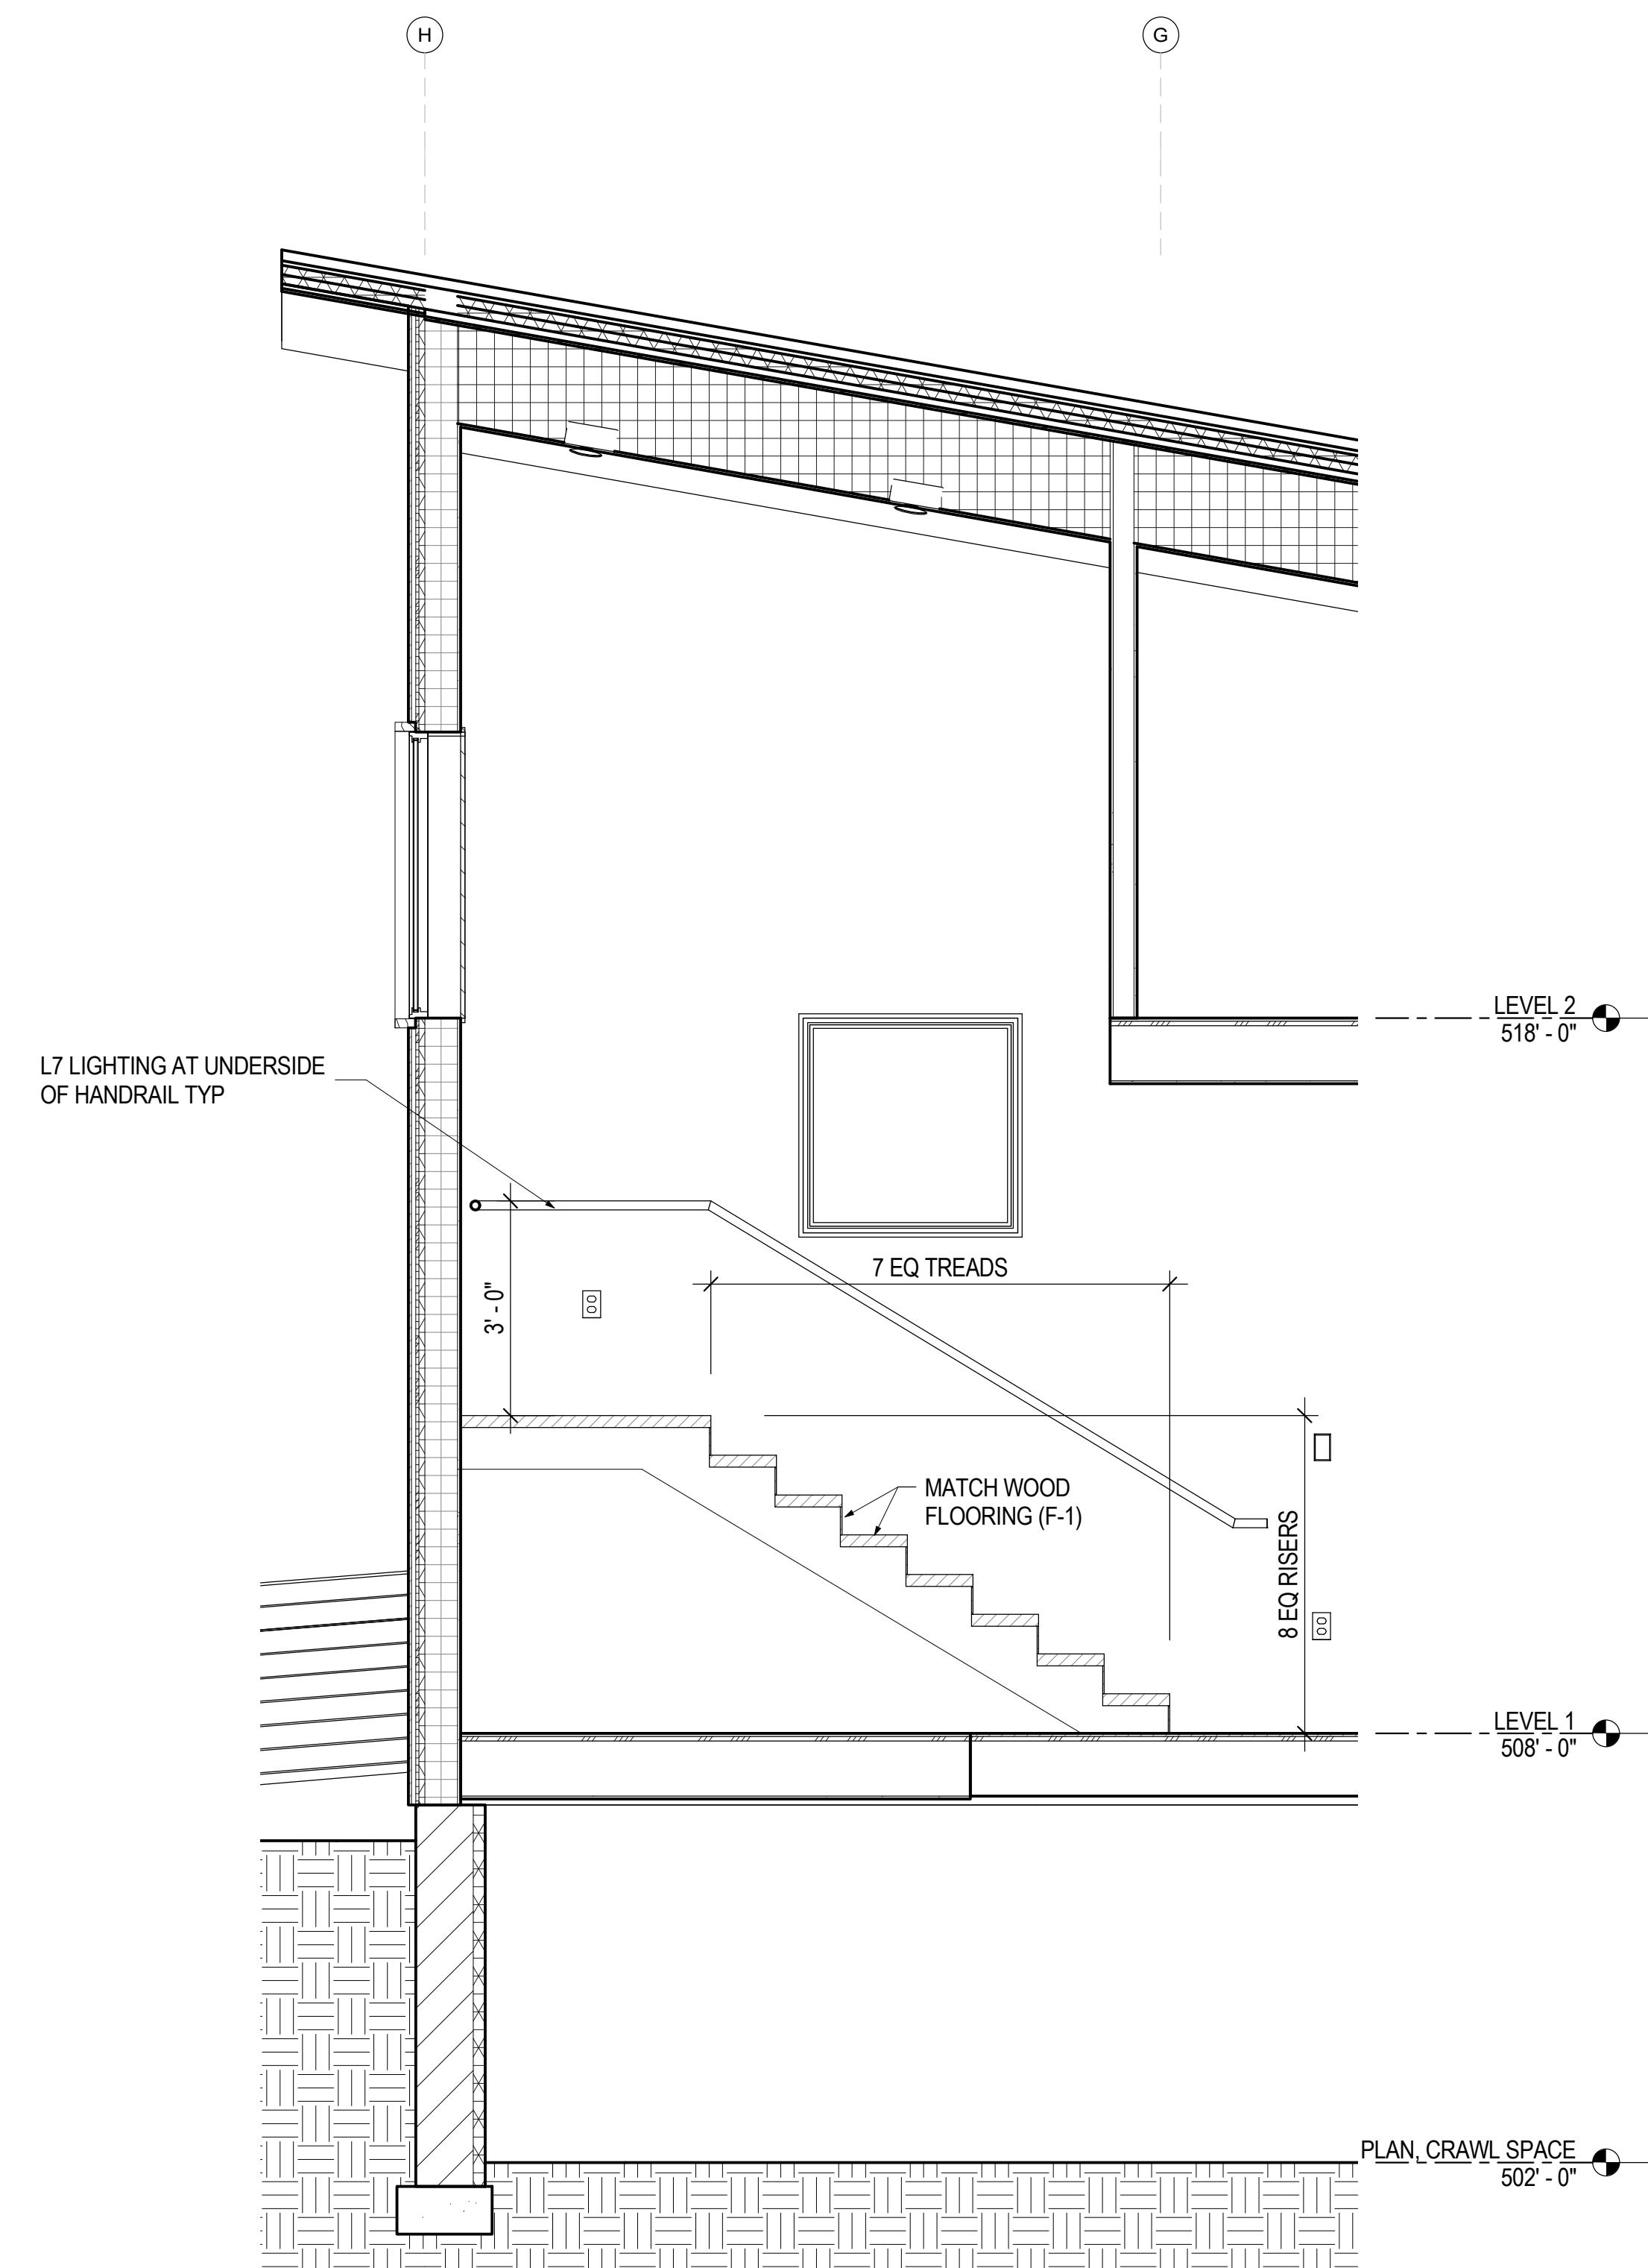


2
A3.22
SECTION, STAIRS SOUTH
1/2" = 1'-0"

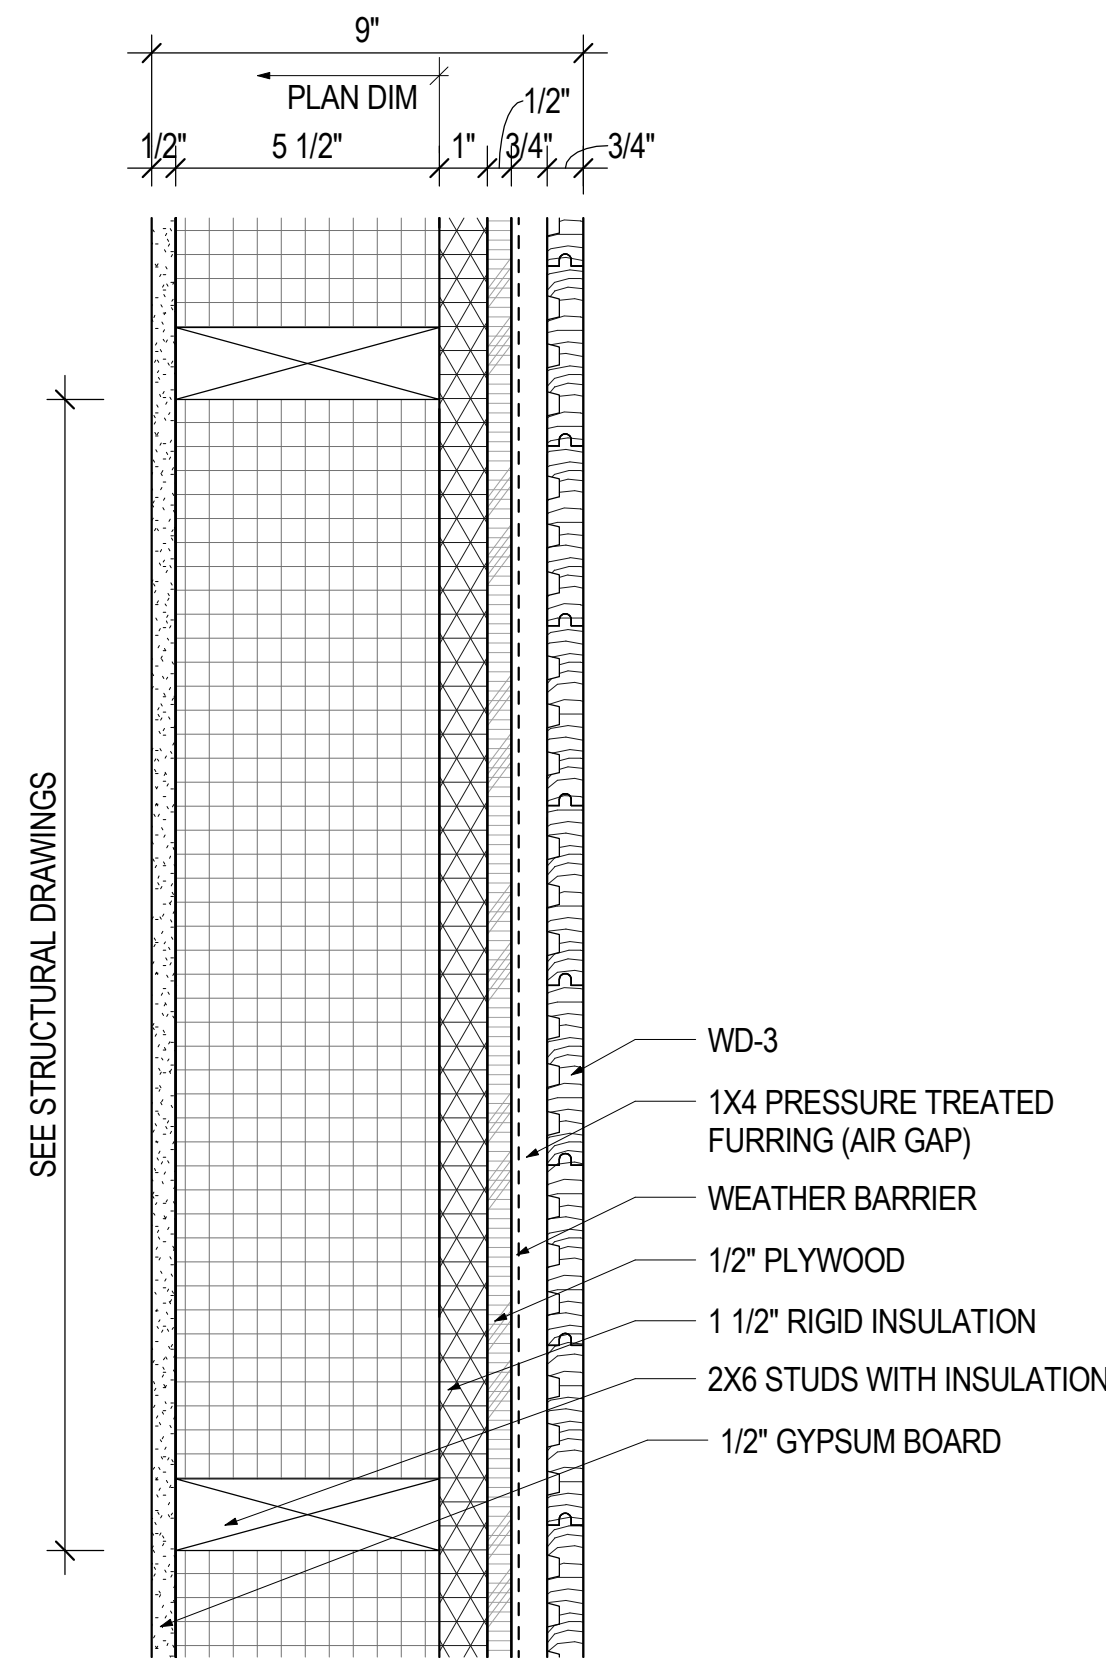


E-4 EXTERIOR WALL, WOOD
3" = 1'-0"

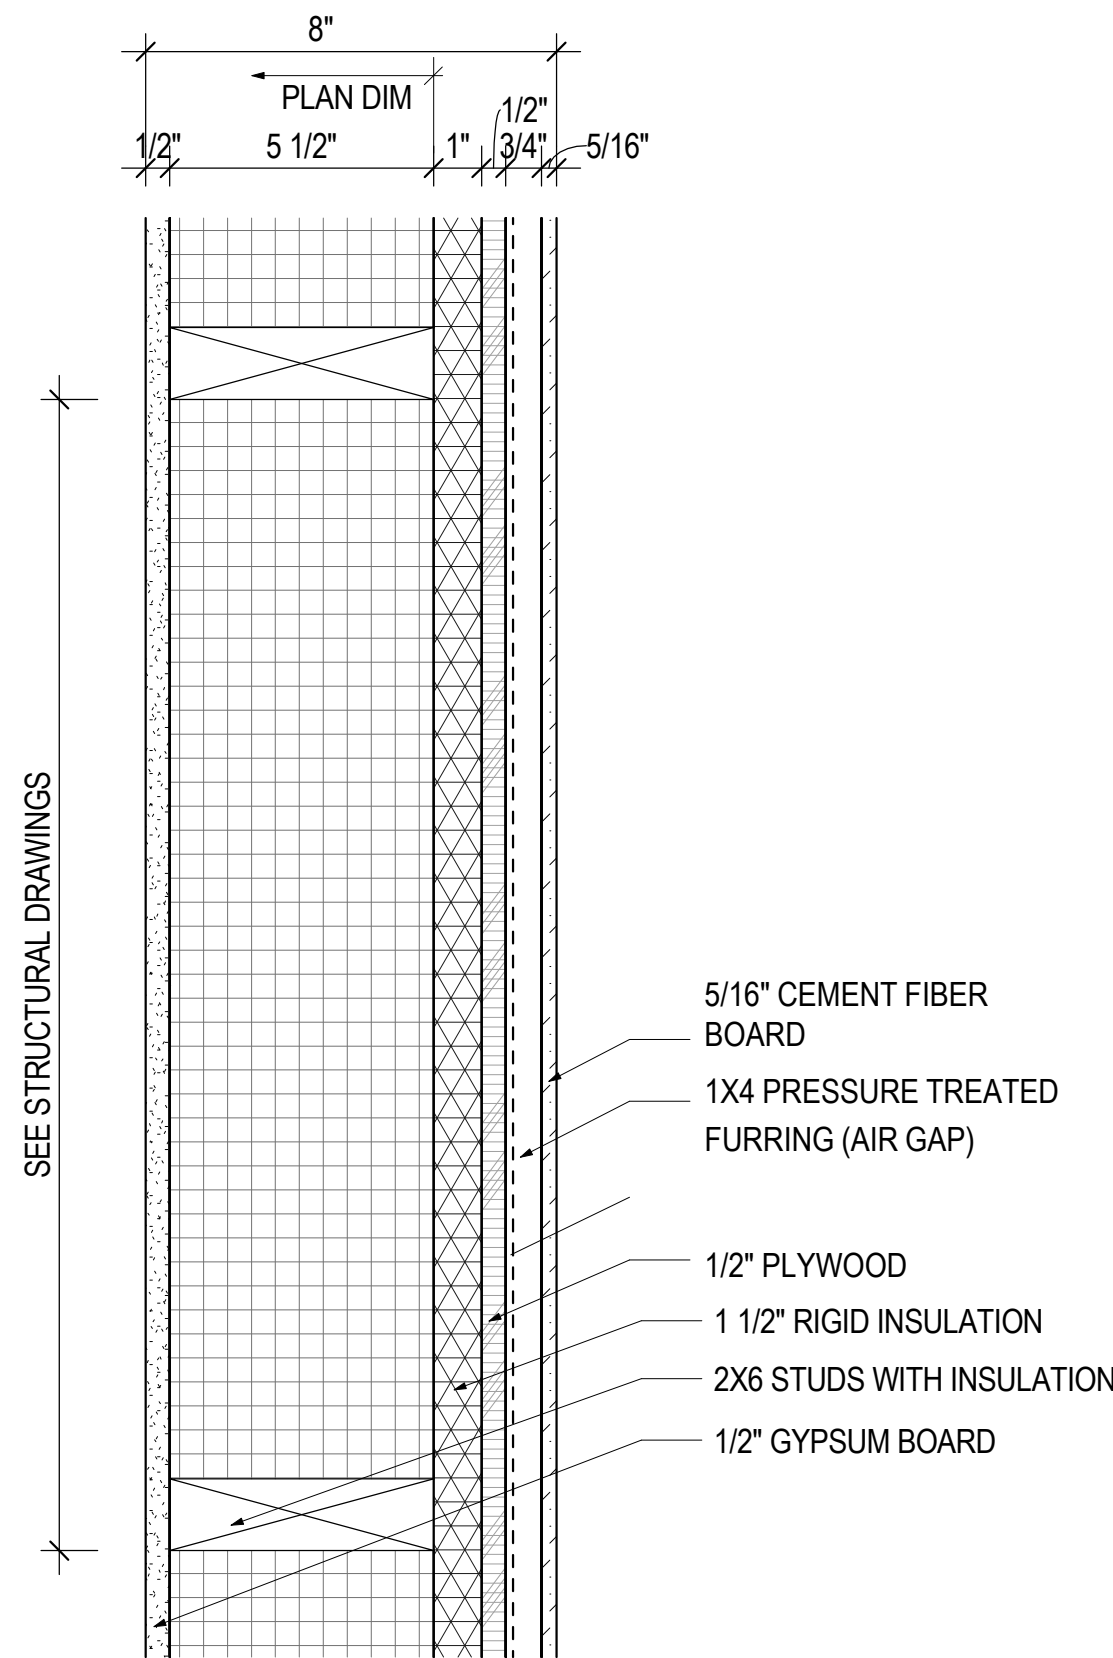


E-3 EXTERIOR WALL, FIBERBOARD
3" = 1'-0"

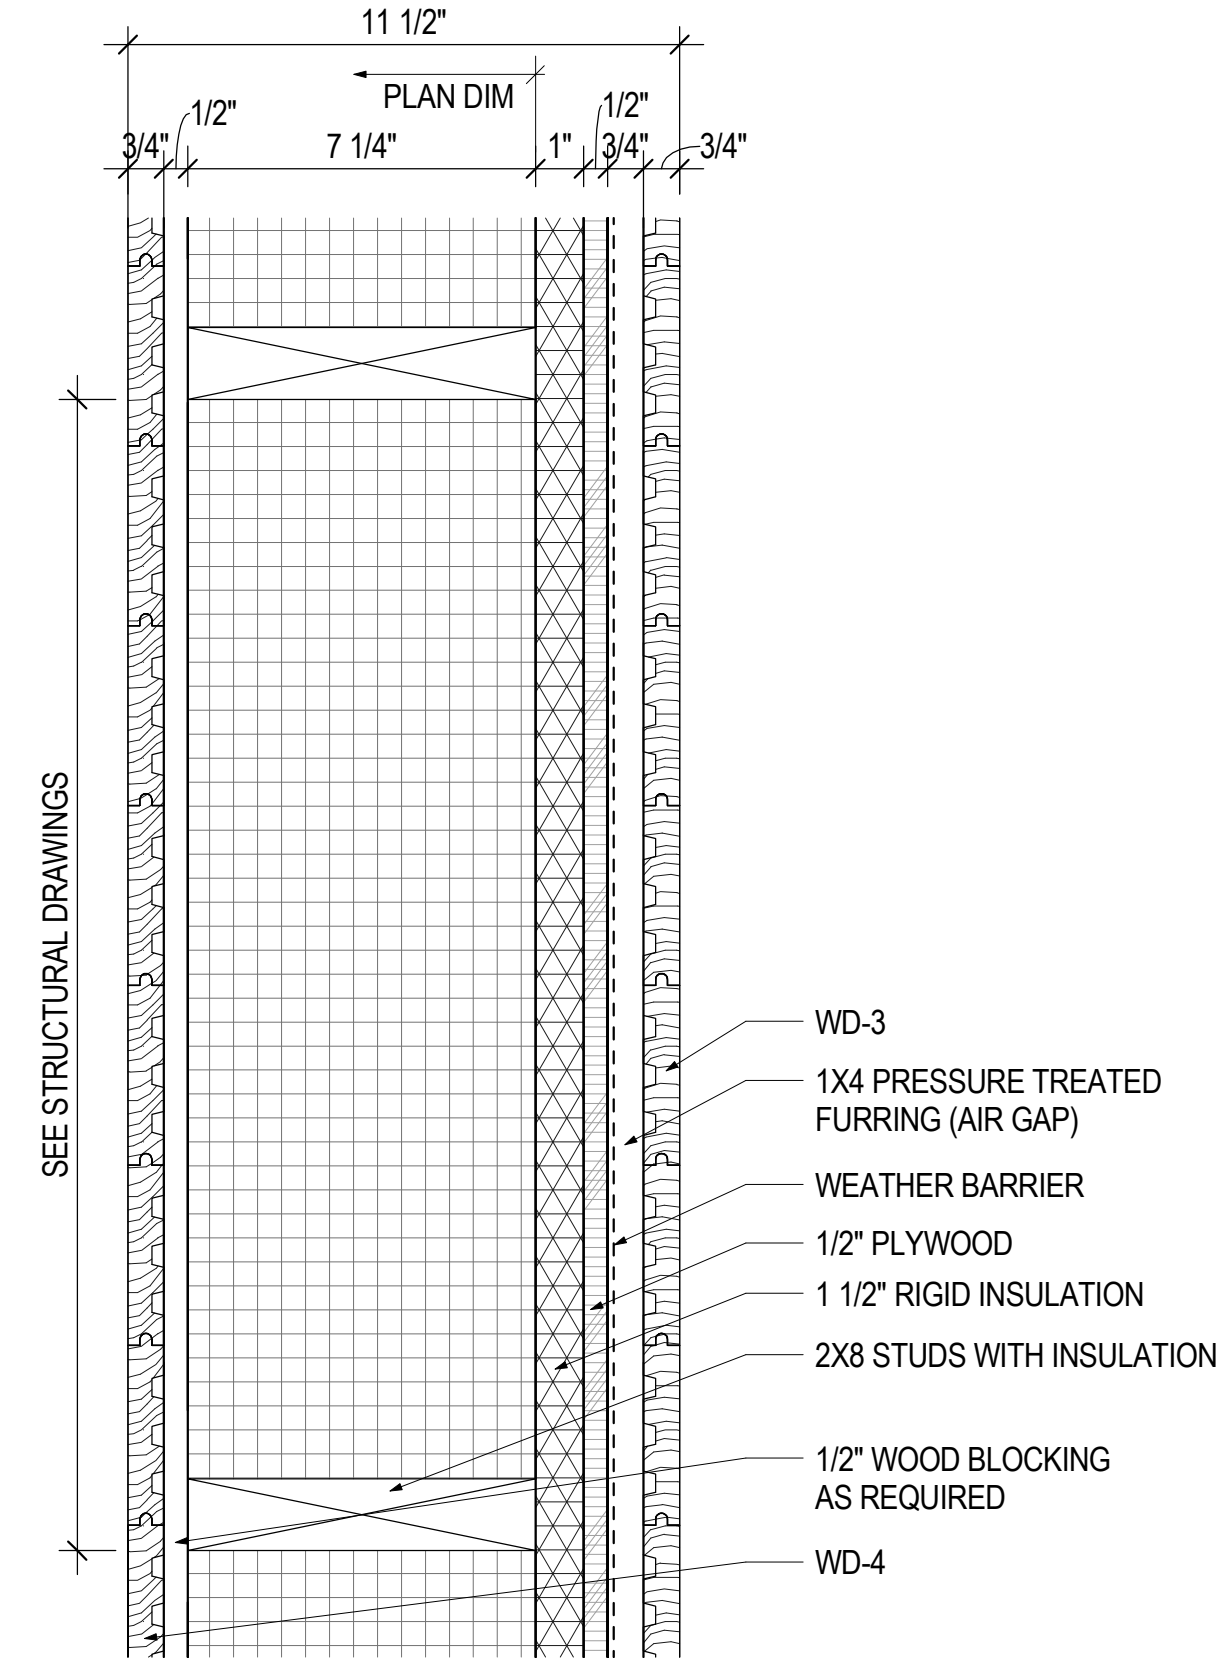


E-2 EXTERIOR WALL, WOOD CONNECTOR
3" = 1'-0"

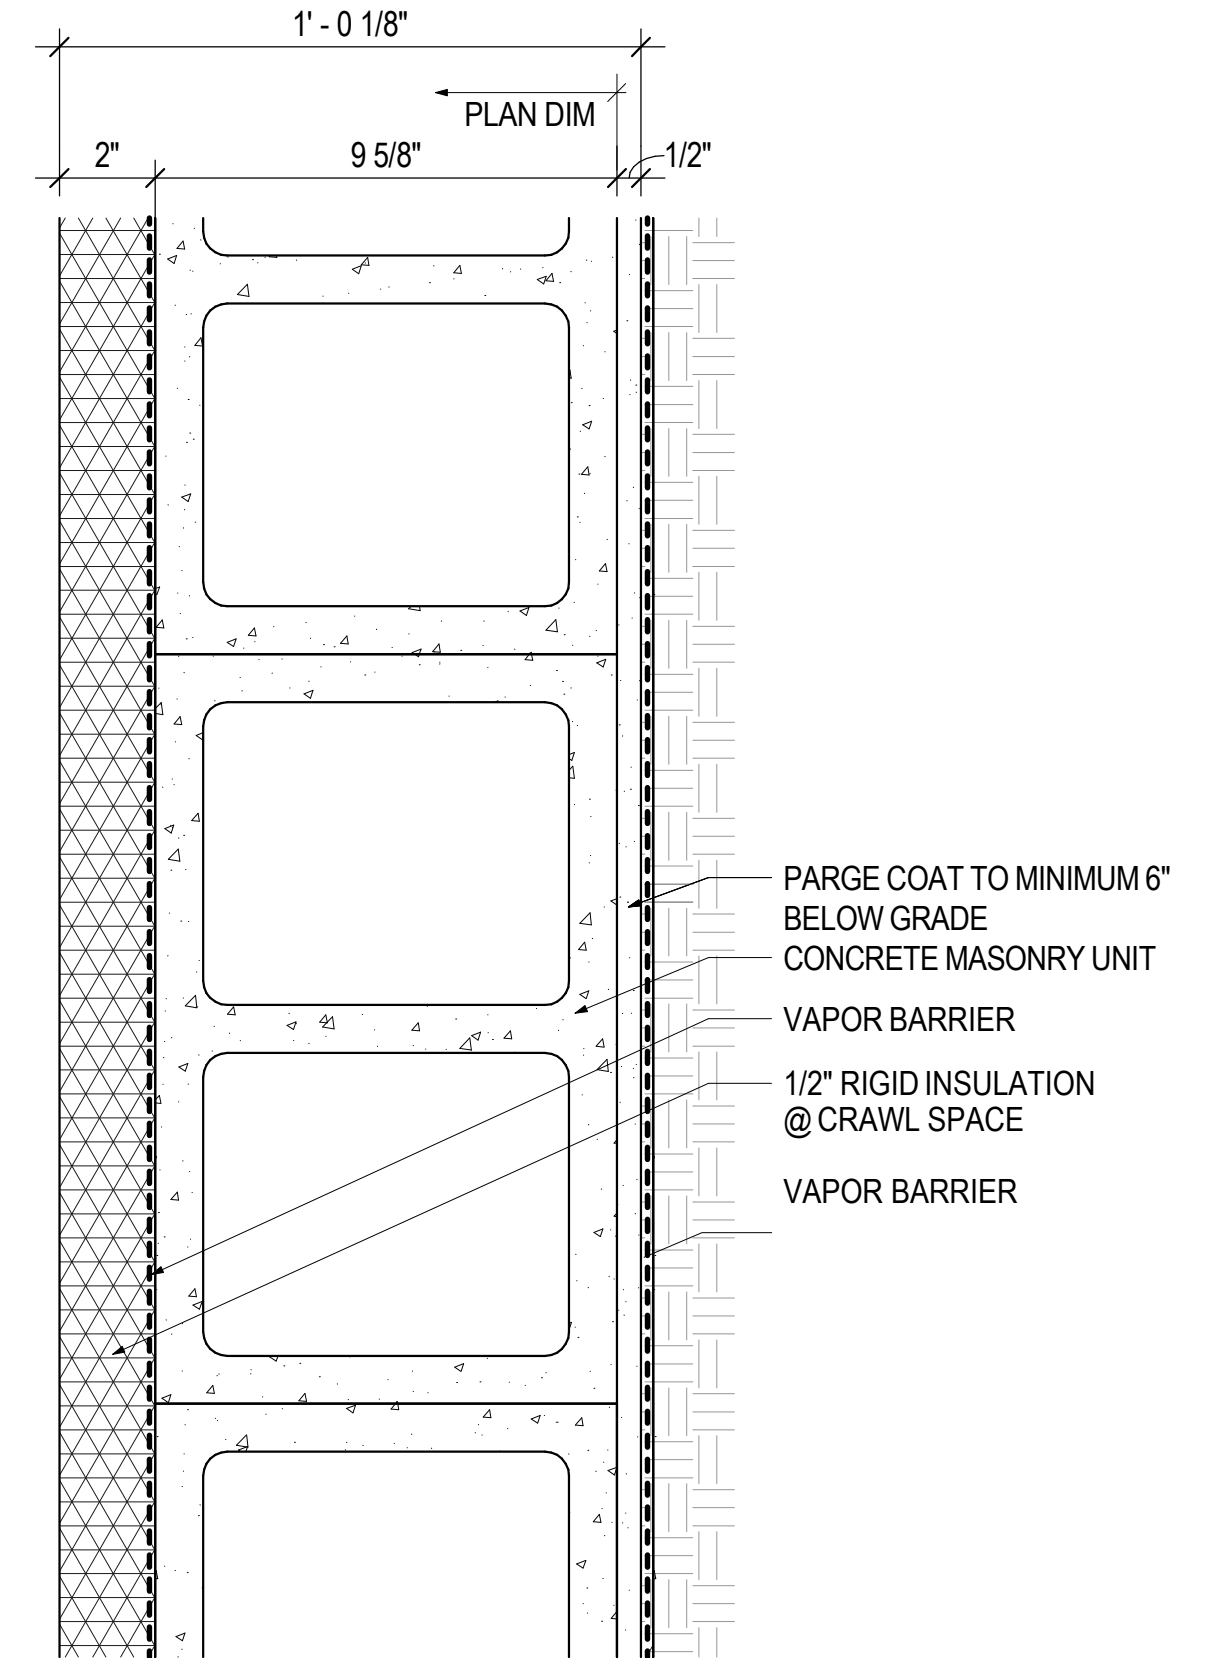


E-1 EXTERIOR WALL, CMU
3" = 1'-0"

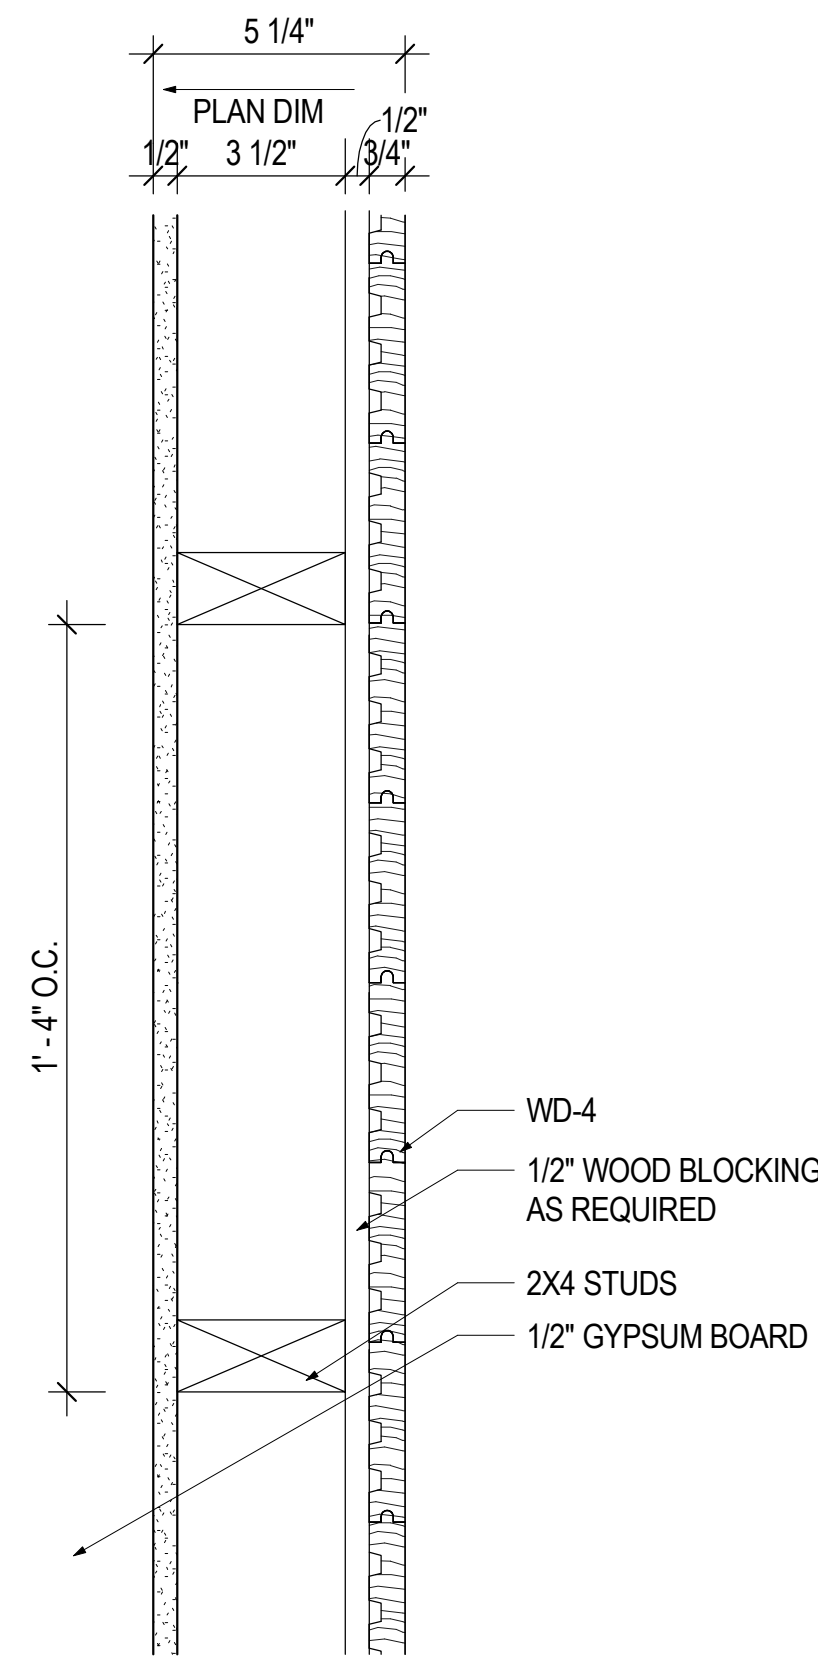


W-4 INTERIOR WALL, 2X4 WOOD VENEER
3" = 1'-0"

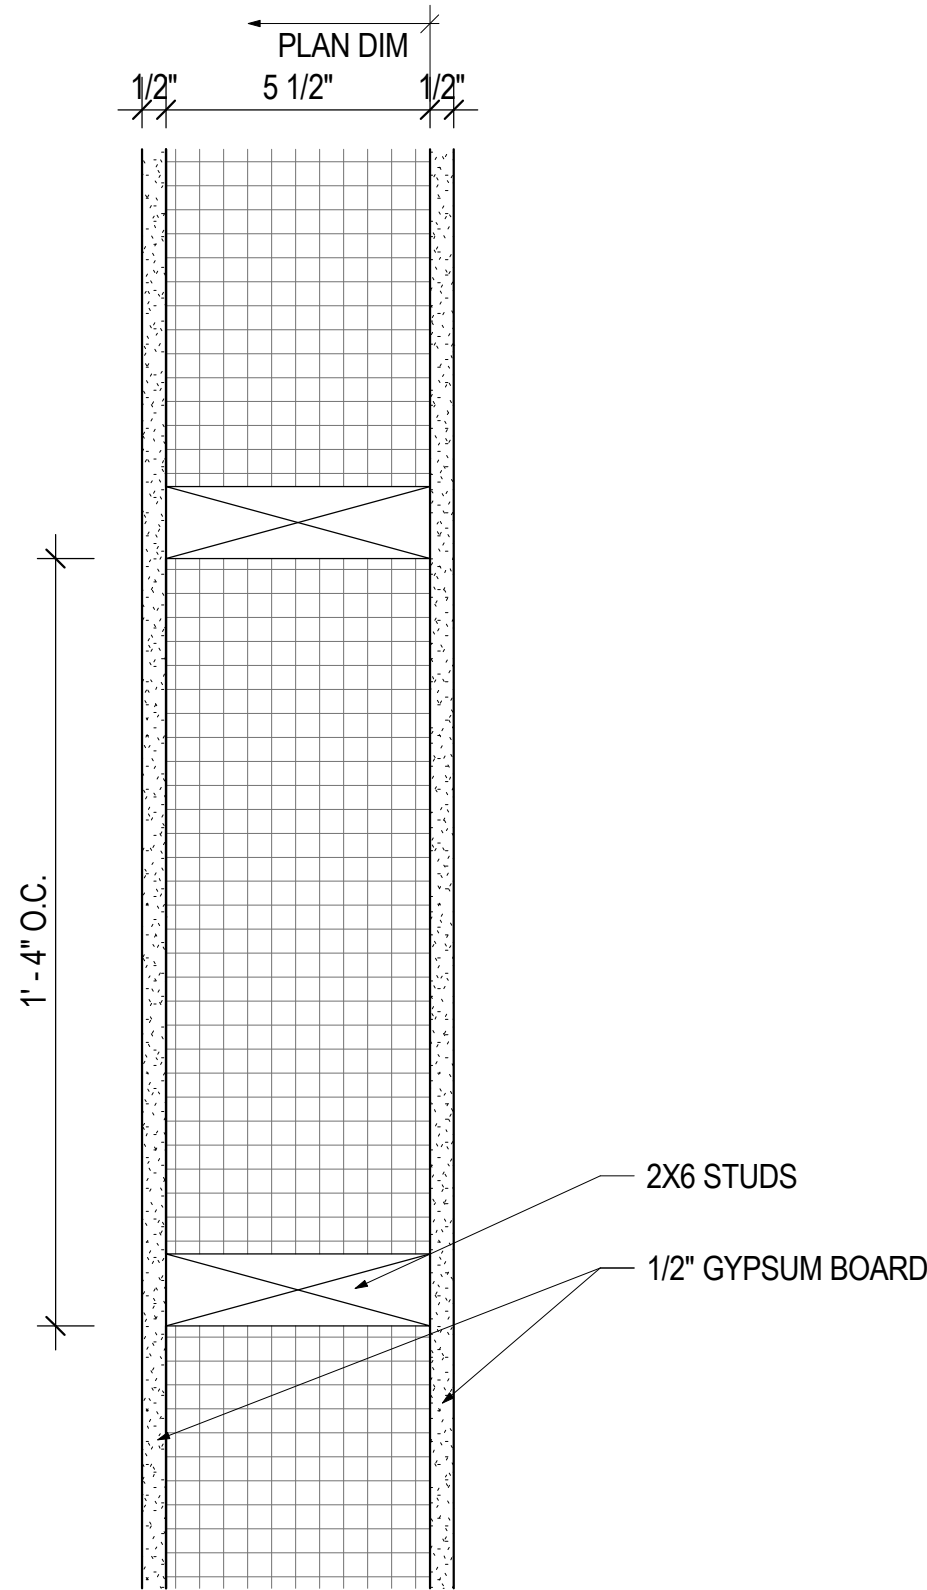


W-3 INTERIOR WALL, INSULATED
3" = 1'-0"

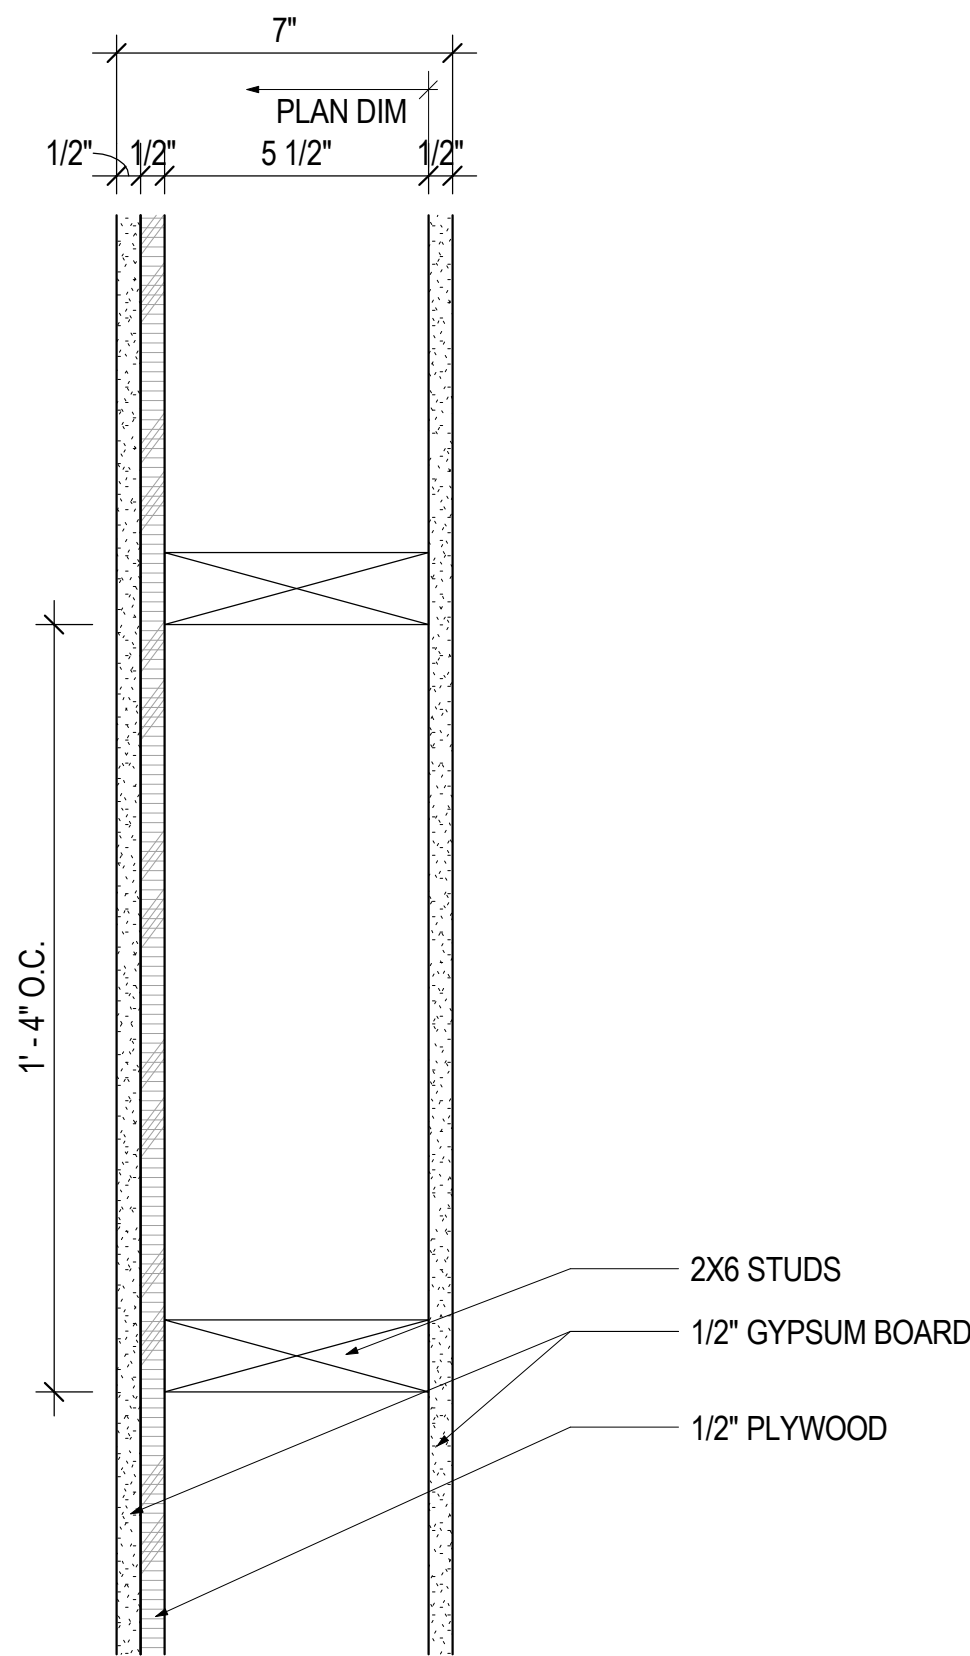


W-2 INTERIOR WALL, 2X6
3" = 1'-0"

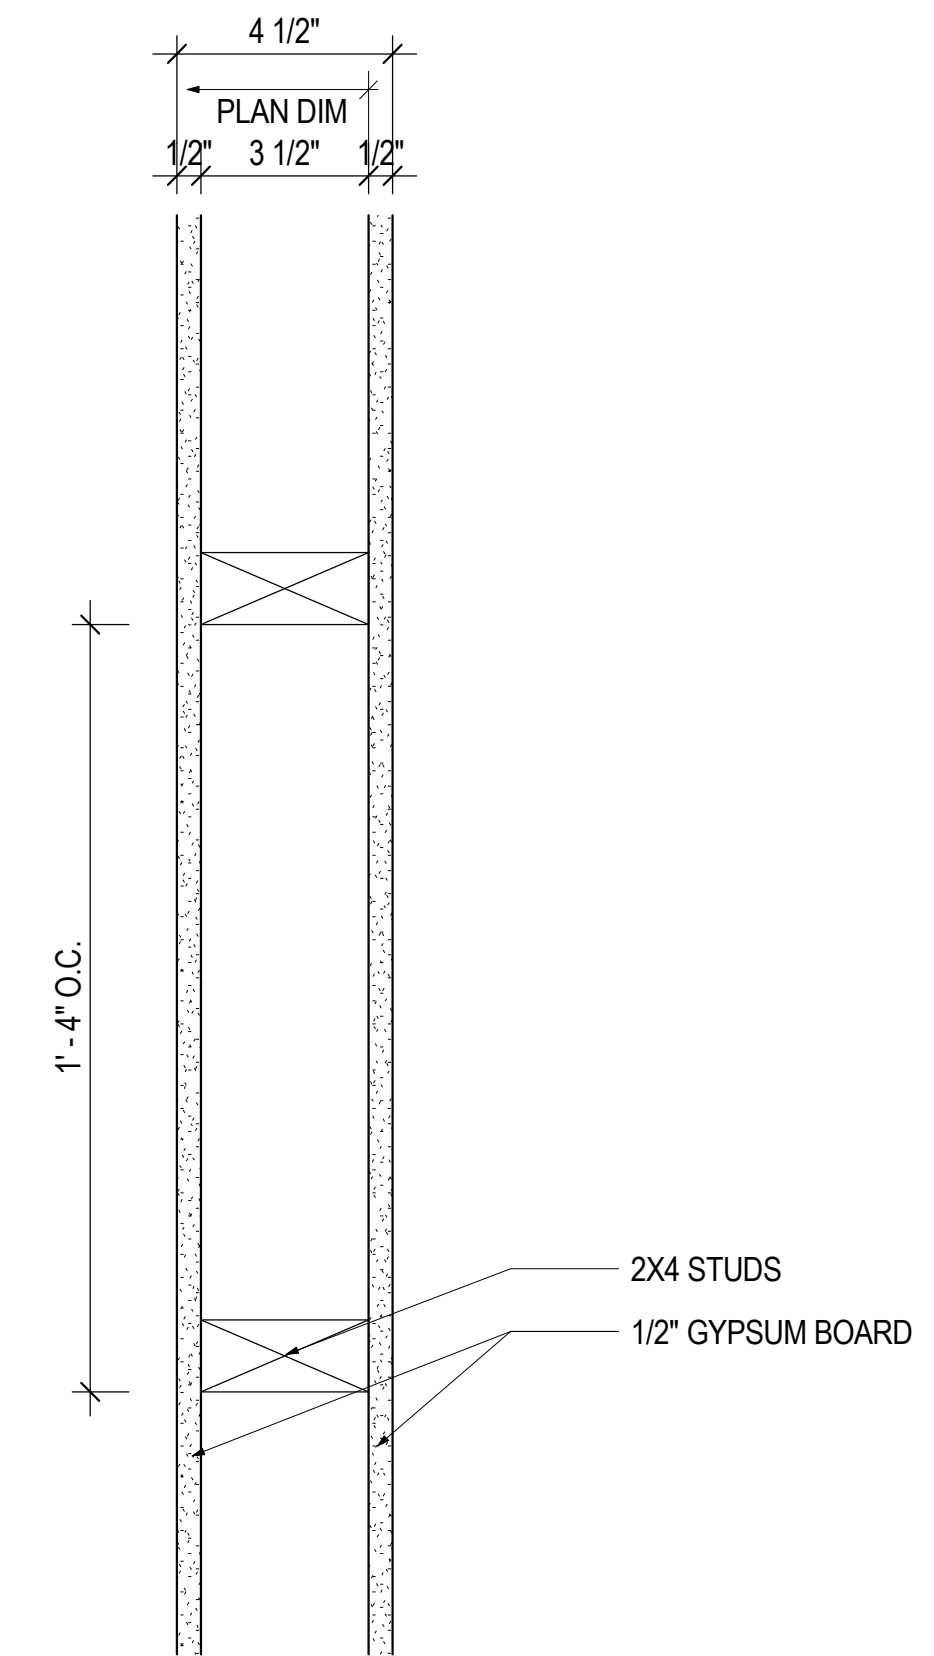


W-1 INTERIOR WALL, TYP
3" = 1'-0"

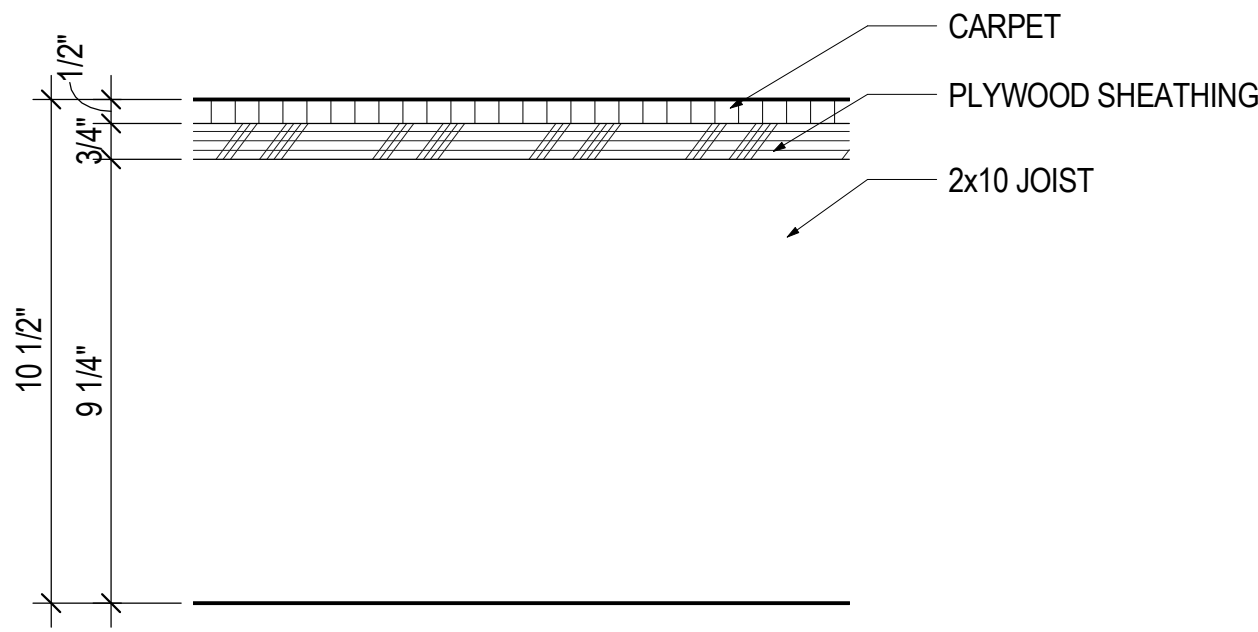


F-4 FLOOR ASSEMBLY, CARPET
3" = 1'-0"

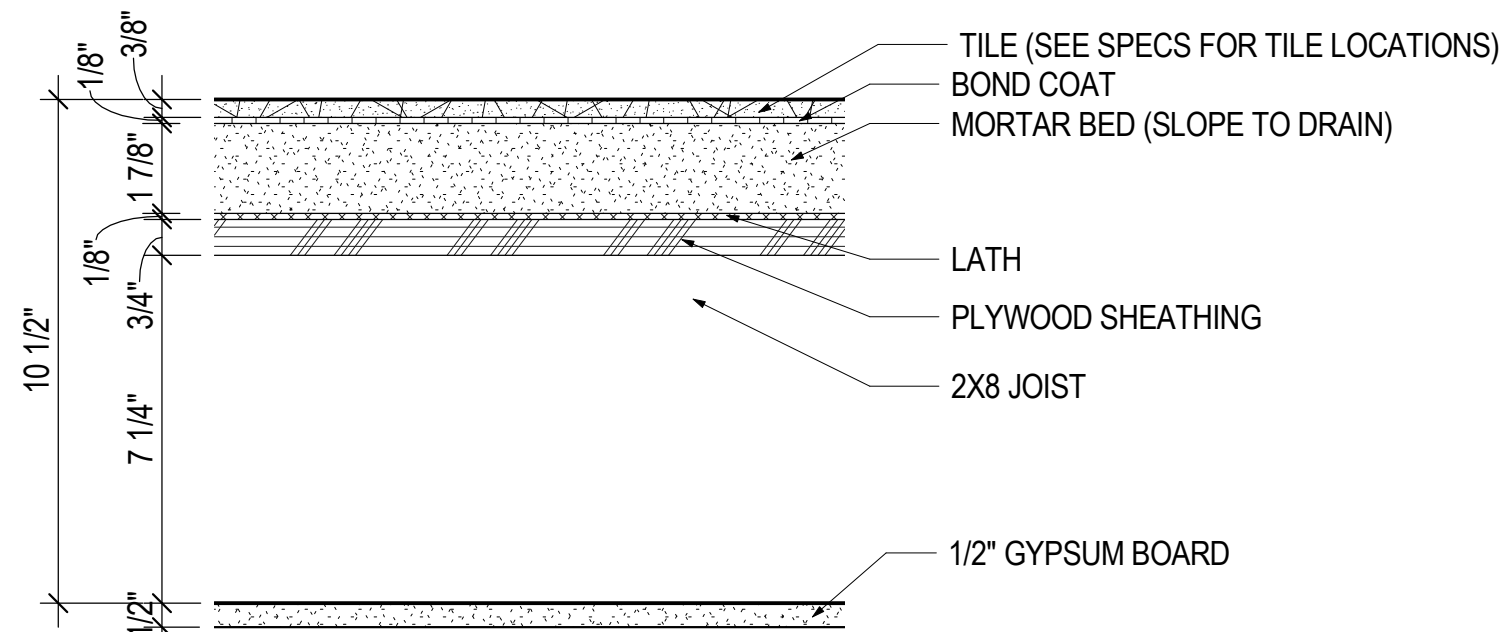


F-3 FLOOR ASSEMBLY, TILE AT SHOWER
3" = 1'-0"

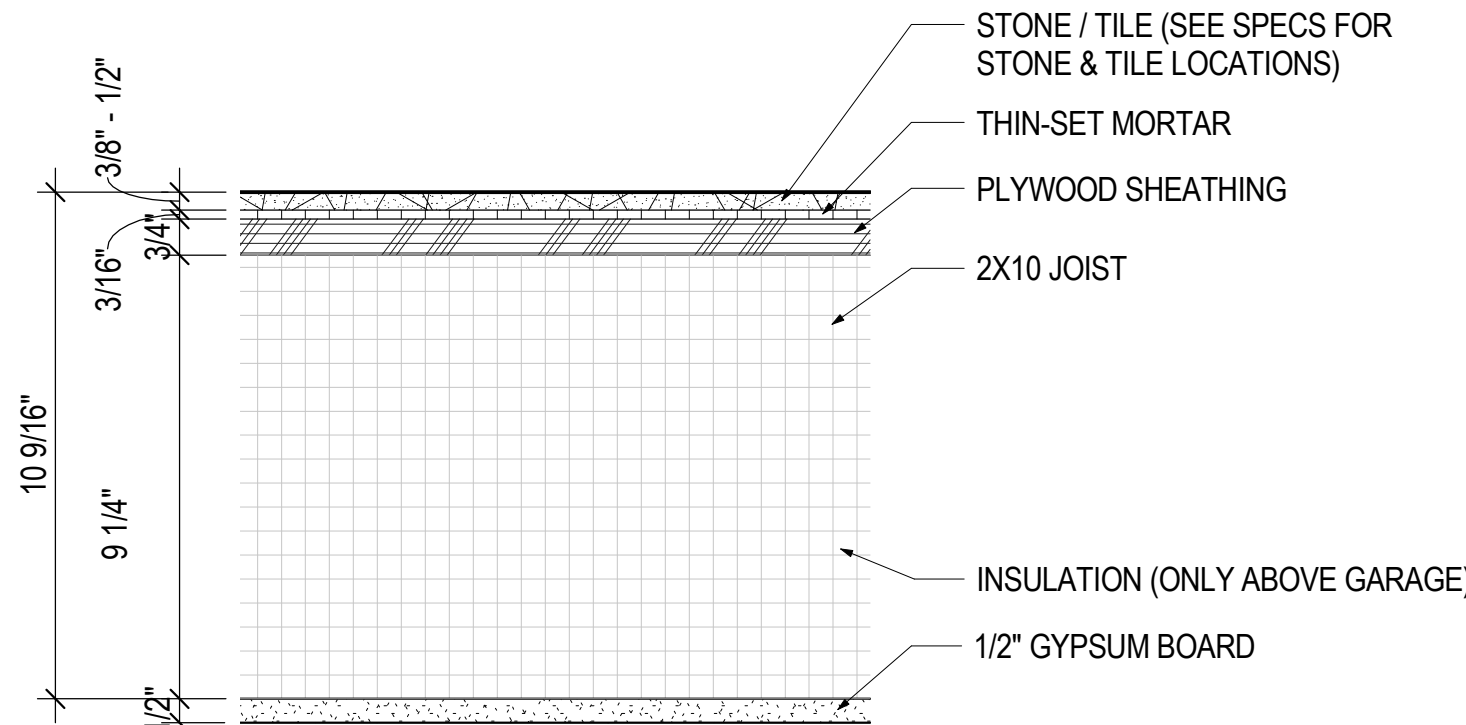


F-2 FLOOR ASSEMBLY, TILE THINSET
3" = 1'-0"

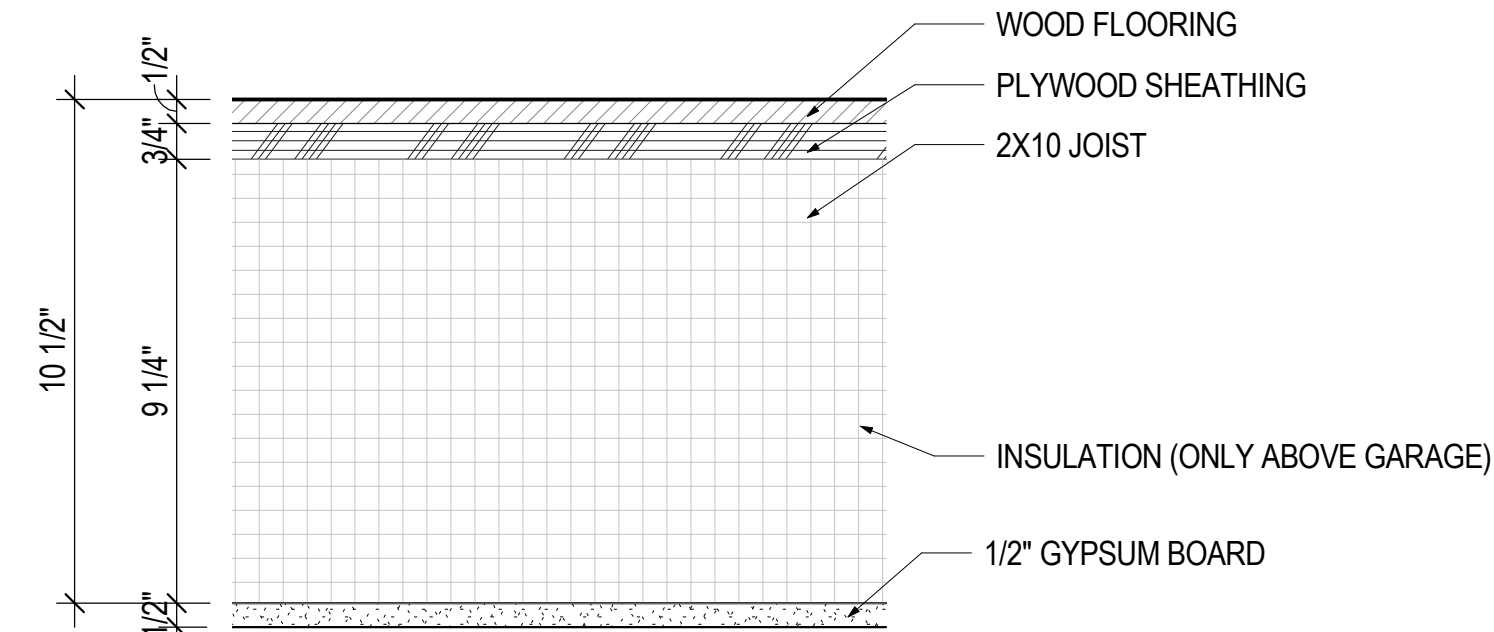


F-1 FLOOR ASSEMBLY, TYPICAL
3" = 1'-0"

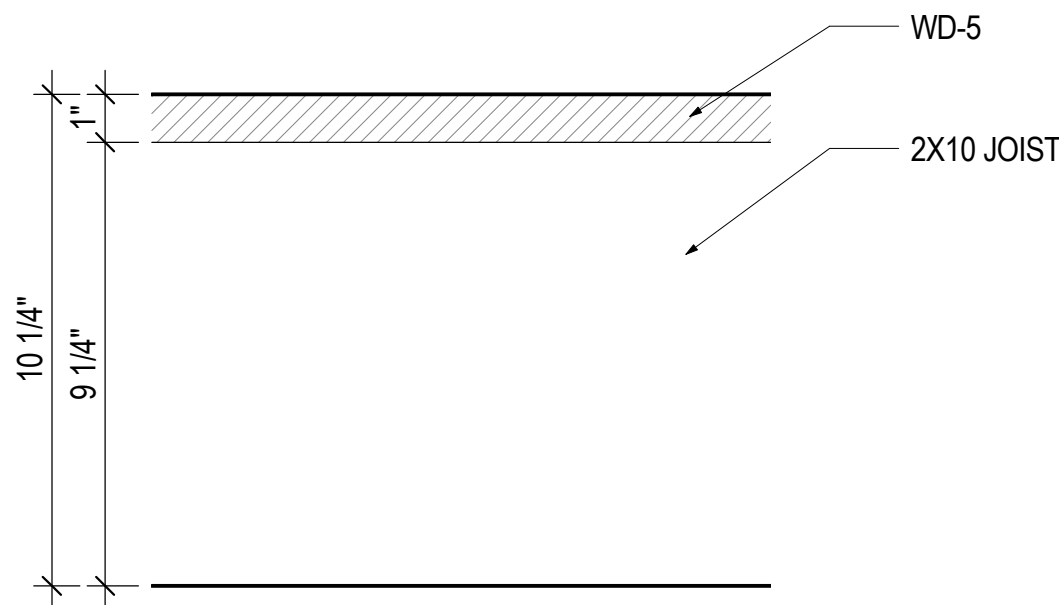


F-7 FLOOR ASSEMBLY, WOOD DECKING
3" = 1'-0"

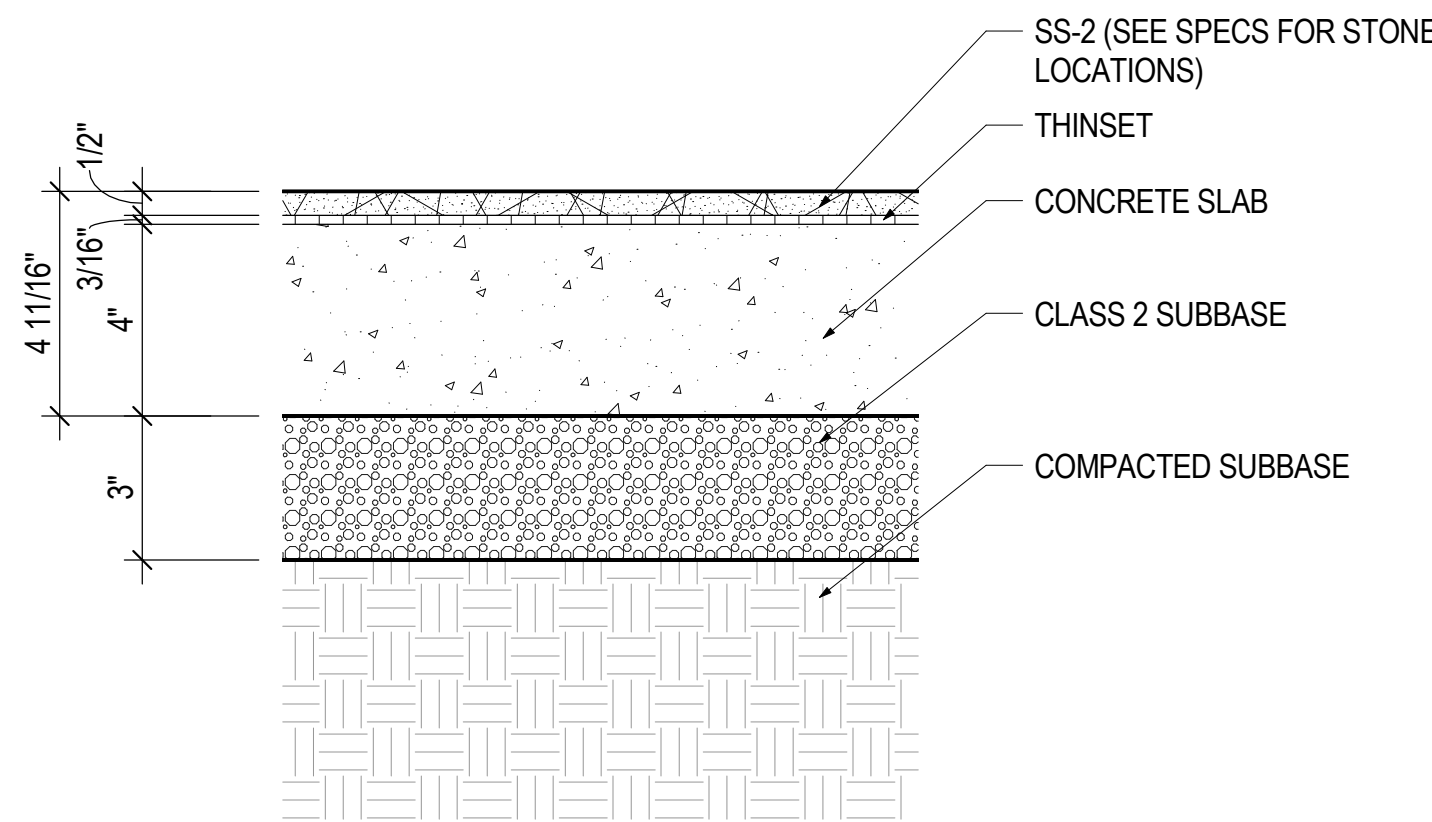


F-6 FLOOR ASSEMBLY, EXTERIOR STONE
3" = 1'-0"

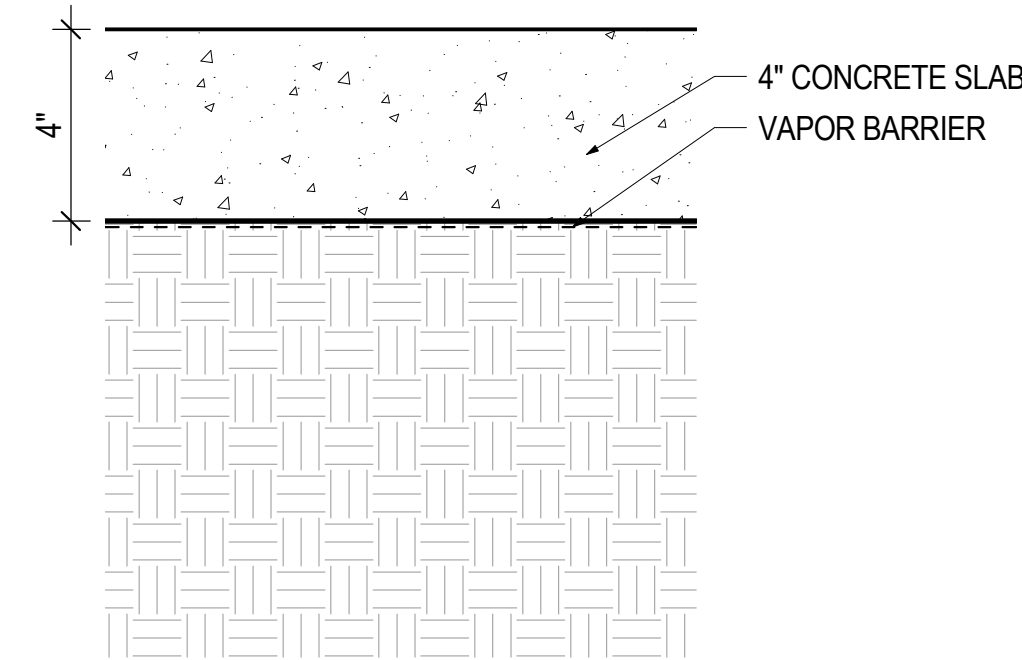

F-5 FLOOR ASSEMBLY, GARAGE
3" = 1'-0"

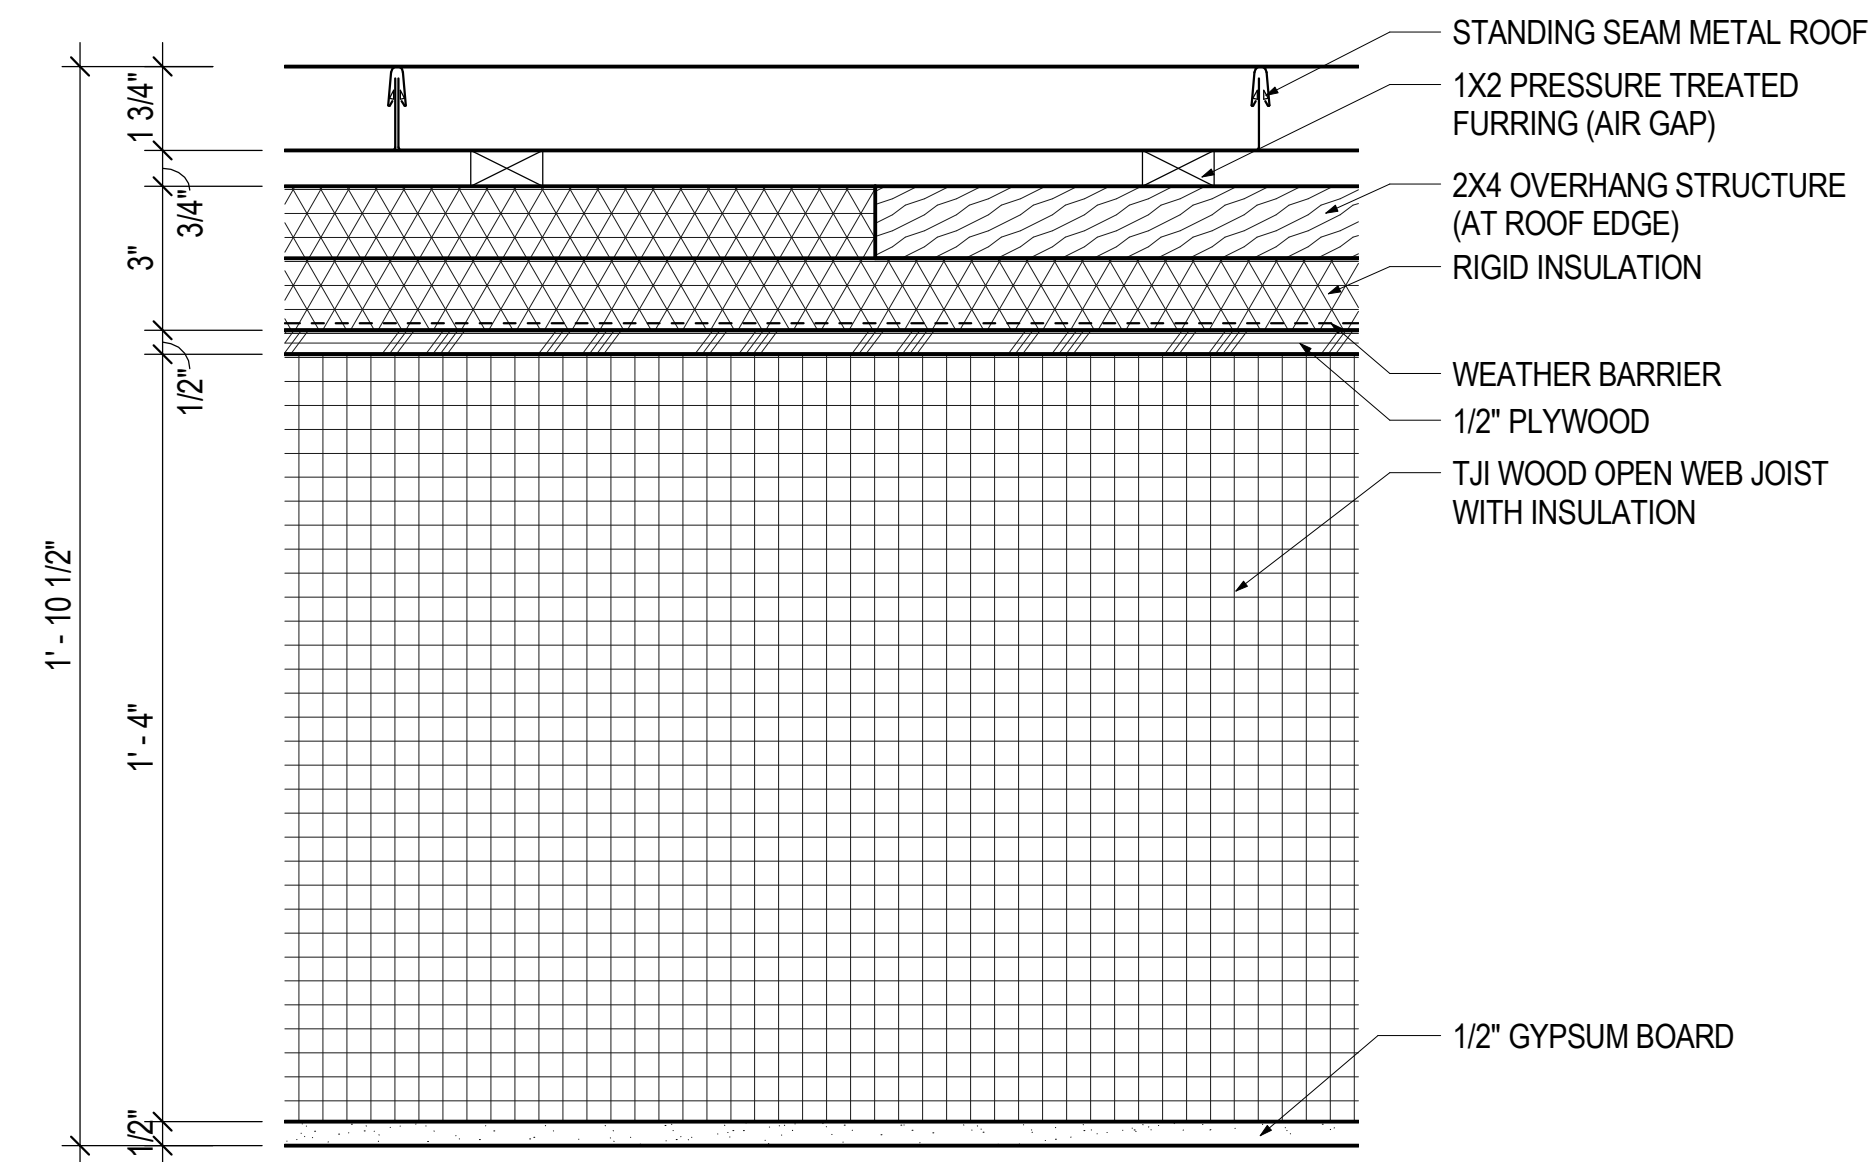

R-1 ROOF ASSEMBLY, TYPICAL
3" = 1'-0"

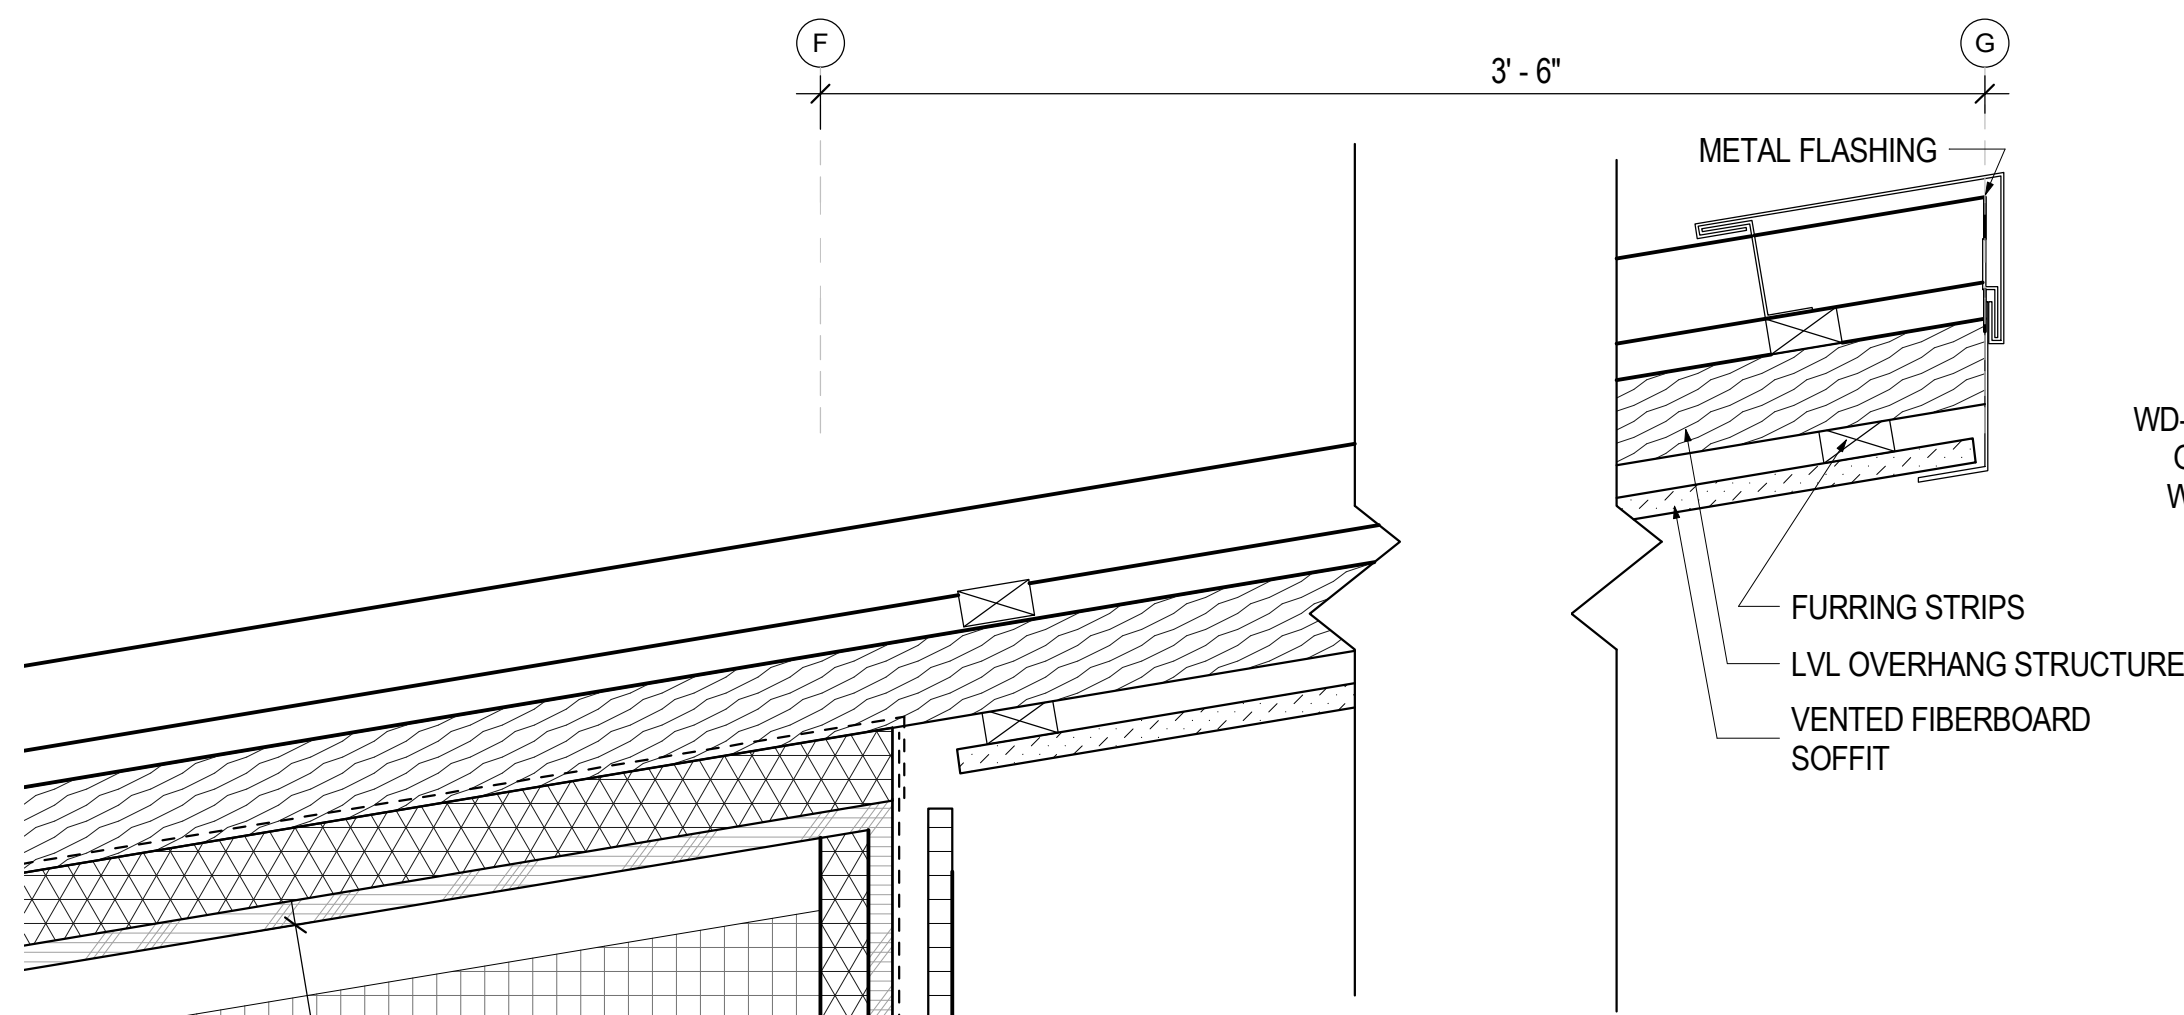

ROOF TRUSS OR I-JOIST WITH INSULATION
HEADER FRAMING (SEE STRUCTURAL)
T.O.F. (TOP OF FRAMING)

WOOD VENEER WD-1
WEATHER BARRIER
INSECT SCREEN
METAL FLASHING
ACCOYA FRAME

7 ROOF, ENTRY HALL
A4.10 3" = 1'-0"

FLASHING MEMBRANE
ACCOYA FRAME
INSECT SCREEN

8 SILL, ENTRY HALL WINDOW, TYP
A4.10 3" = 1'-0"

WD-4
WD-1 TRIM TYP AT GYP BOARD TO WOOD CORNER
GYP BOARD
ACCOYA FRAME

5 CORNER, FIBERBOARD
A4.10 3" = 1'-0"

WD-4
WD-1 WOOD VENEER
1X2 FURRING STRIP
WOOD BLOCKING AS NEEDED
1/2" PLYWOOD SHEATHING
1/4" MIRROR PANEL FULL HEIGHT OF WINDOW CAVITY
2x10 STUD
FLASHING MEMBRANE
ACCOYA FRAME

4 JAMB, ENTRY WALL WINDOW, TYP
A4.10 3" = 1'-0"

WD-4 DOOR FRAME
WD-1 WOOD VENEER
1X2 FURRING STRIP
WOOD BLOCKING AS NEEDED
1/2" PLYWOOD SHEATHING
1/4" MIRROR PANEL FULL HEIGHT OF WINDOW CAVITY
ACCOYA TRIM, ALIGN WITH WINDOW FRAME

1 JAMB, ENTRY DOOR
A4.10 3" = 1'-0"

INSECT SCREEN
METAL FLASHING
ACCOYA TRIM, ALIGN WITH WINDOW FRAME
DOOR FRAME
ALIGN



2 HEAD, ENTRY DOOR
A4.10 3" = 1'-0"


WOOD VENEER WD-1
INSECT SCREEN
METAL FLASHING
STONE DECK
CMU EXTENSION FOR DECK FOUNDATION
LEVEL 1 508'-0"
INSULATION
VAPOR BARRIER
RIGID INSULATION
7 1/4"
1 1/2"
9 5/8"

6 BASE, ENTRY HALL
A4.10 3" = 1'-0"


DOOR SILL
METAL FLASHING
LEVEL 1 508'-0"

3 BASE, ENTRY DOOR
A4.10 3" = 1'-0"

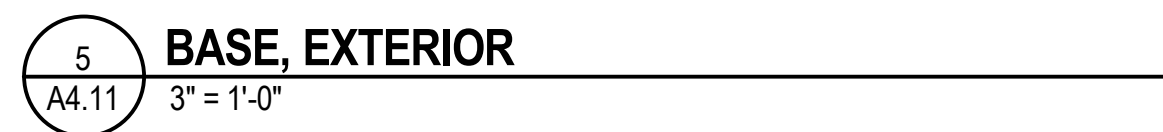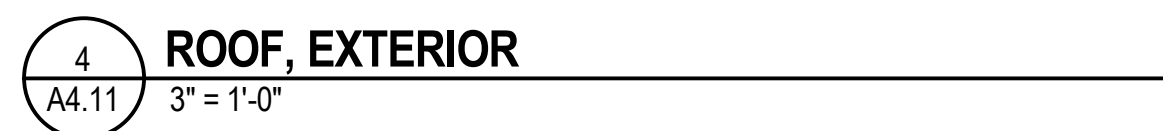


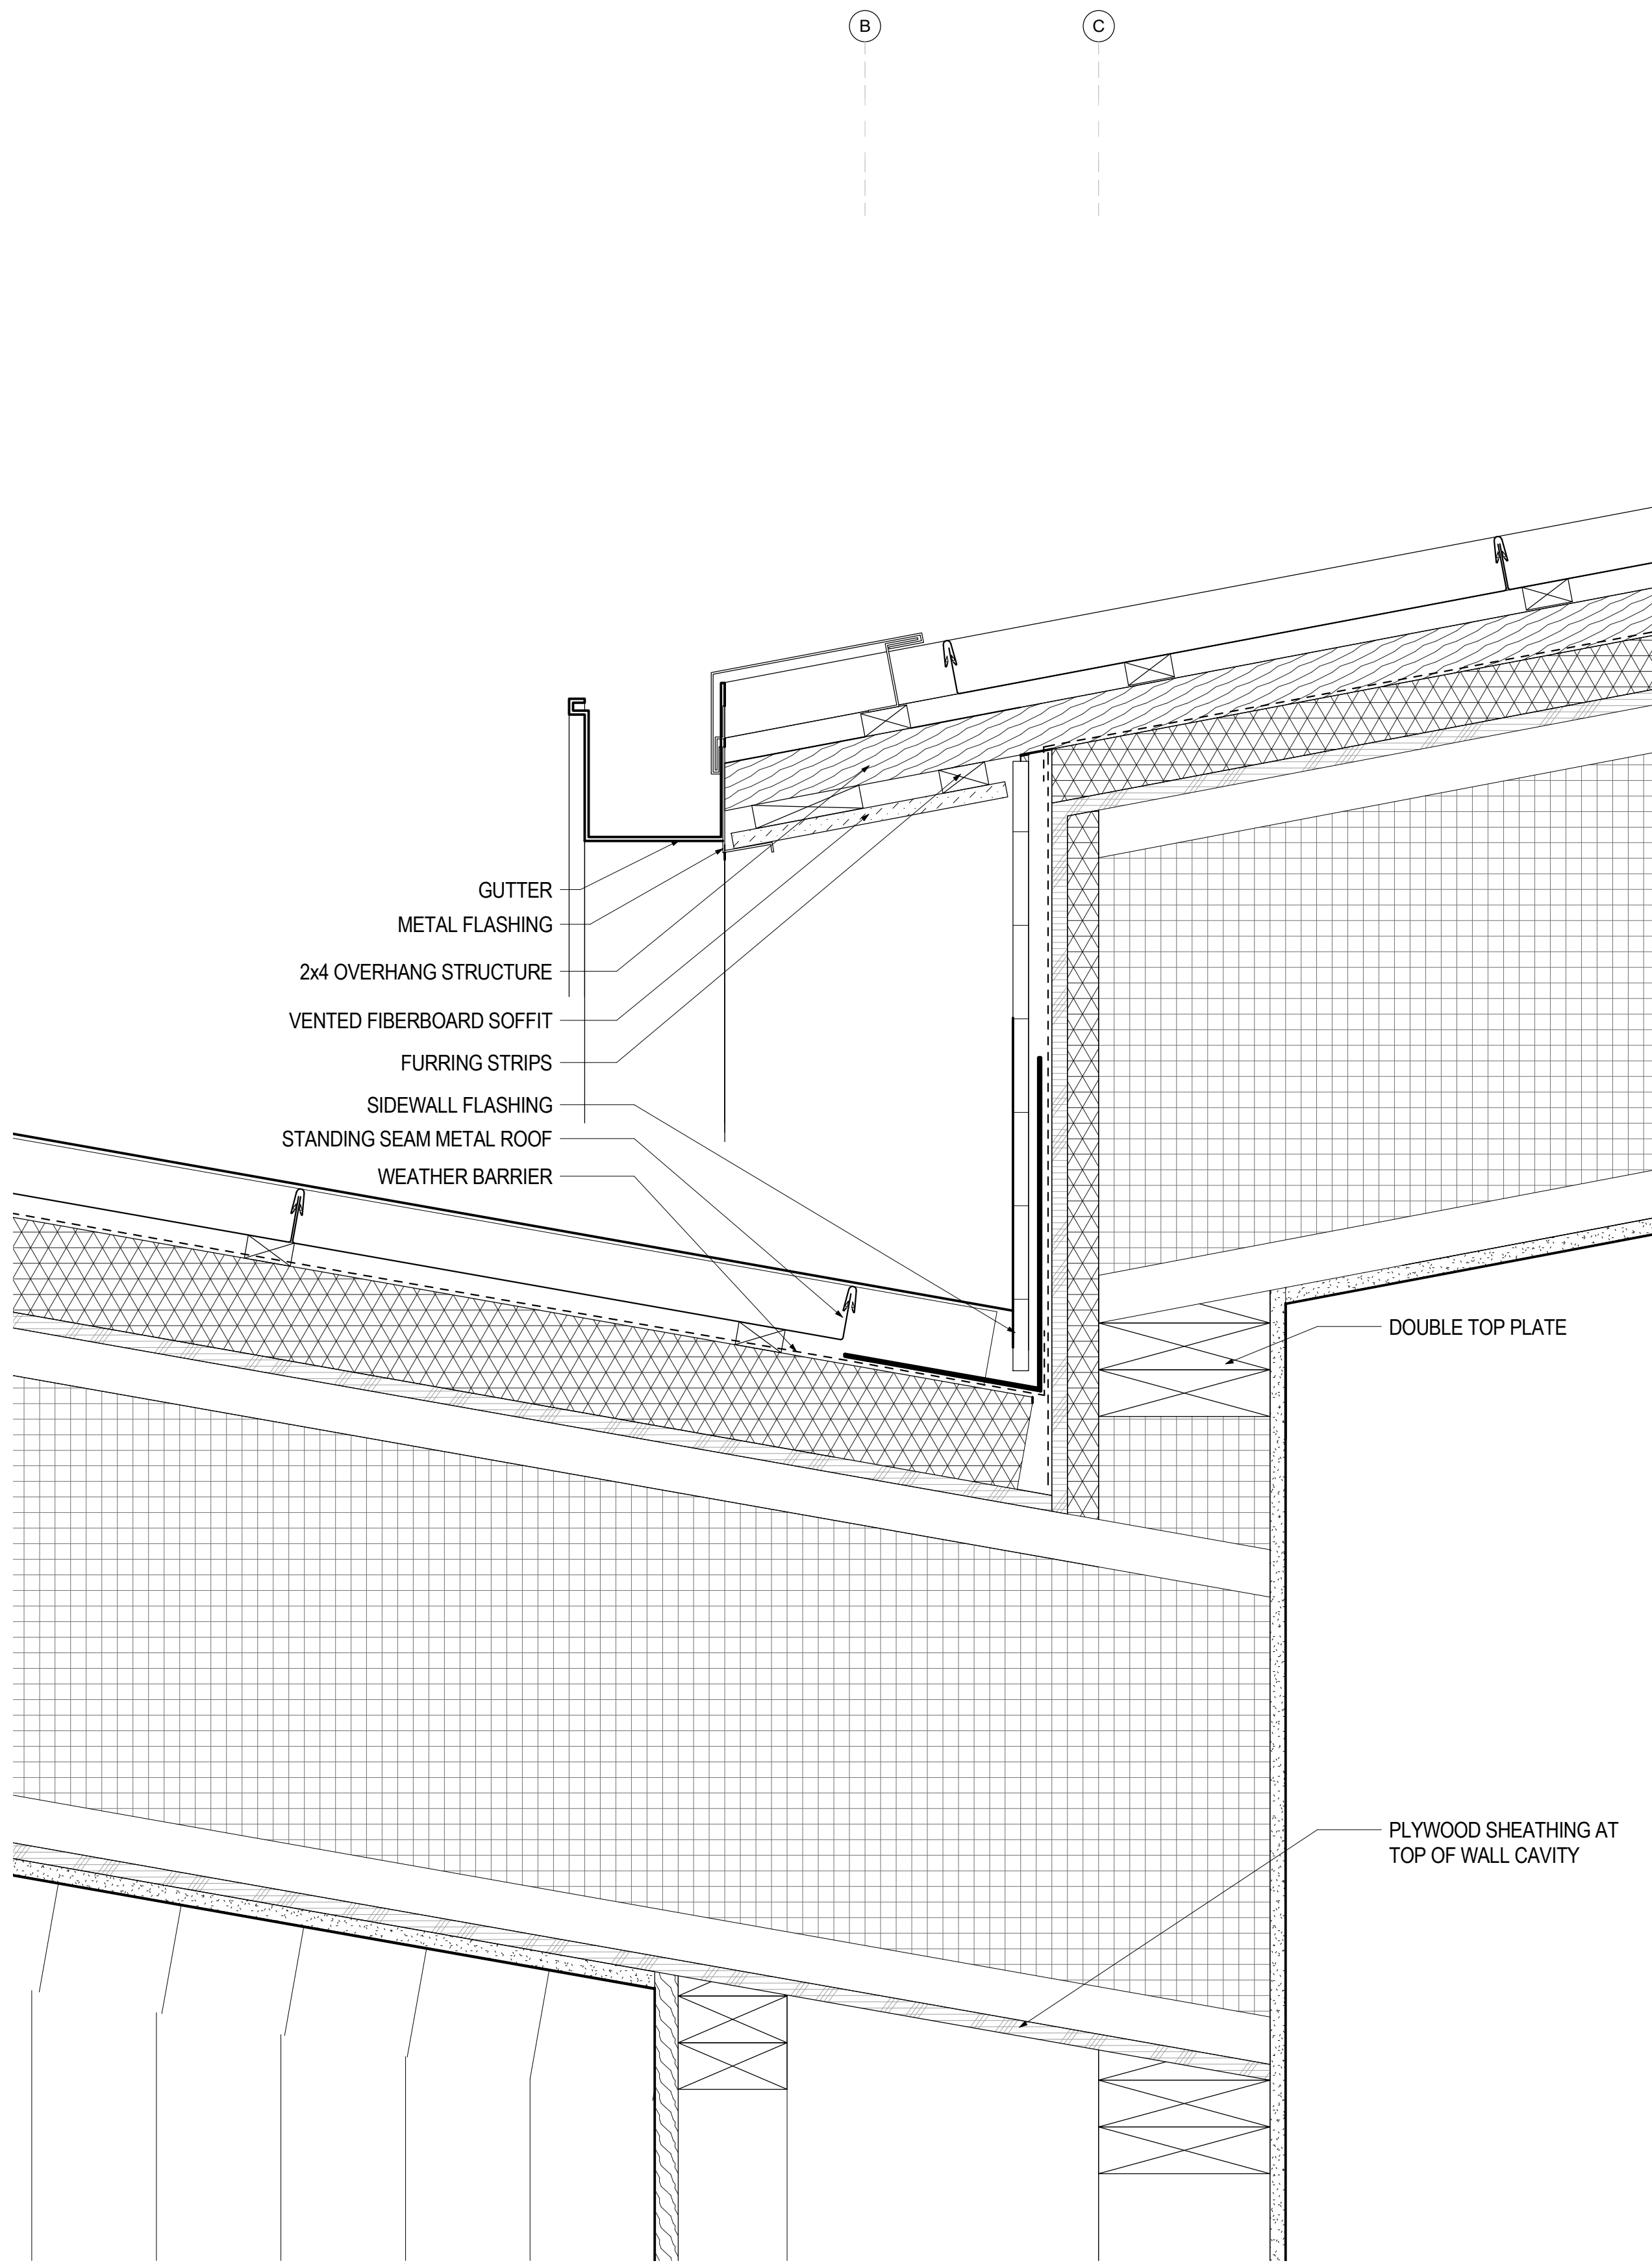


6 SECTION, ROOF INTERSECTION
A4.12 3" = 1'-0"

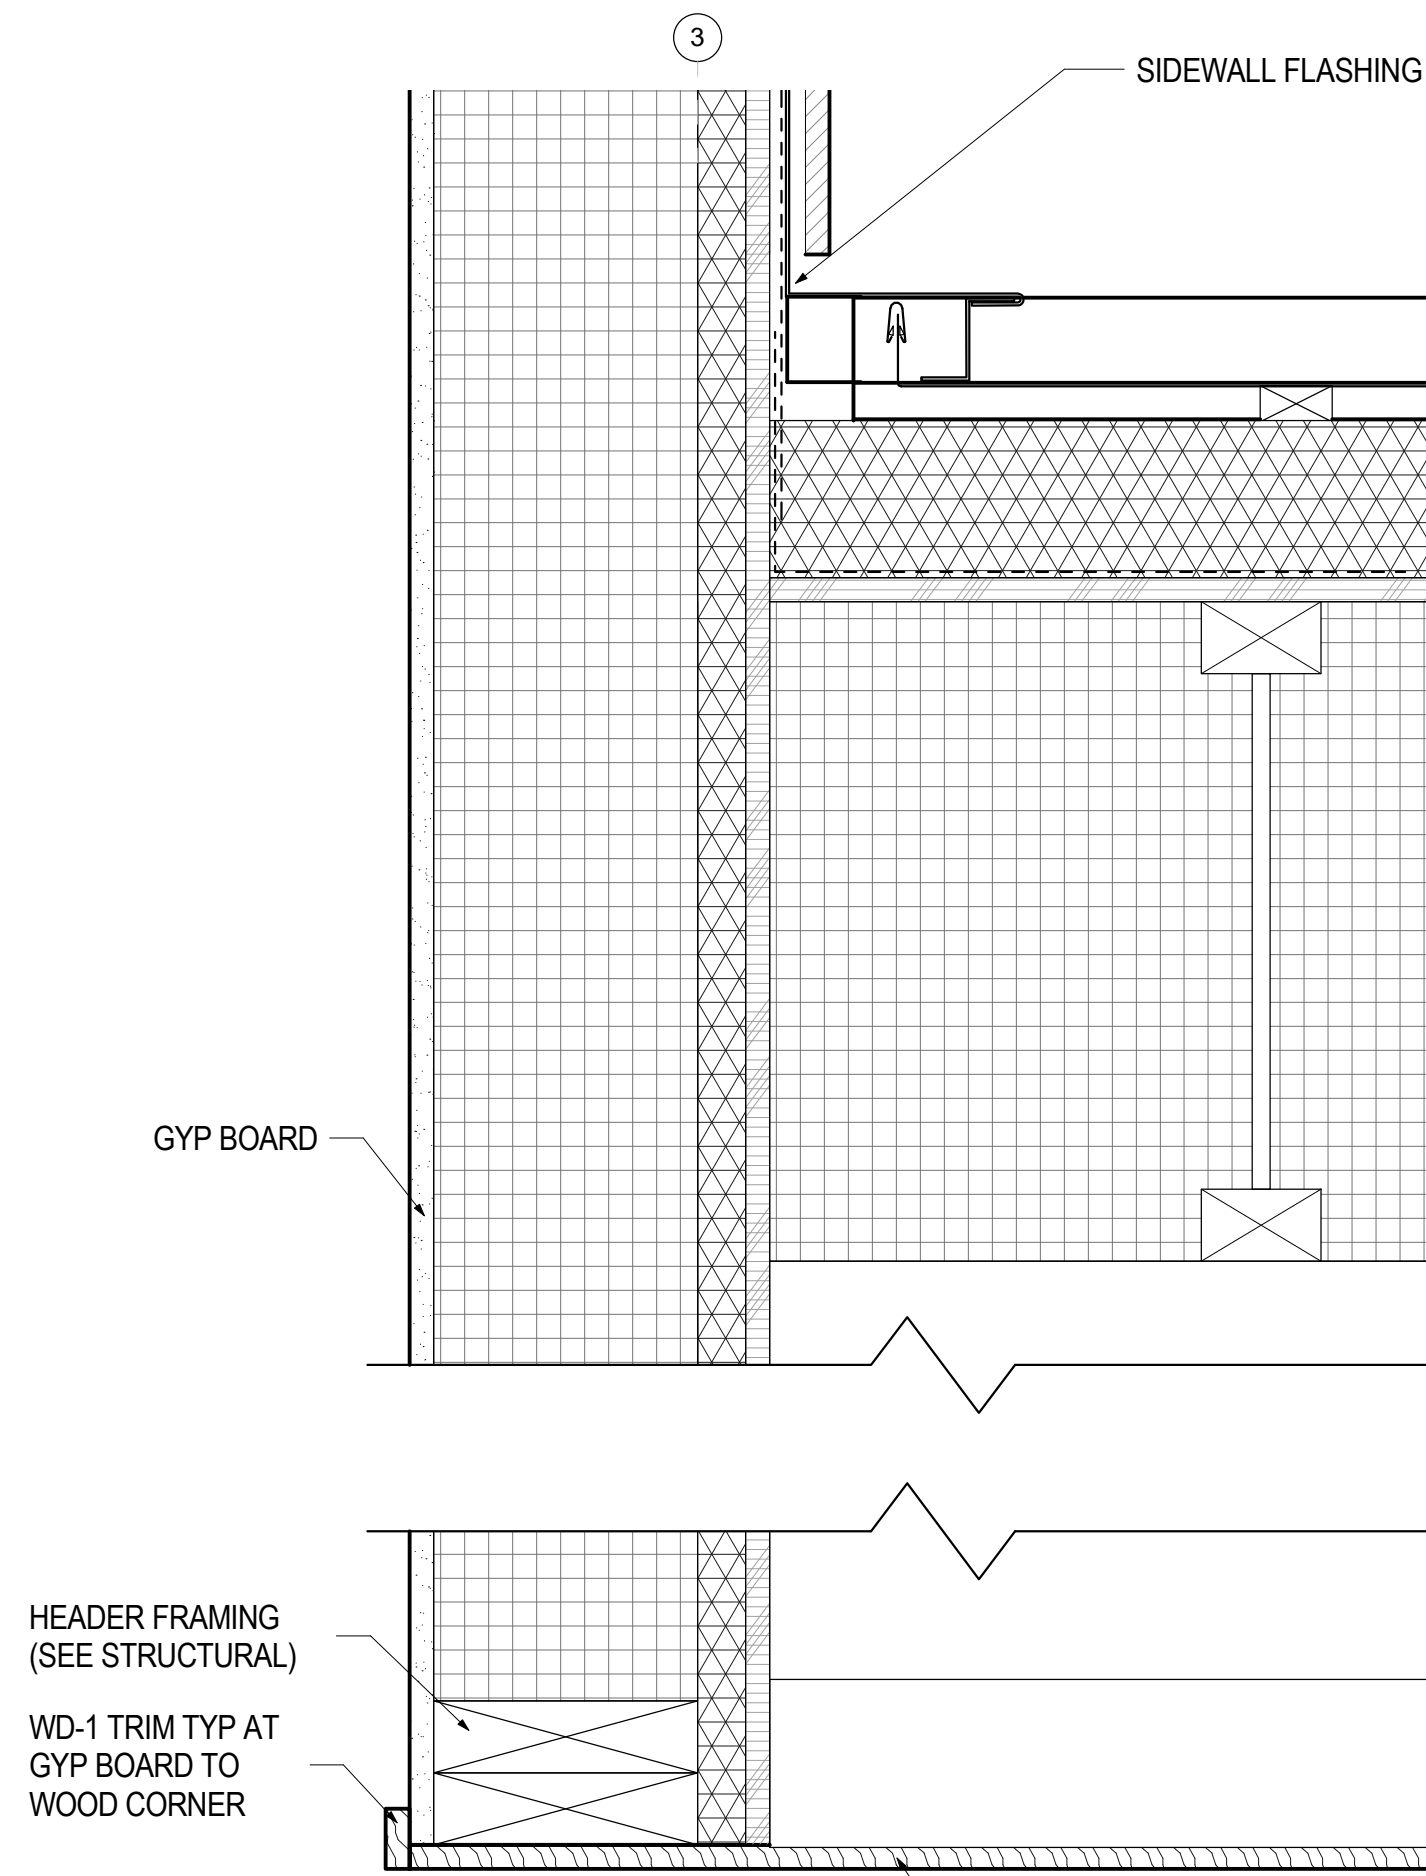


4 SECTION, ENTRY HALL ROOF
A4.12 3" = 1'-0"

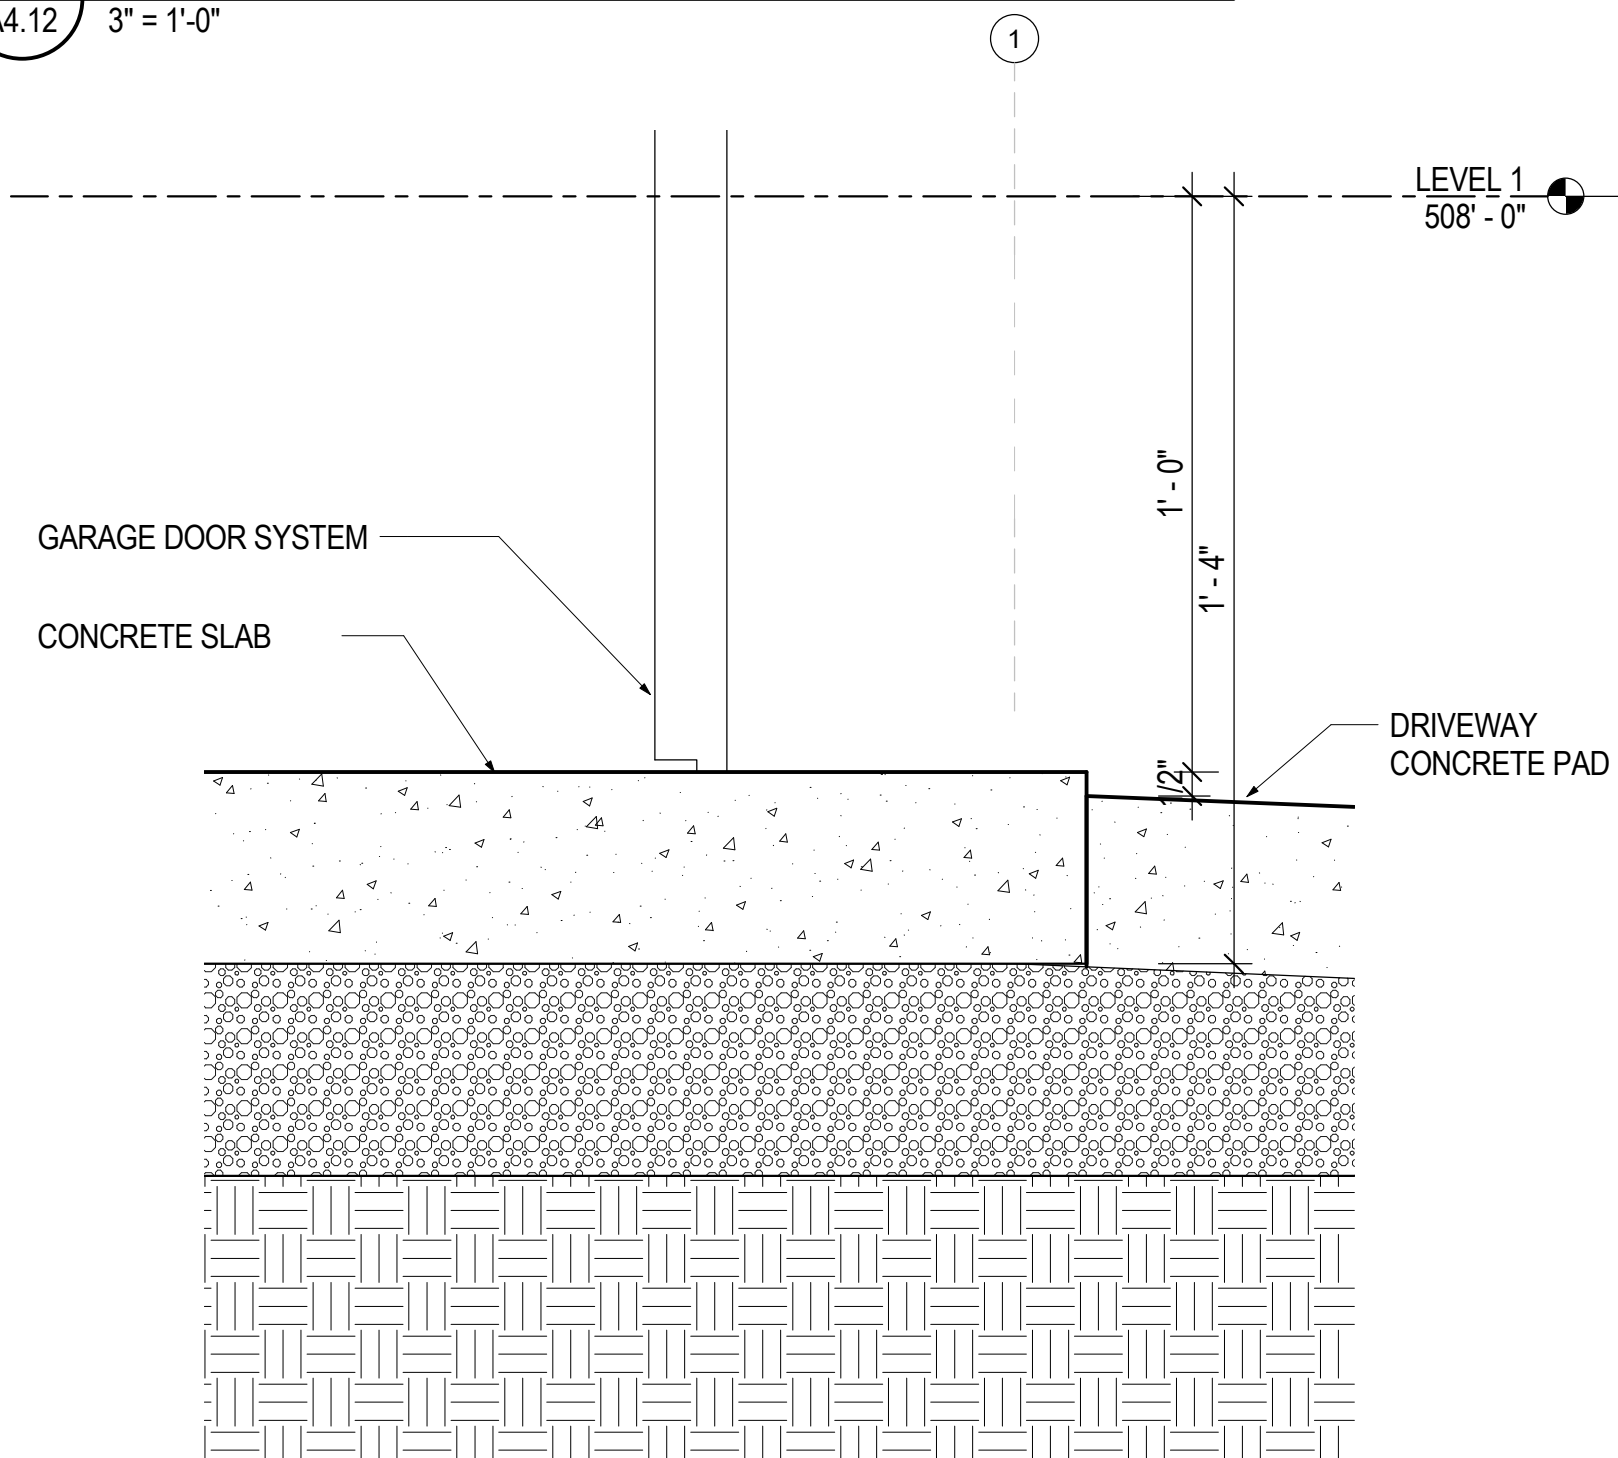


8 BASE, GARAGE DOOR
A4.12 3" = 1'-0"

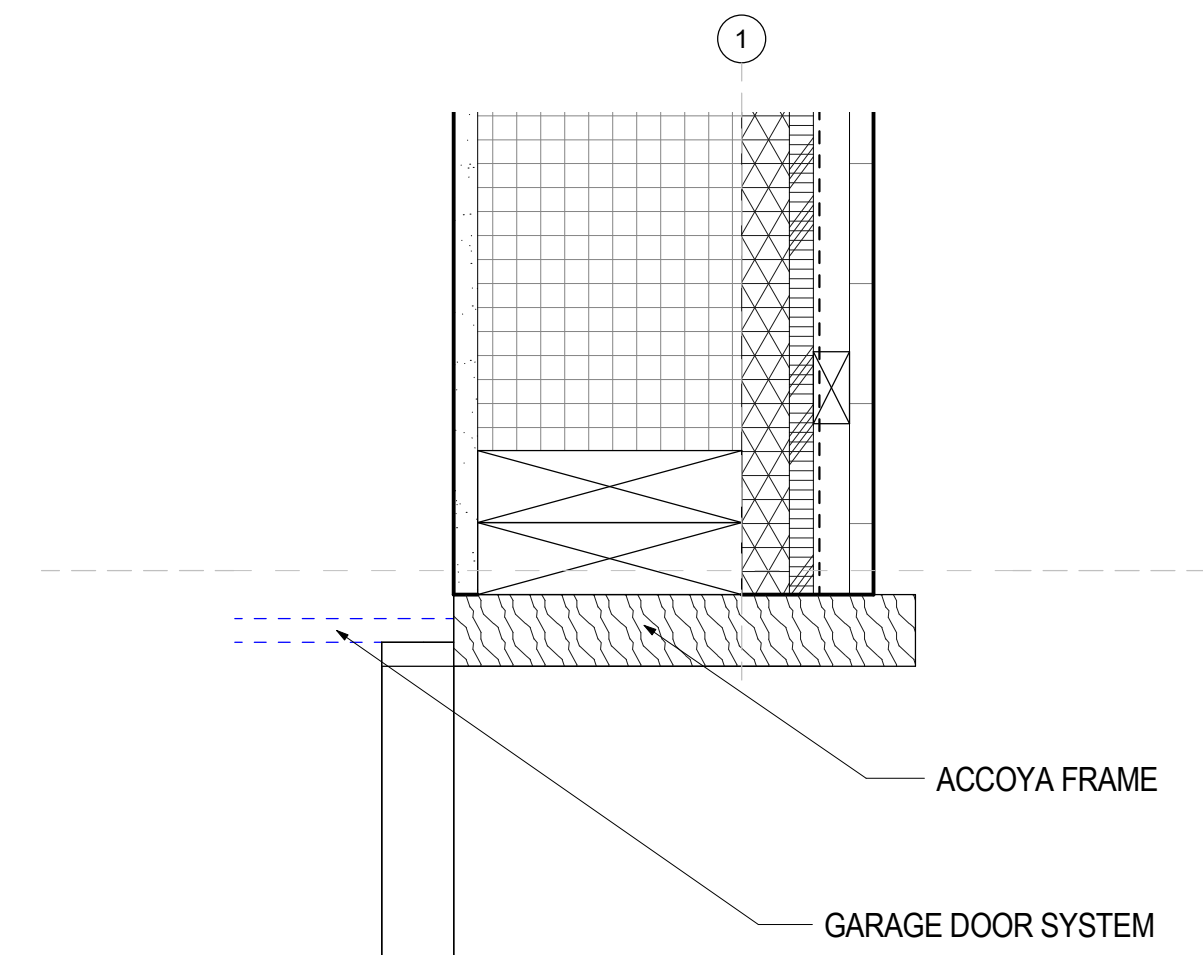


2 JAMB, GARAGE DOOR
A4.12 3" = 1'-0"

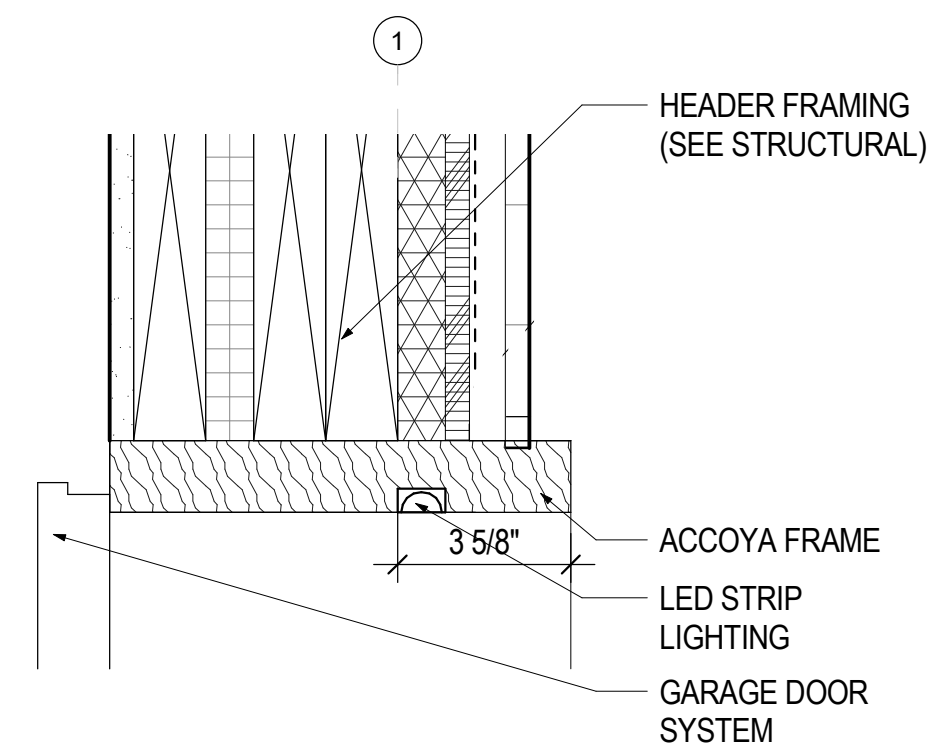


3 HEADER, GARAGE DOOR
A4.12 3" = 1'-0"

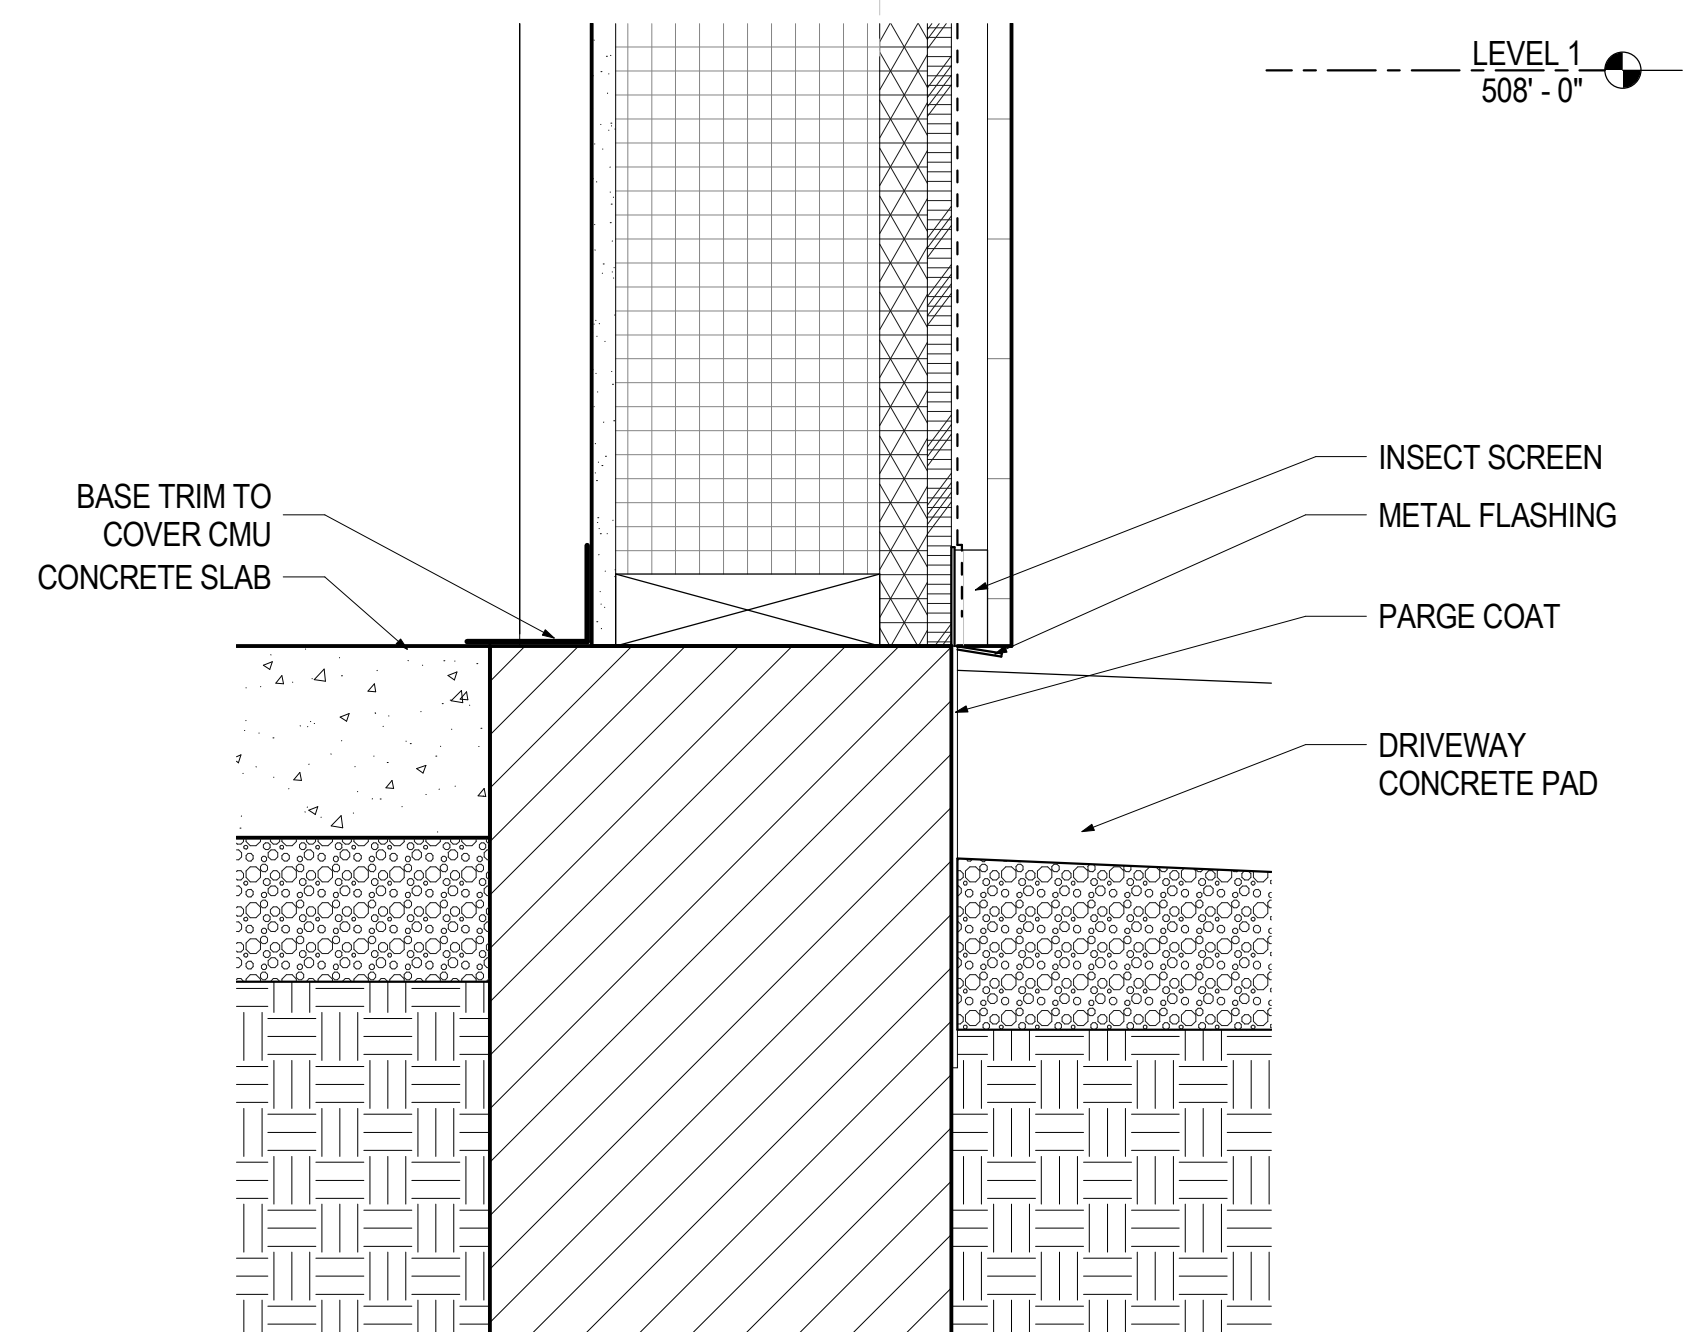


7 BASE, GARAGE
A4.12 3" = 1'-0"

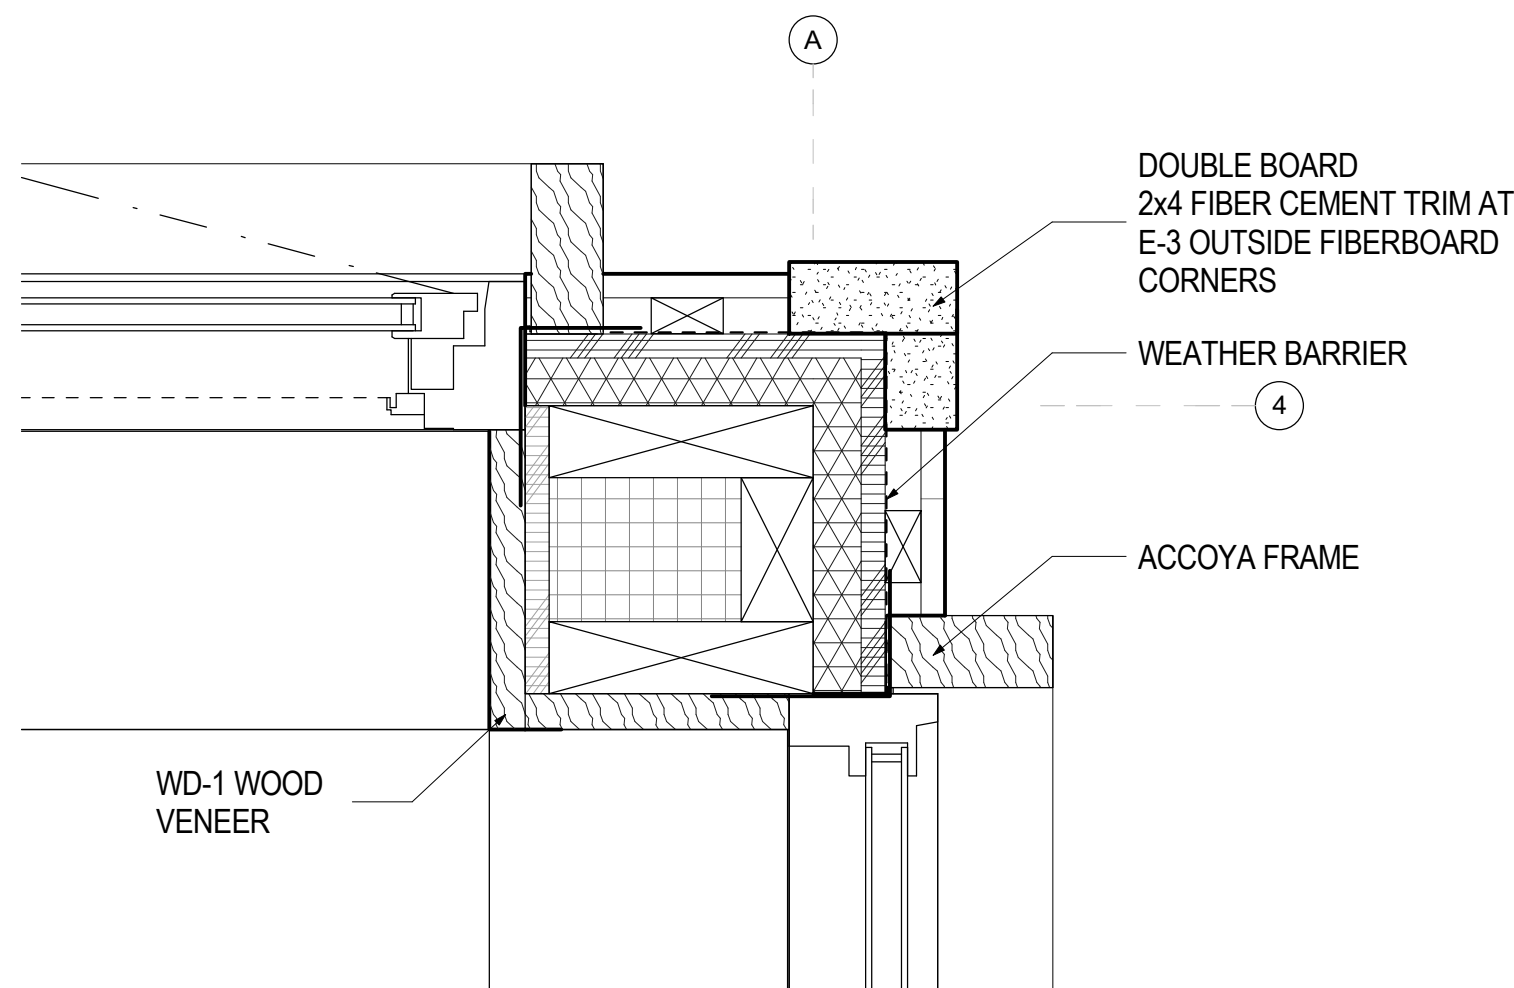


4 JAMB, BATHROOM WINDOW
A4.13 3" = 1'-0"

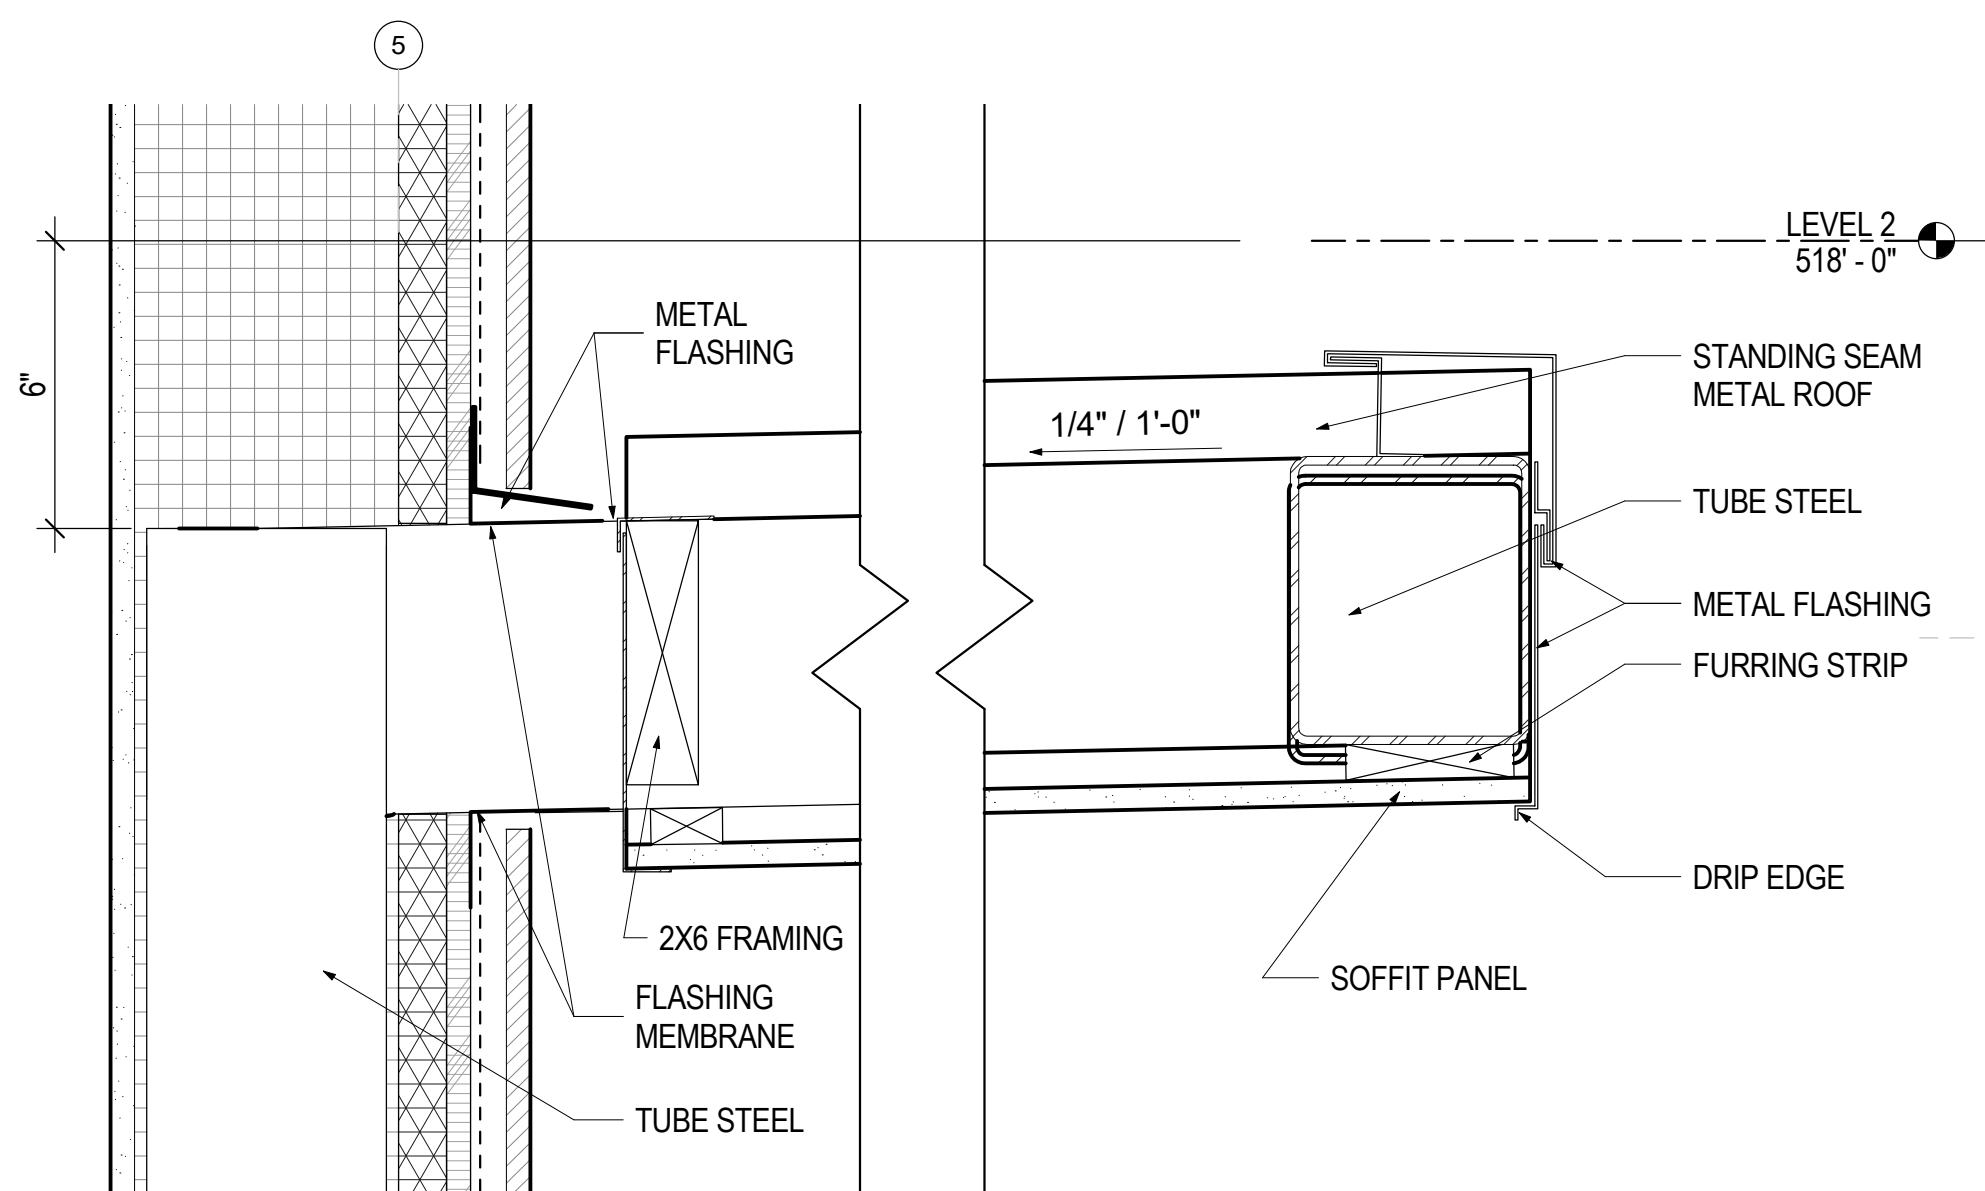


5 SECTION, PORCH OVERHANG
A4.13 3" = 1'-0"

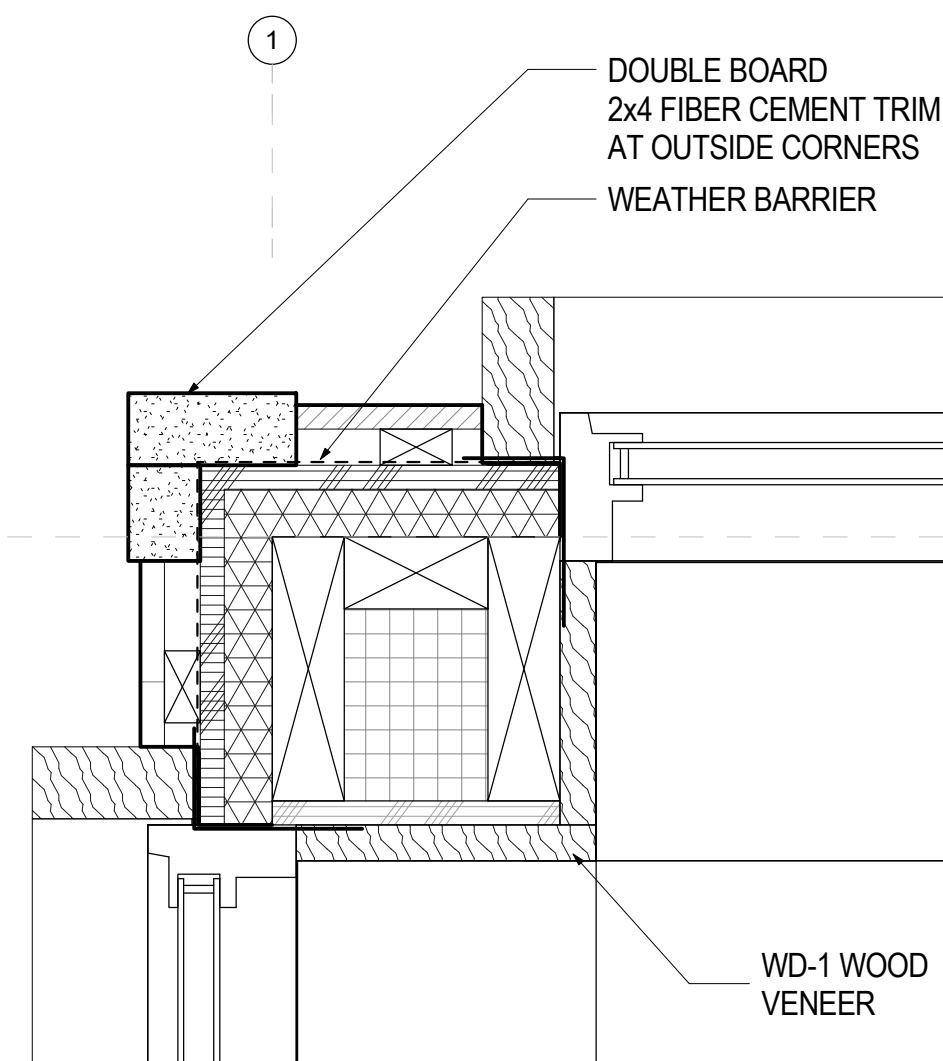


3 JAMB, CORNER WINDOW, OFFICE
A4.13 3" = 1'-0"

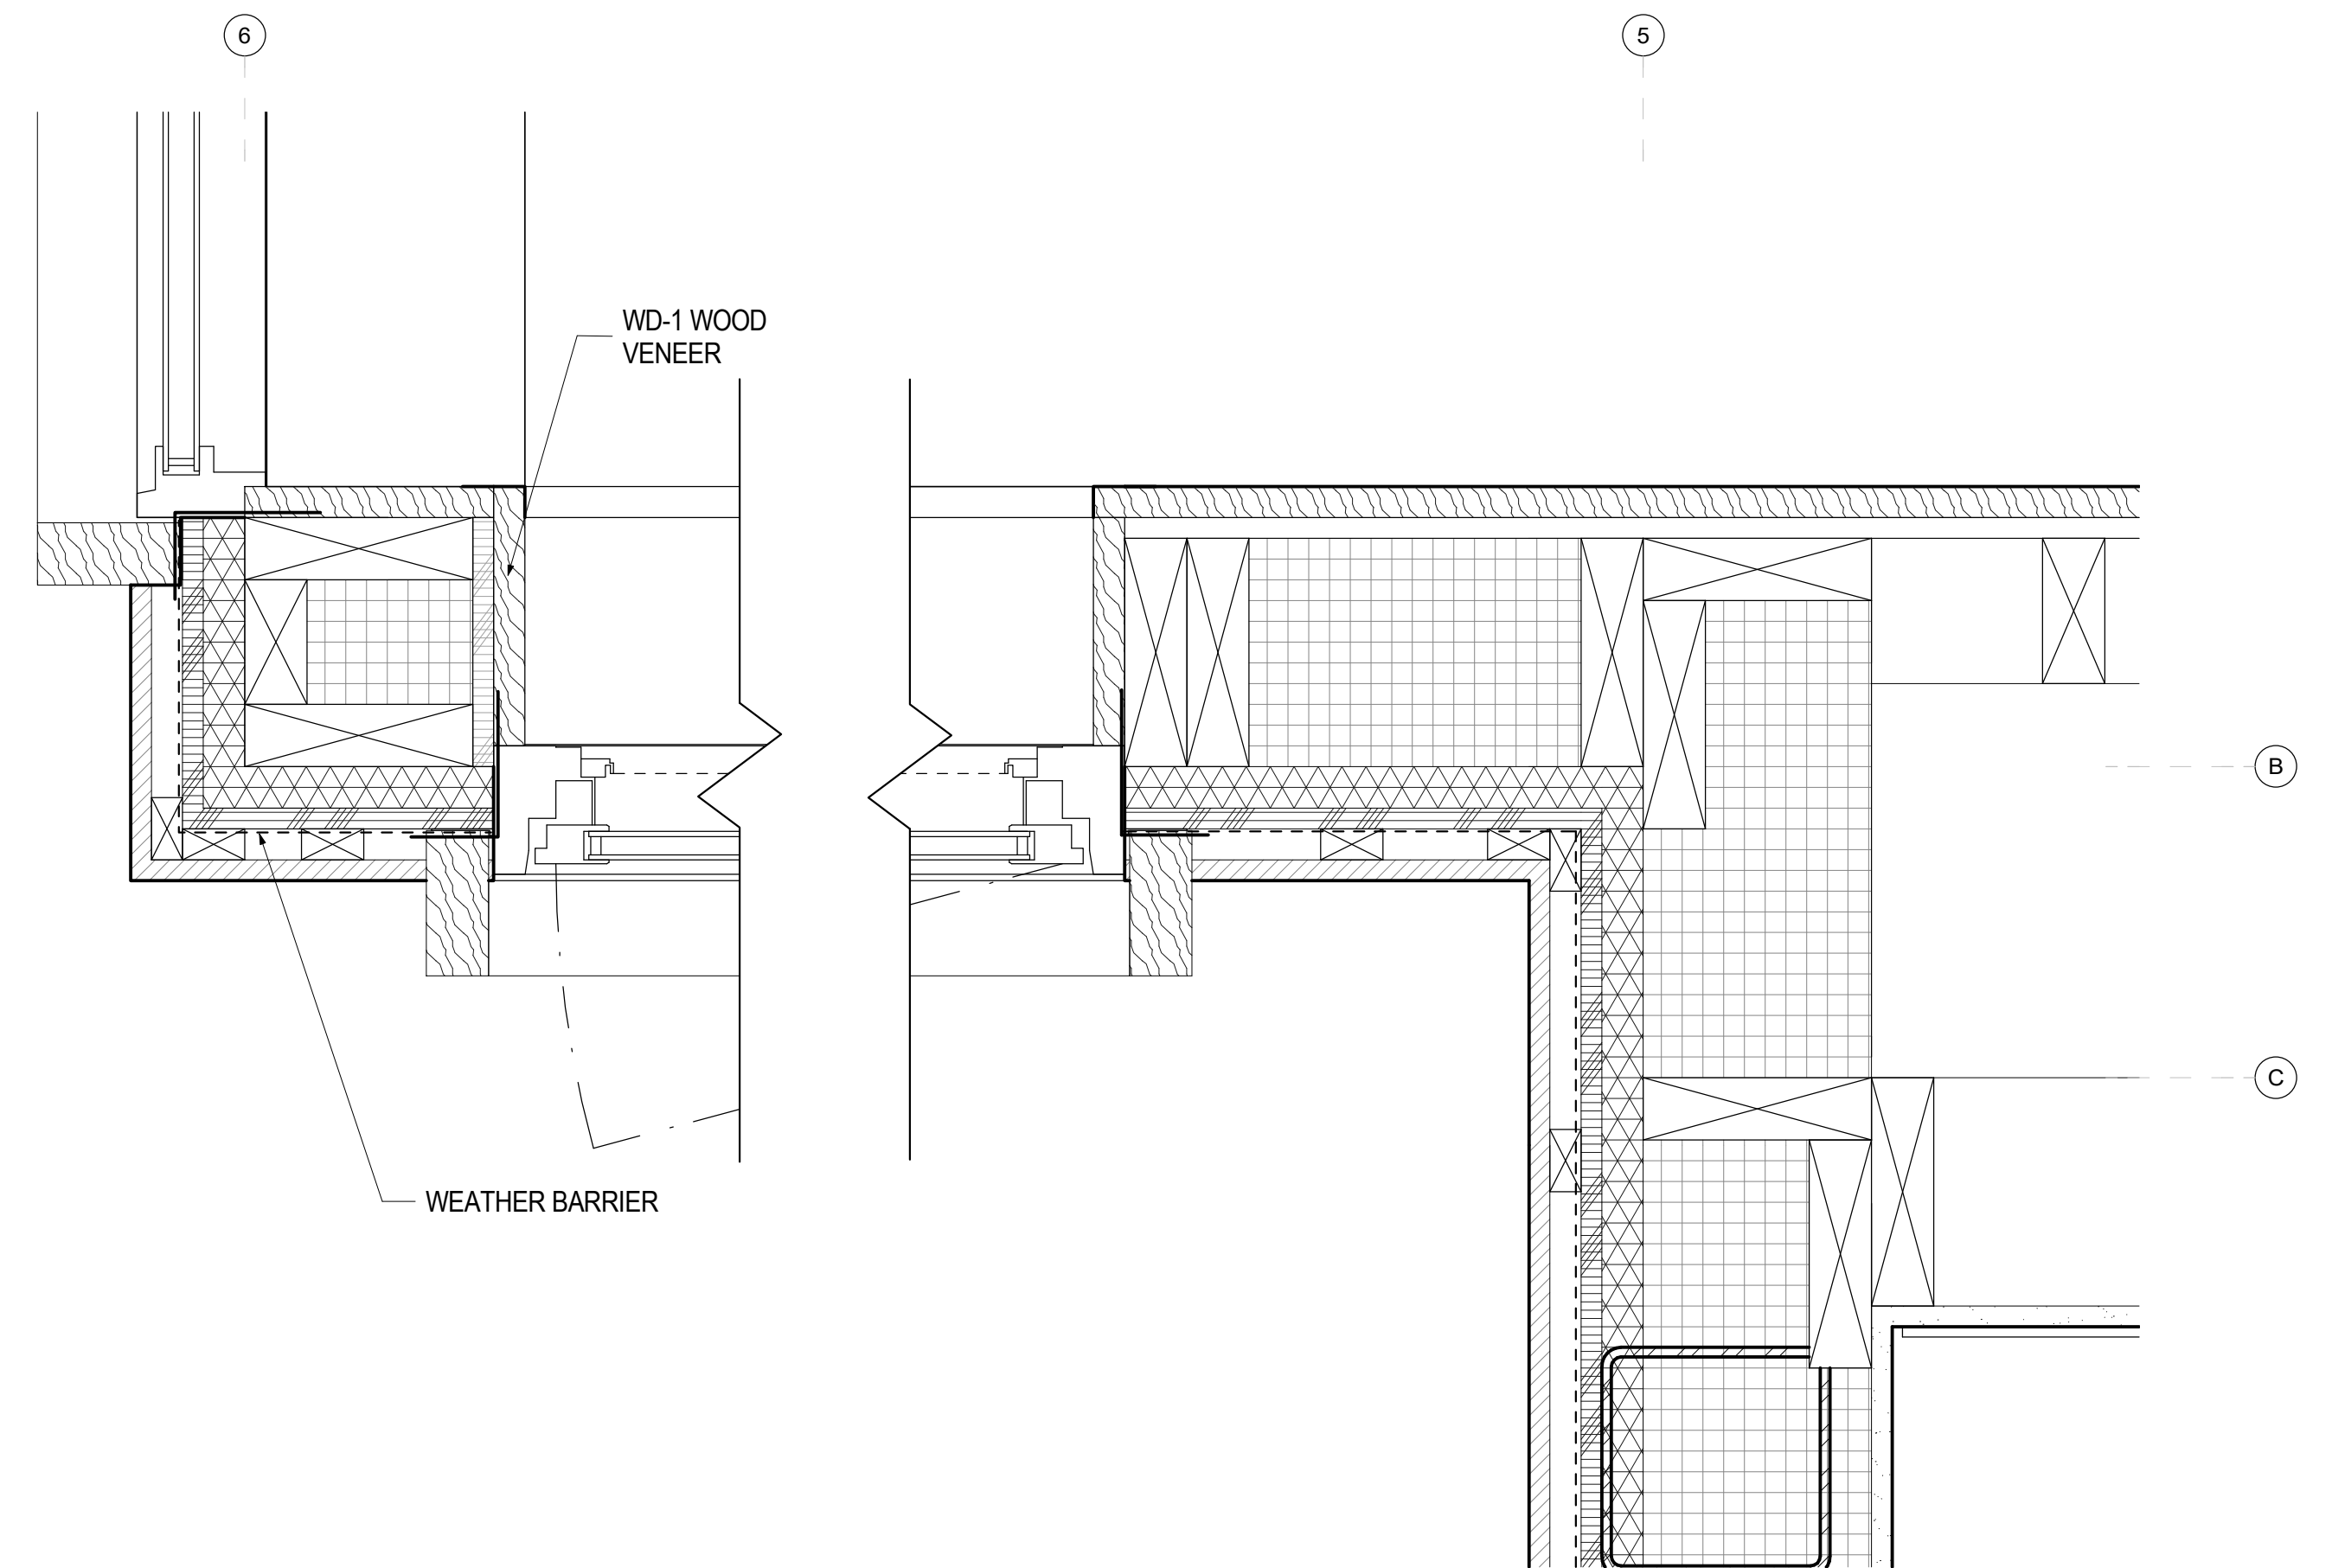


1 JAMB, CORNER WINDOW, READING NOOK
A4.13 3" = 1'-0"

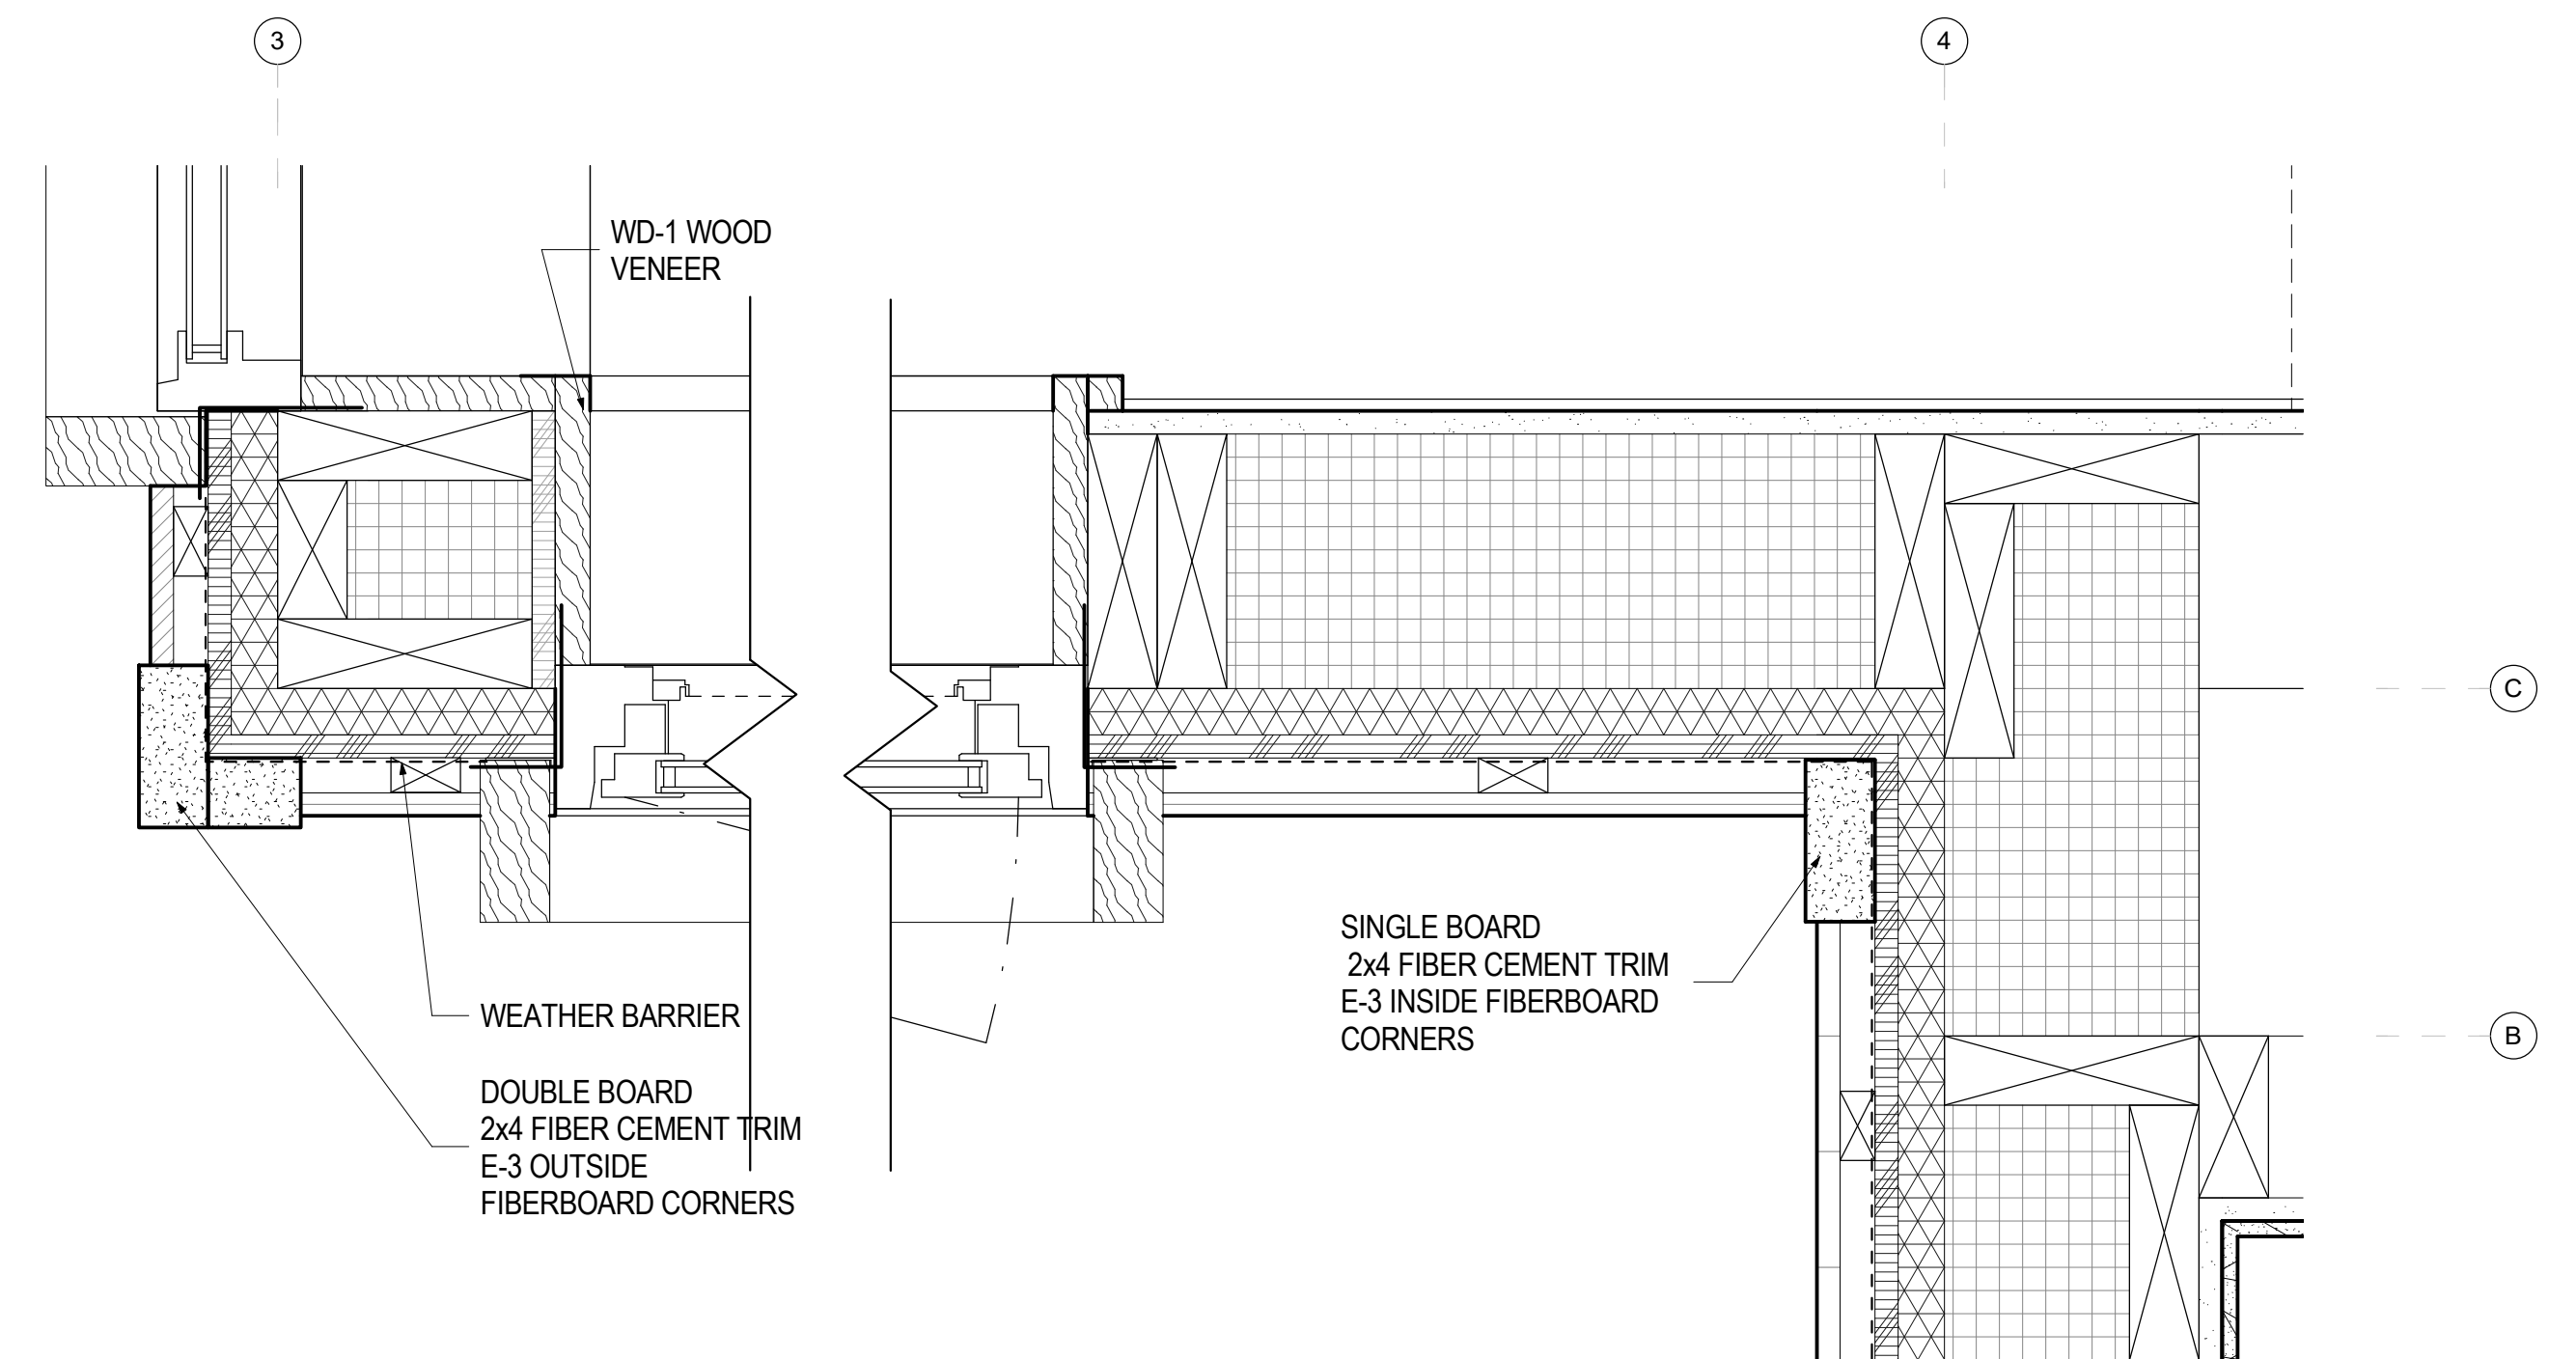


2 JAMB, CORNER WINDOW, KITCHEN
A4.13 3" = 1'-0"

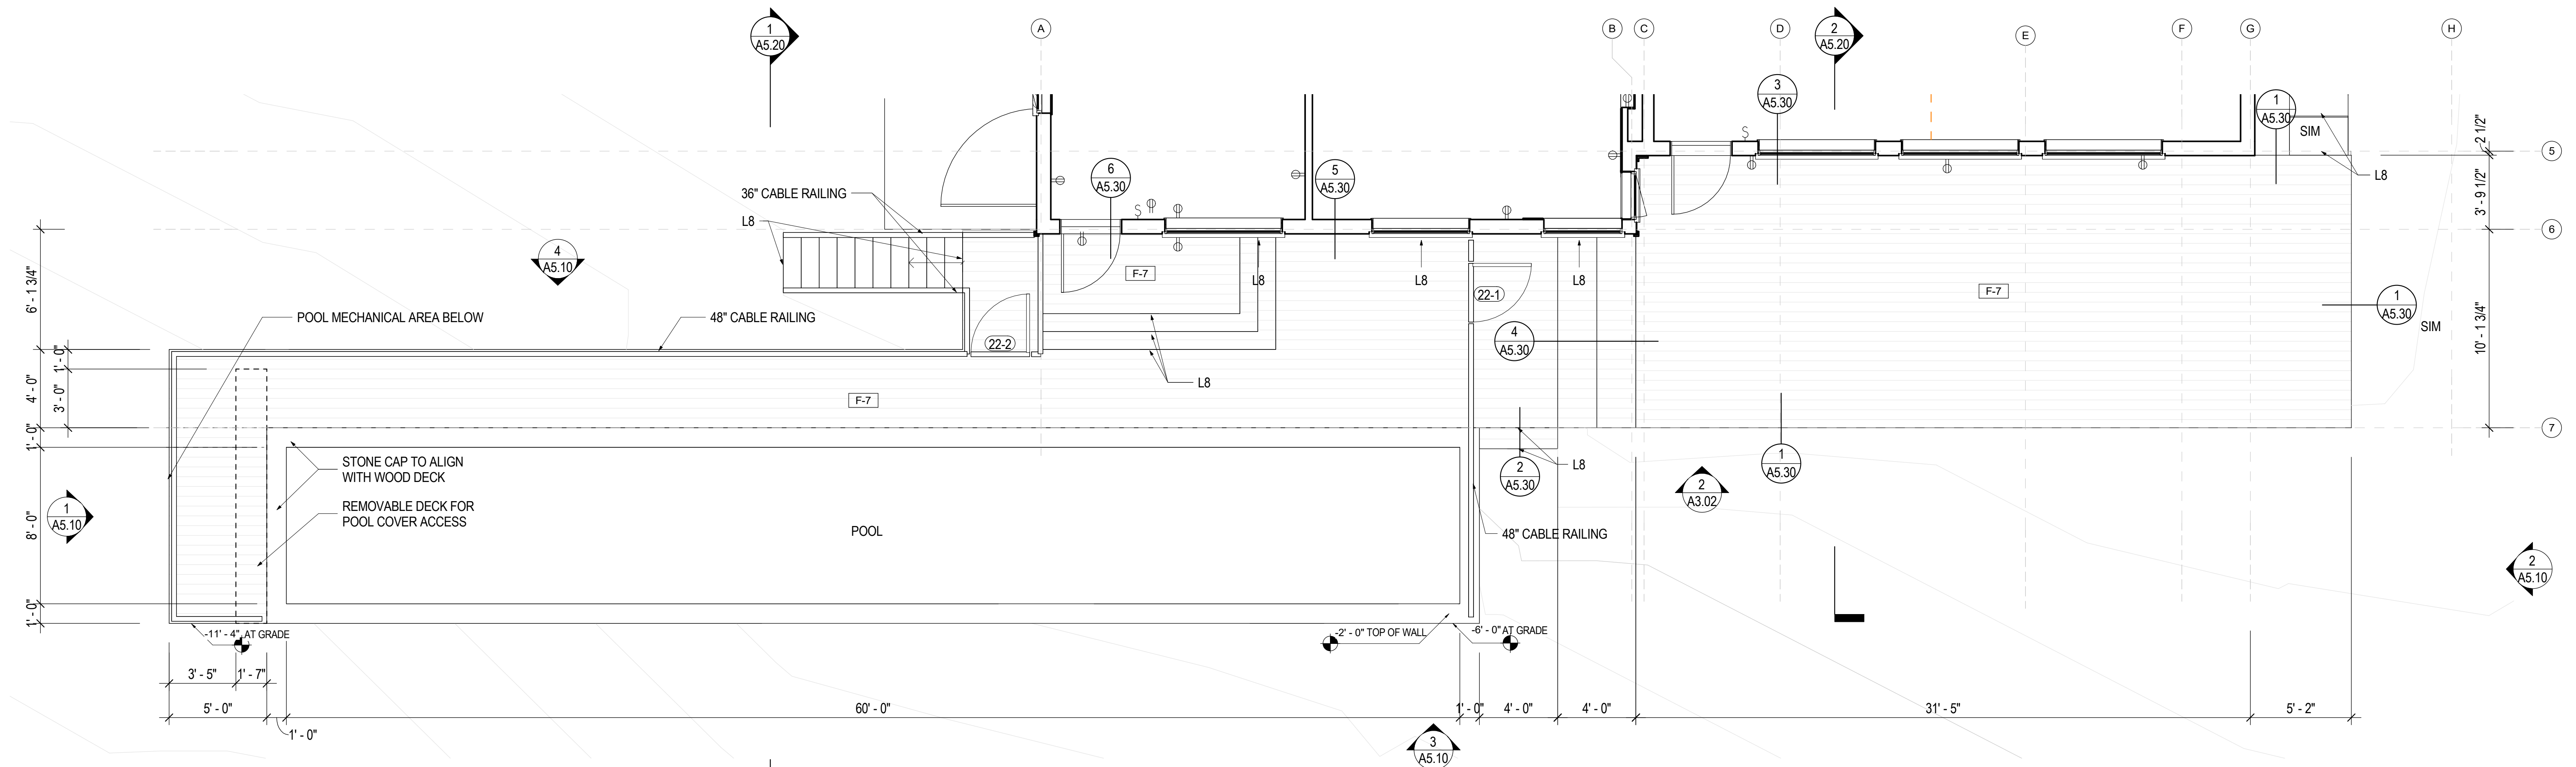


1
A5.01 ENLARGED PLAN, SITE PLAN
1/4" = 1'-0"

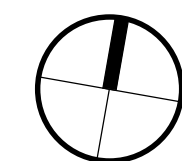


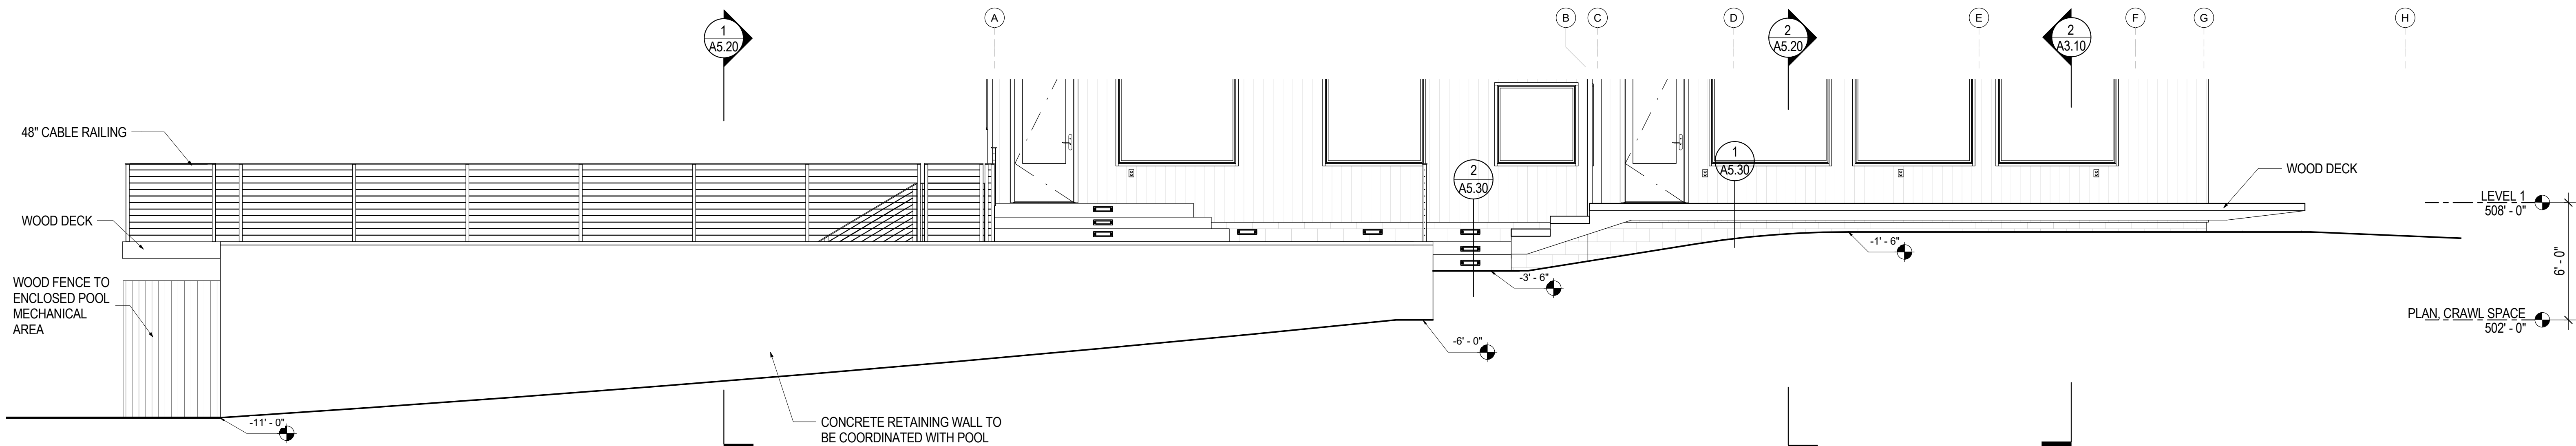


3 NORTH ELEVATION, DECK
A5.10 1/4" = 1'-0"

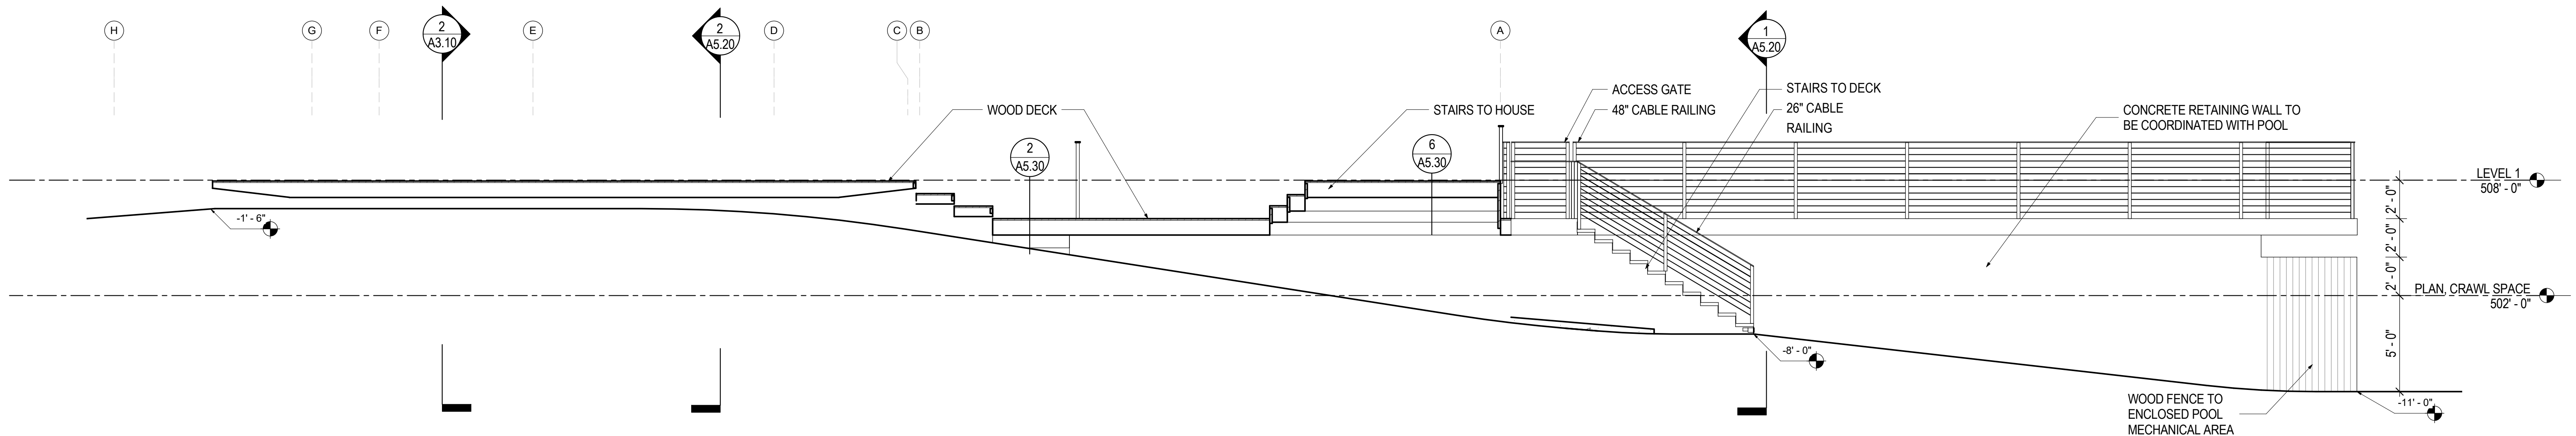


4 SOUTH SECTION, DECK
A5.10 1/4" = 1'-0"

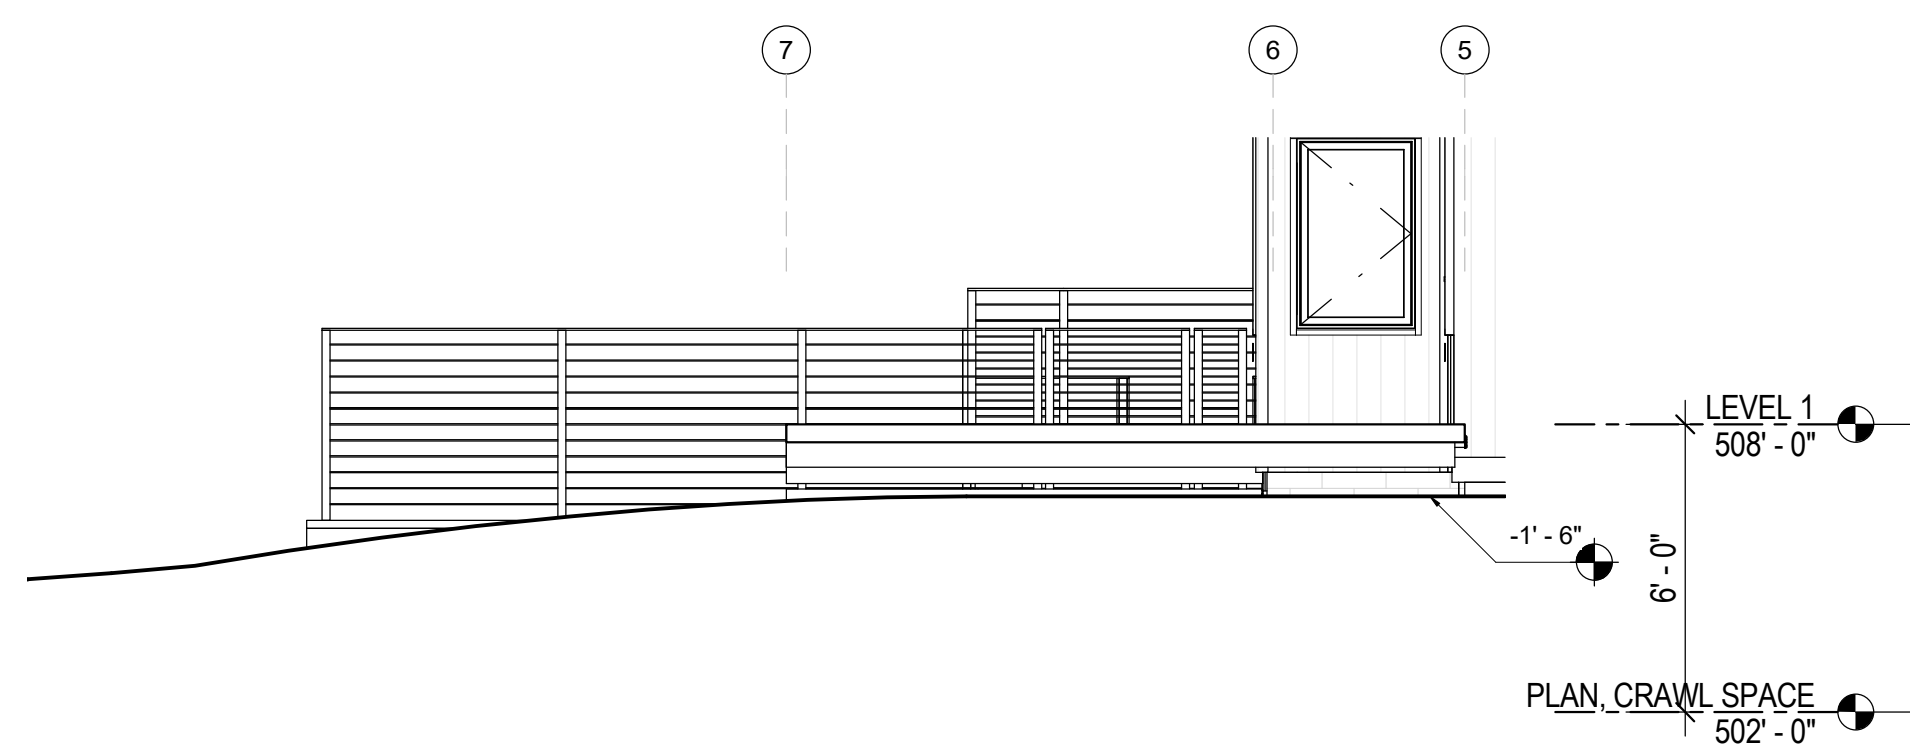


2 EAST ELEVATION, DECK
A5.10 1/4" = 1'-0"

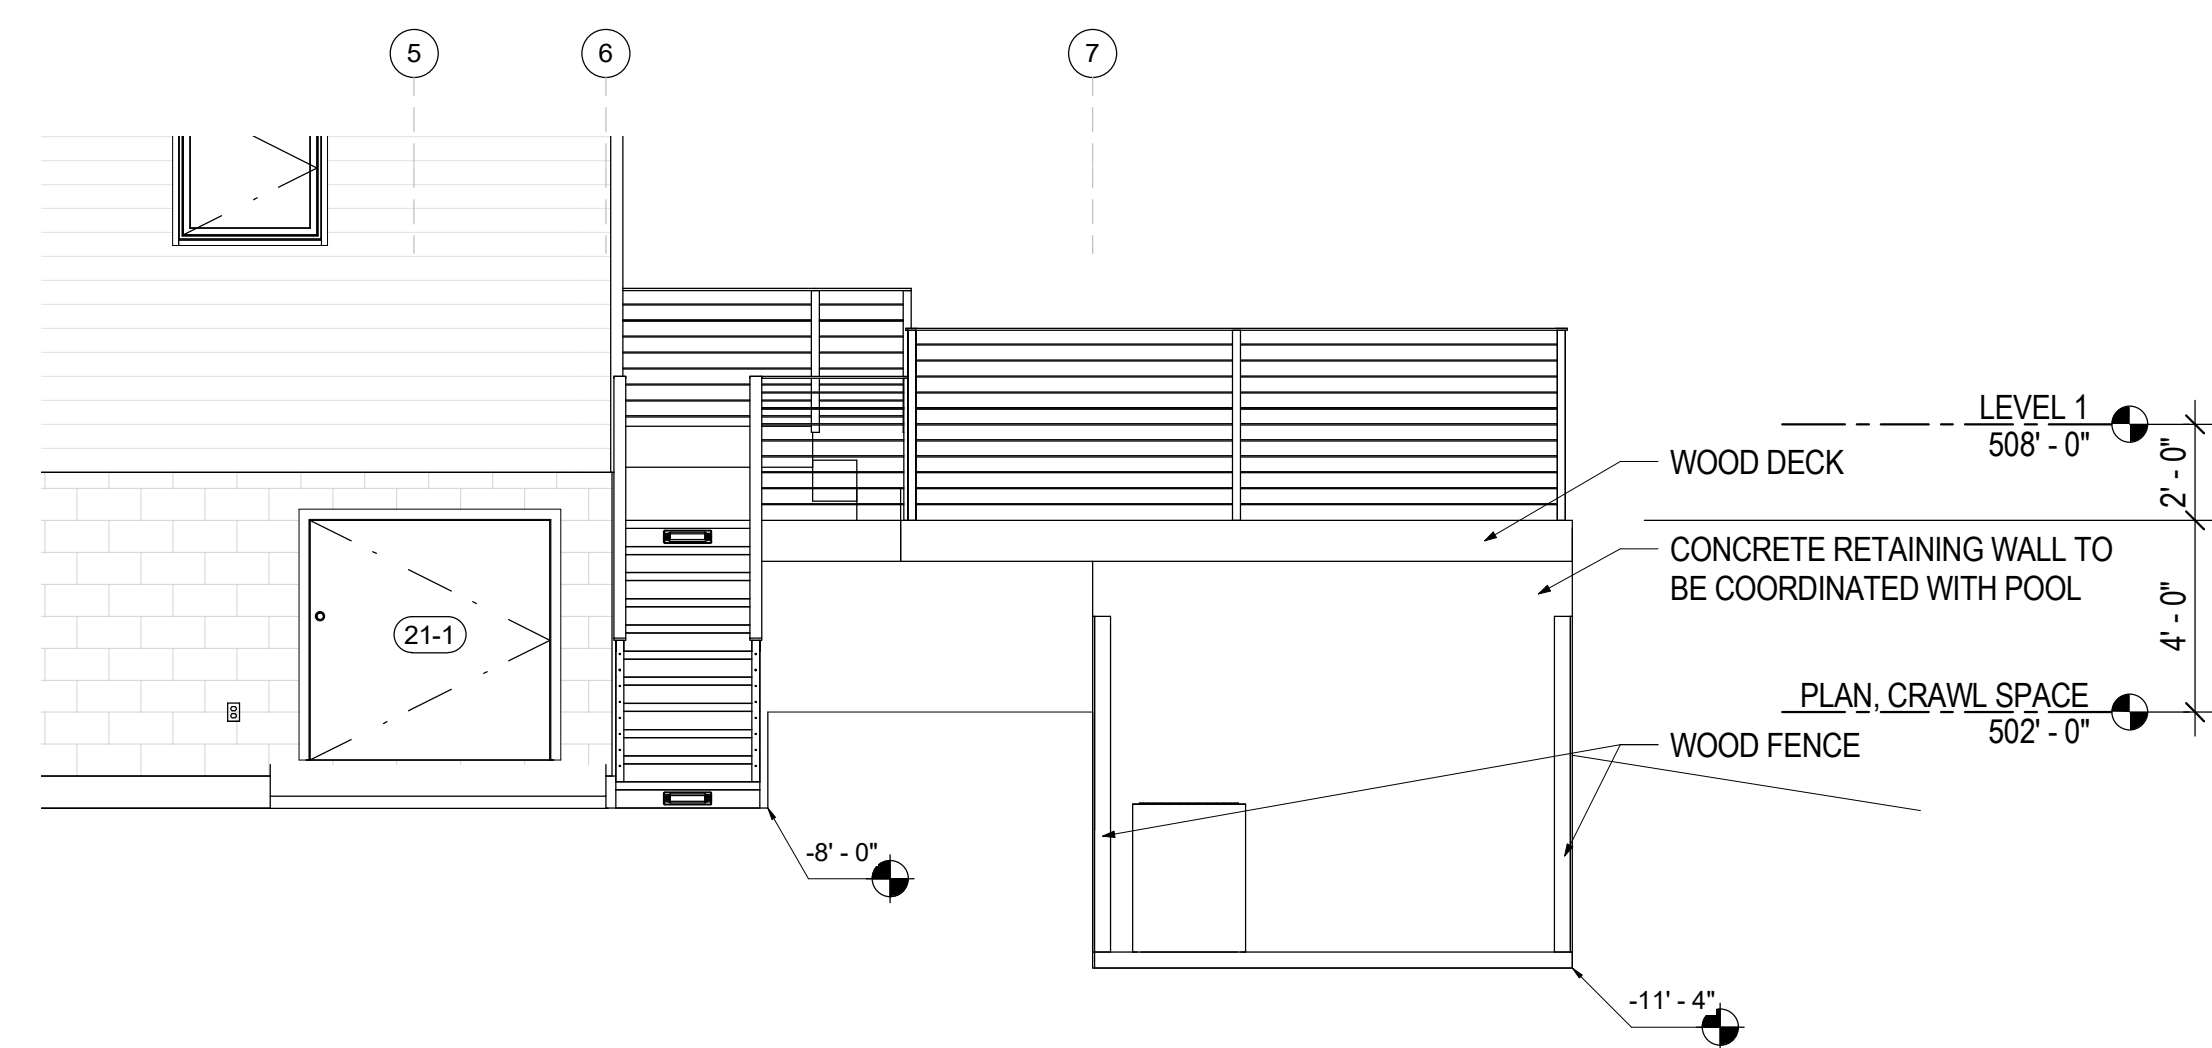


1 WEST ELEVATION, DECK
A5.10 1/4" = 1'-0"

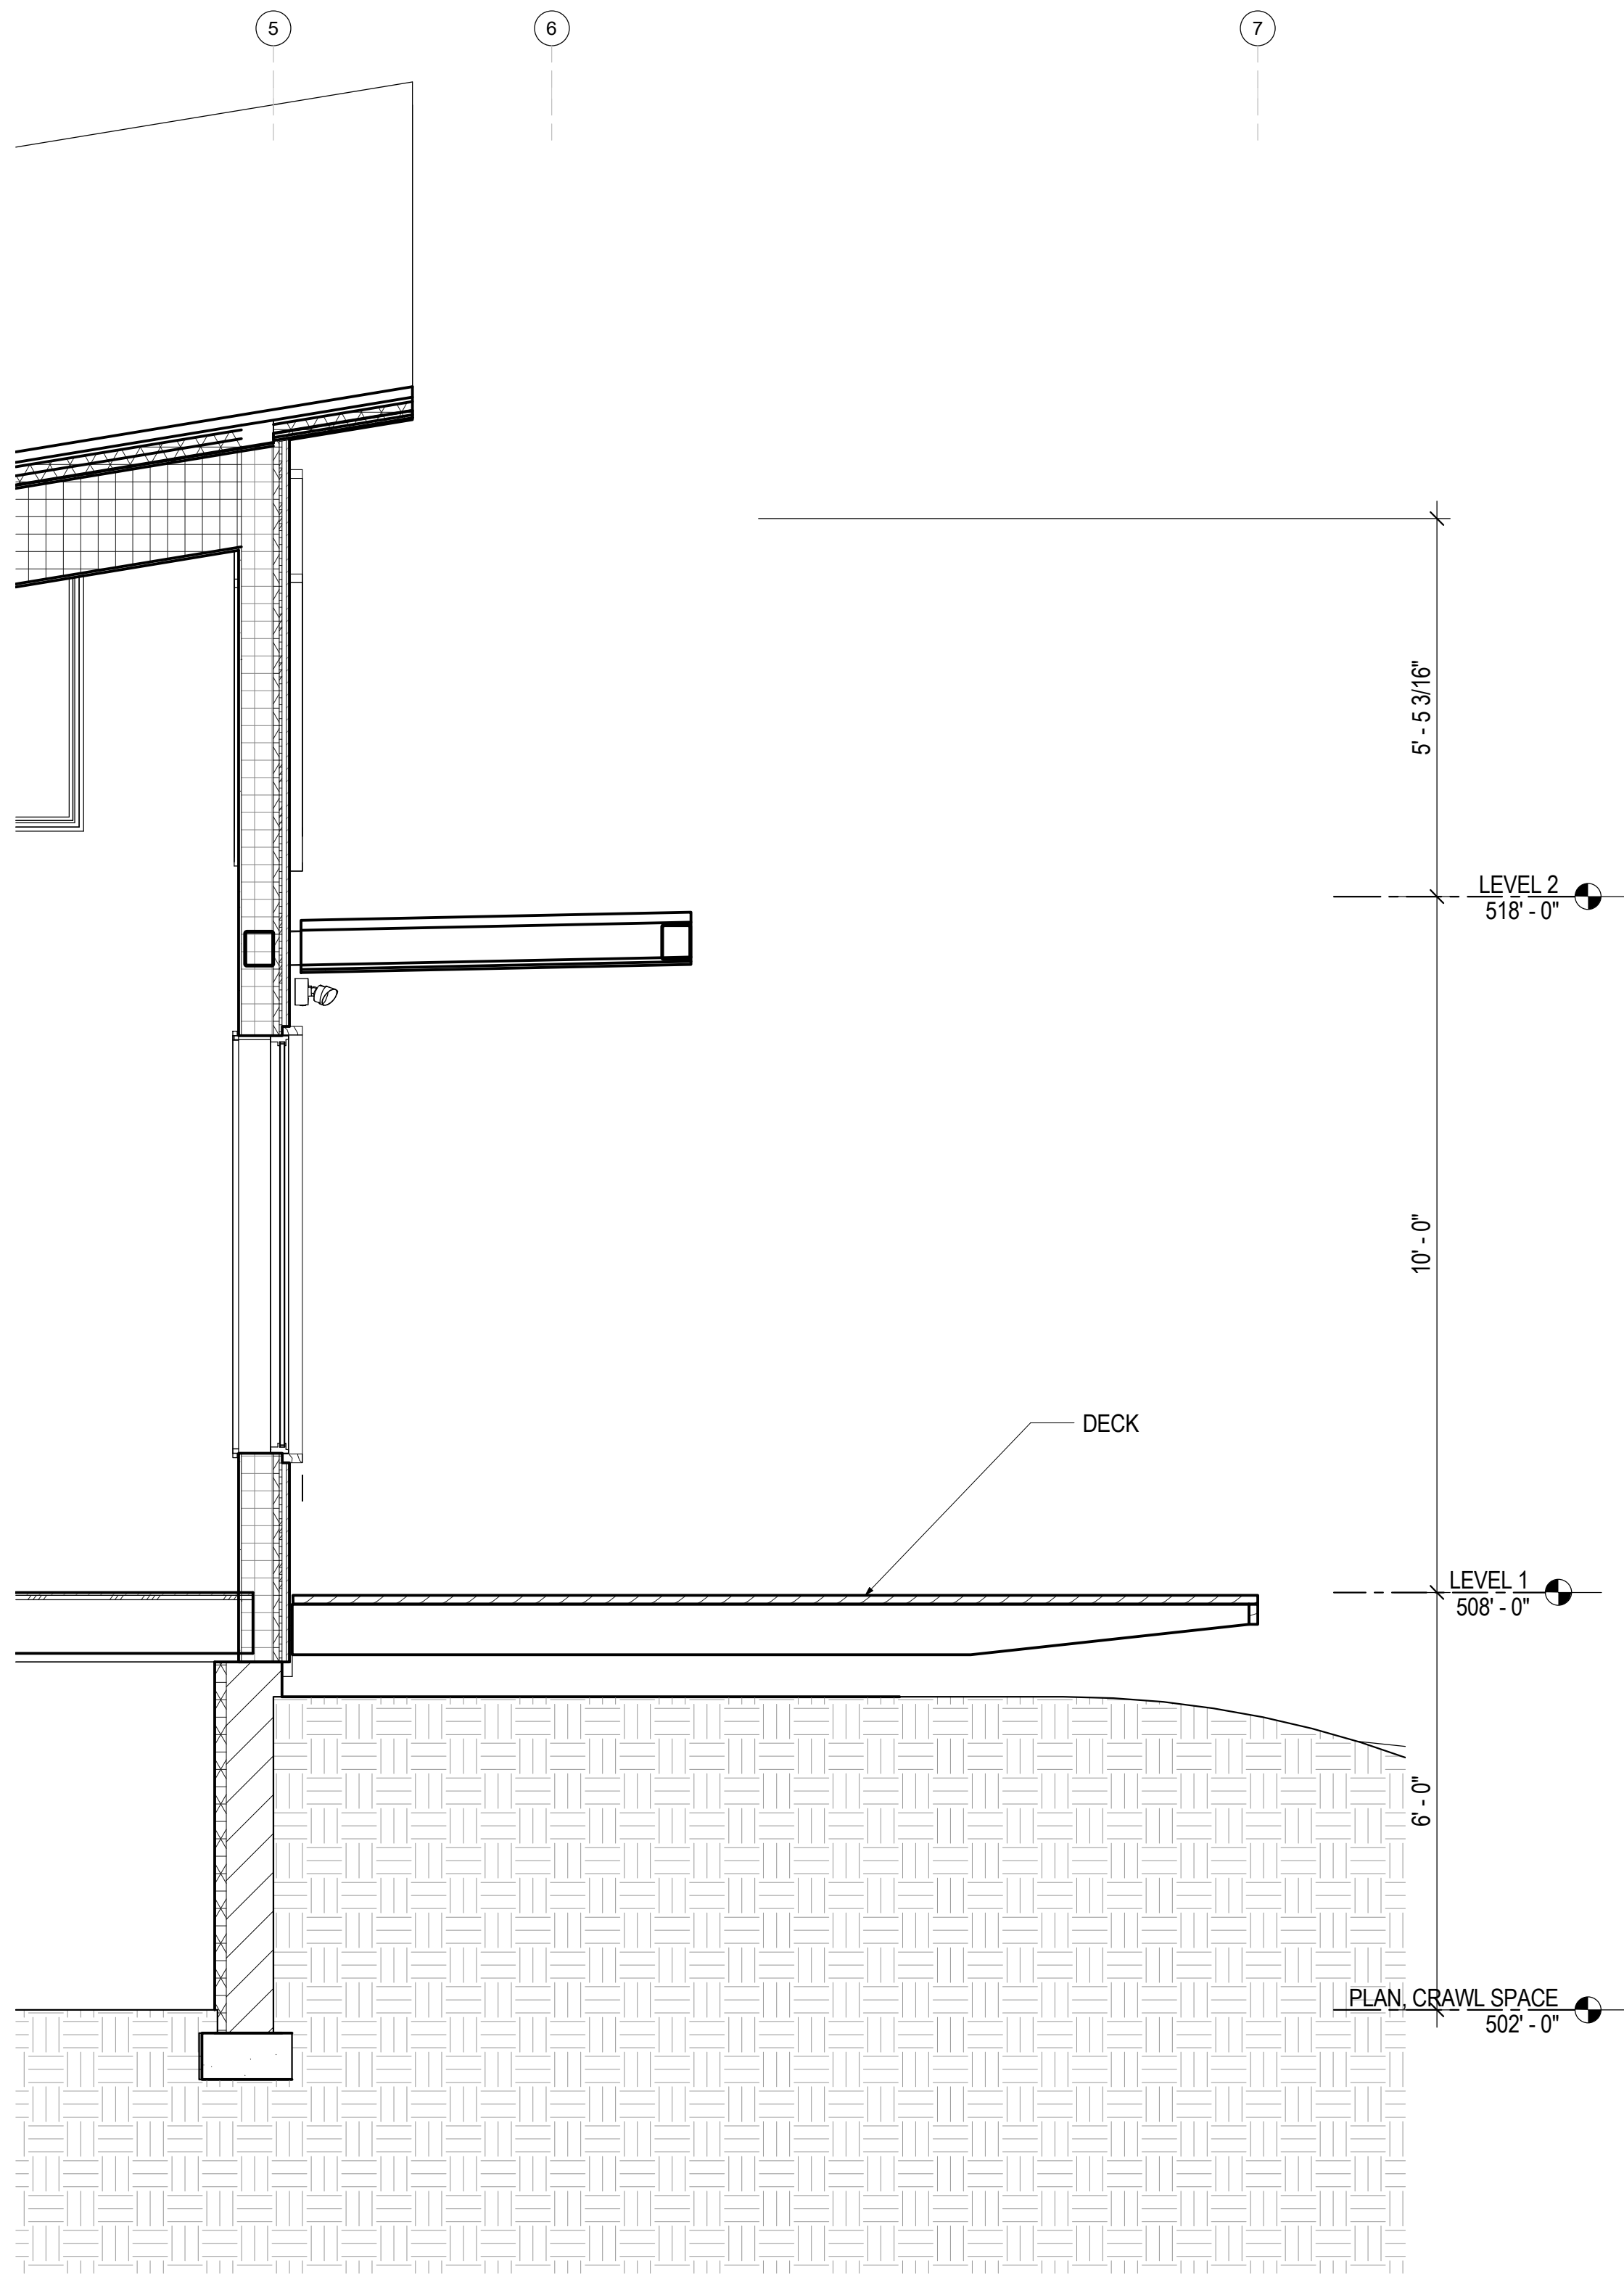


2 SECTION, DECK
A5.20 1/2" = 1'-0"

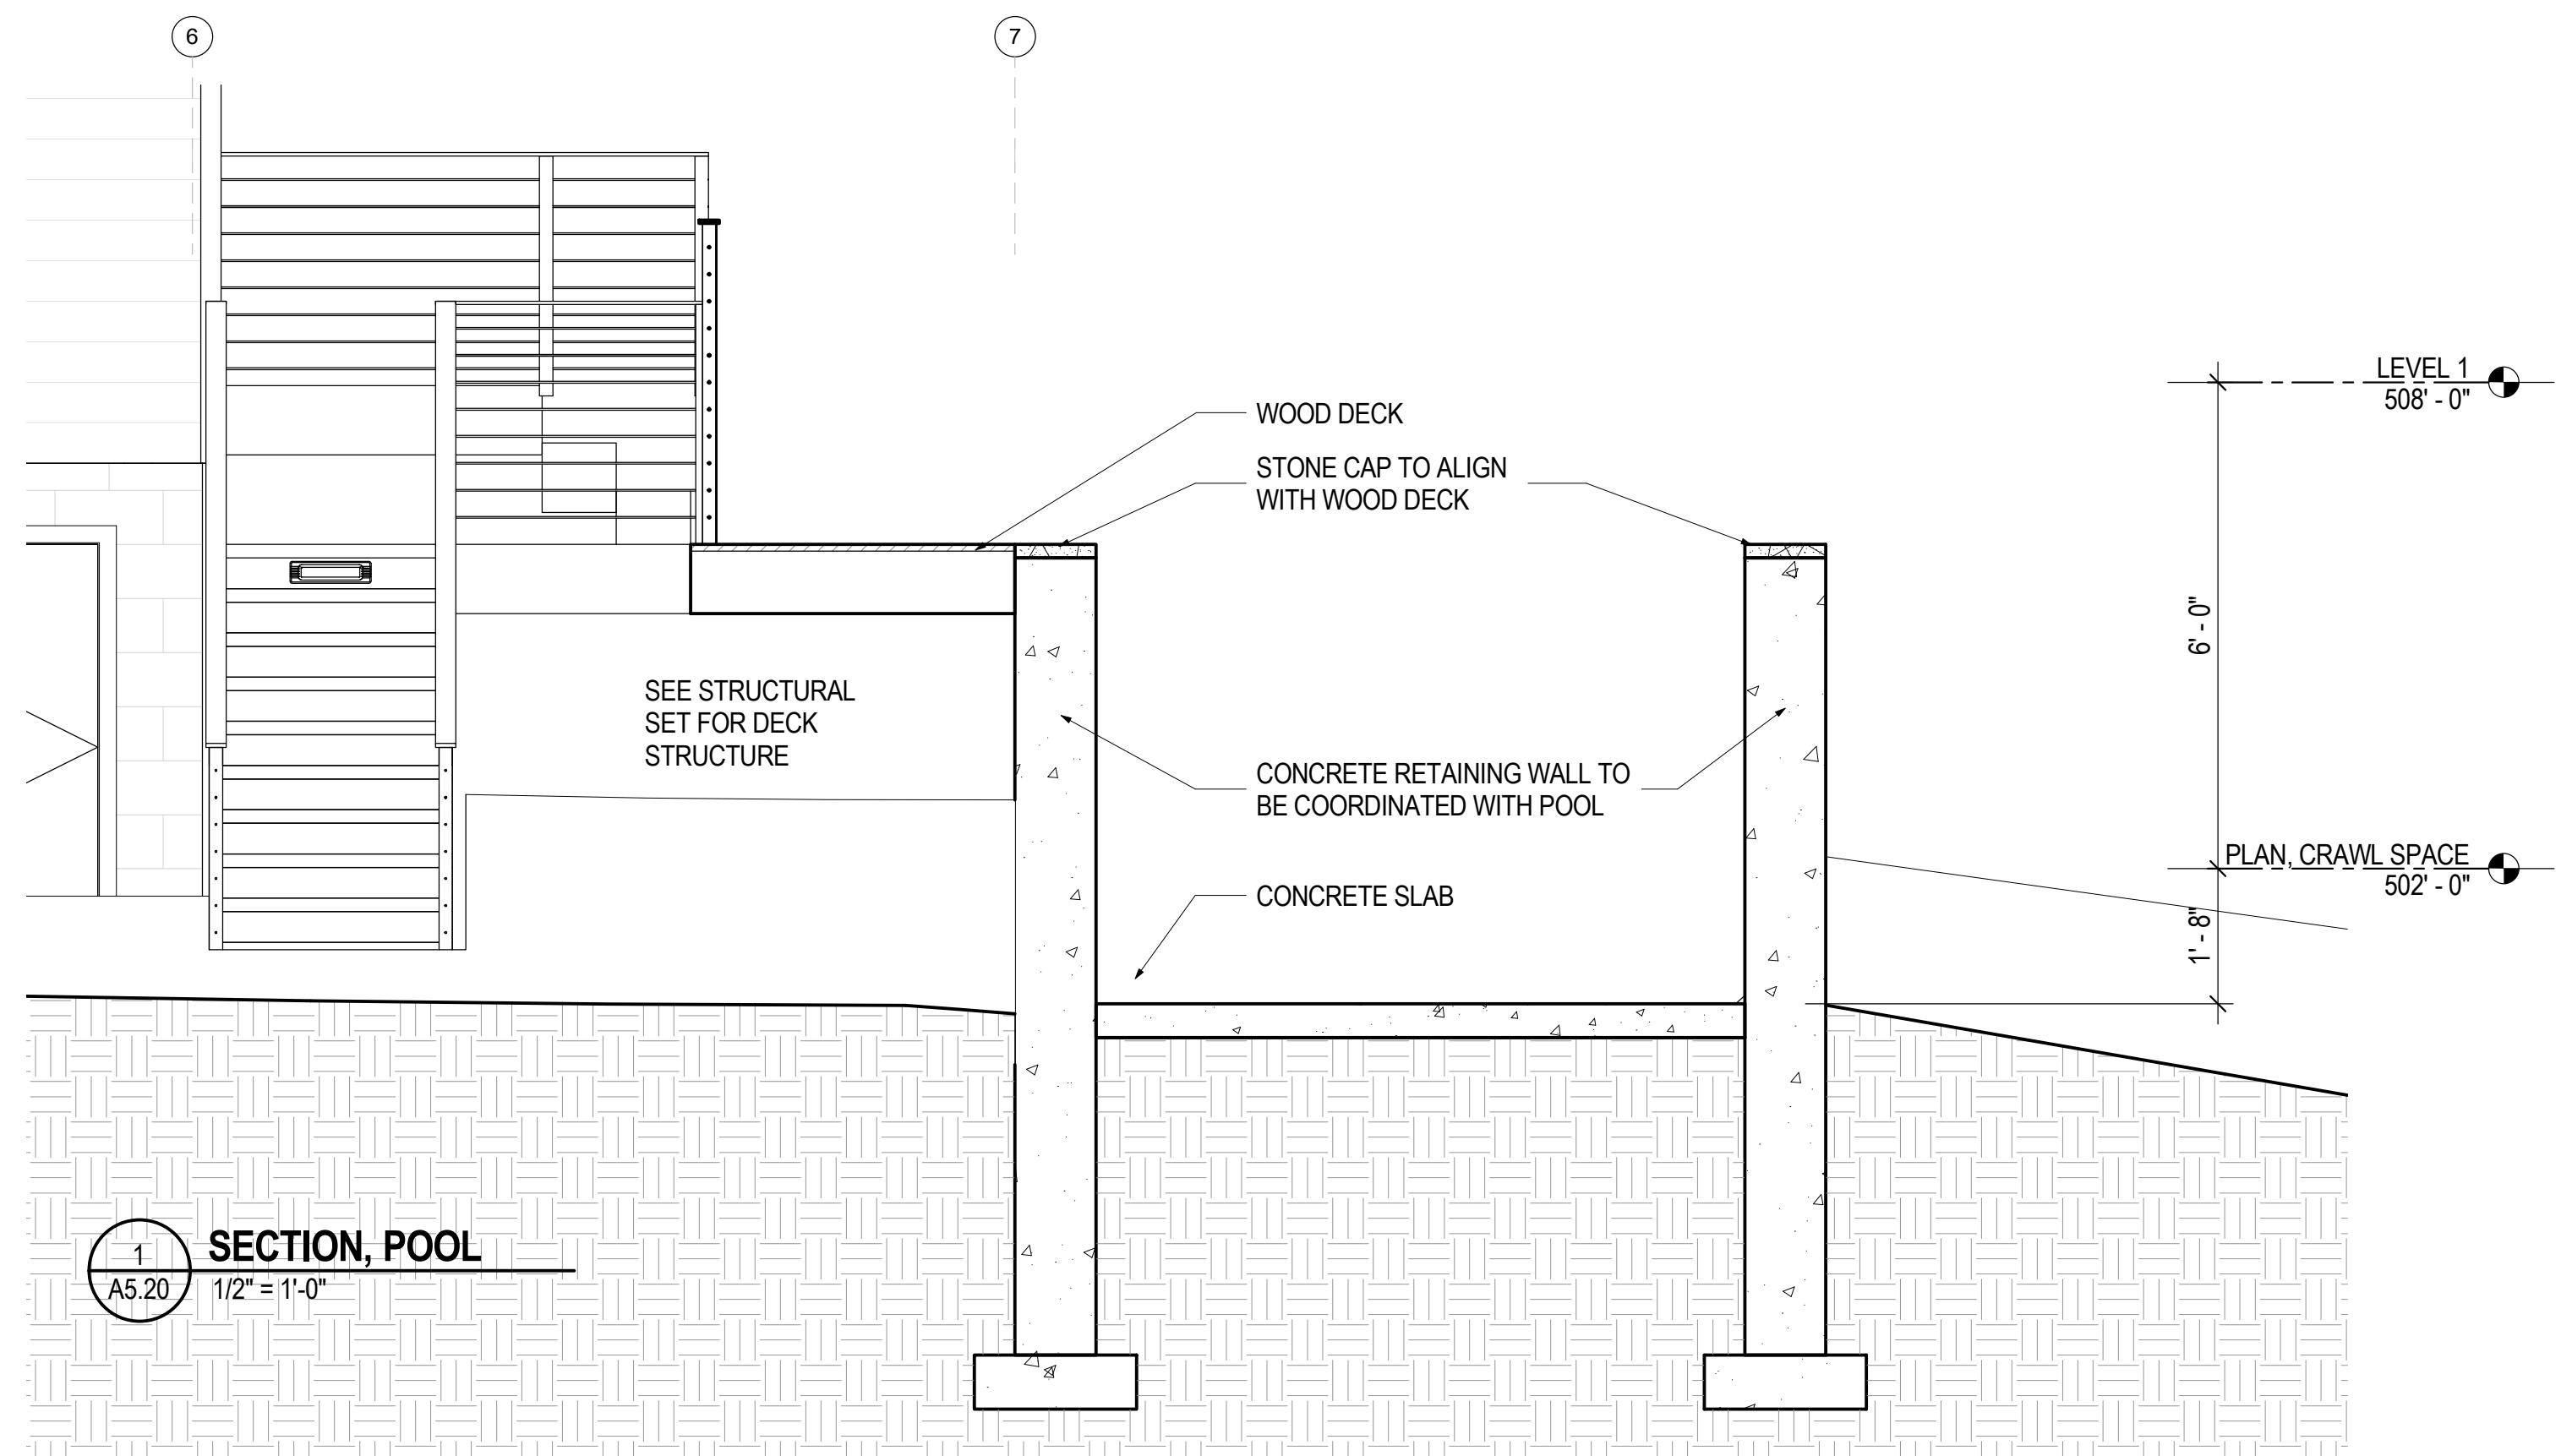


1 SECTION, POOL
A5.20 1/2" = 1'-0"

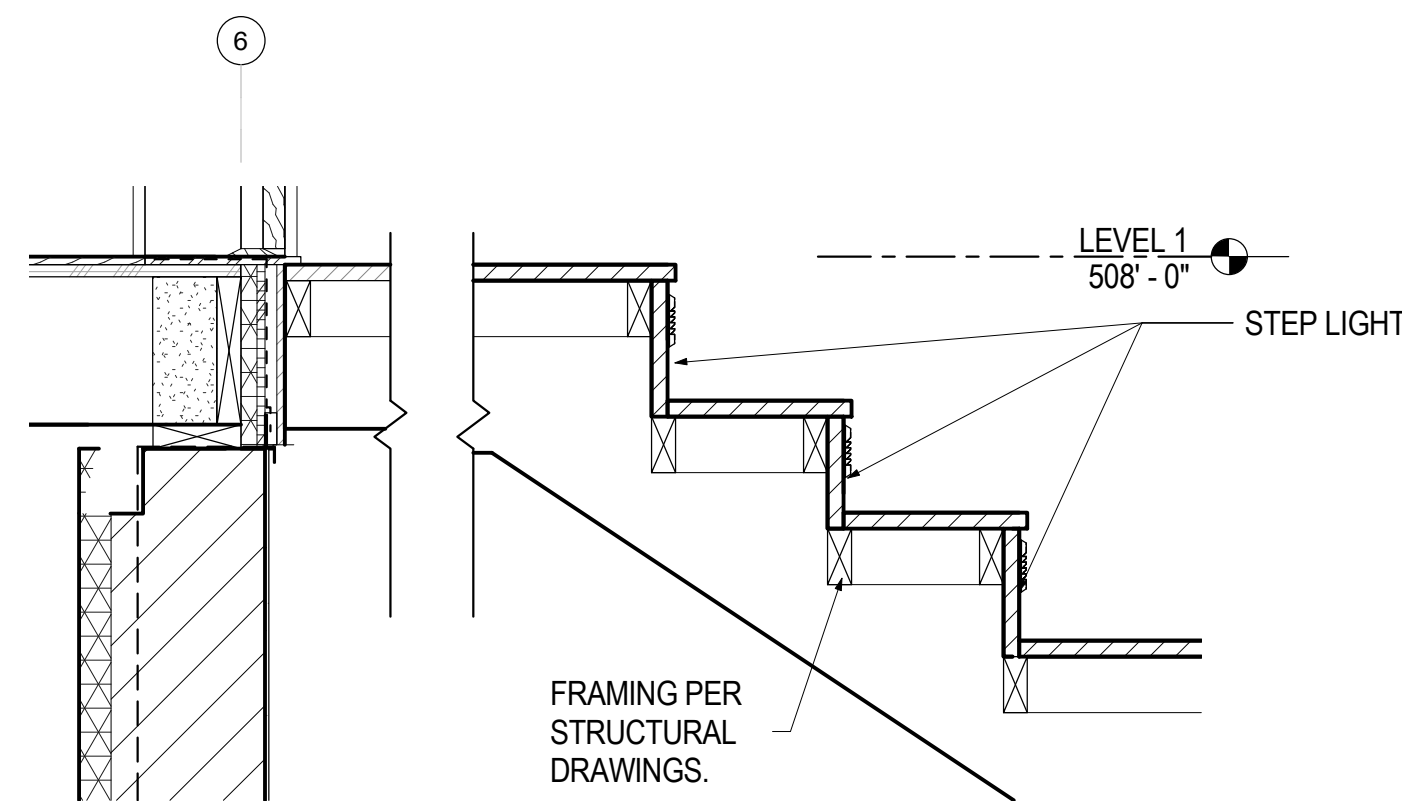


6 SECTION, MASTER BEDROOM TO DECK
1" = 1'-0"

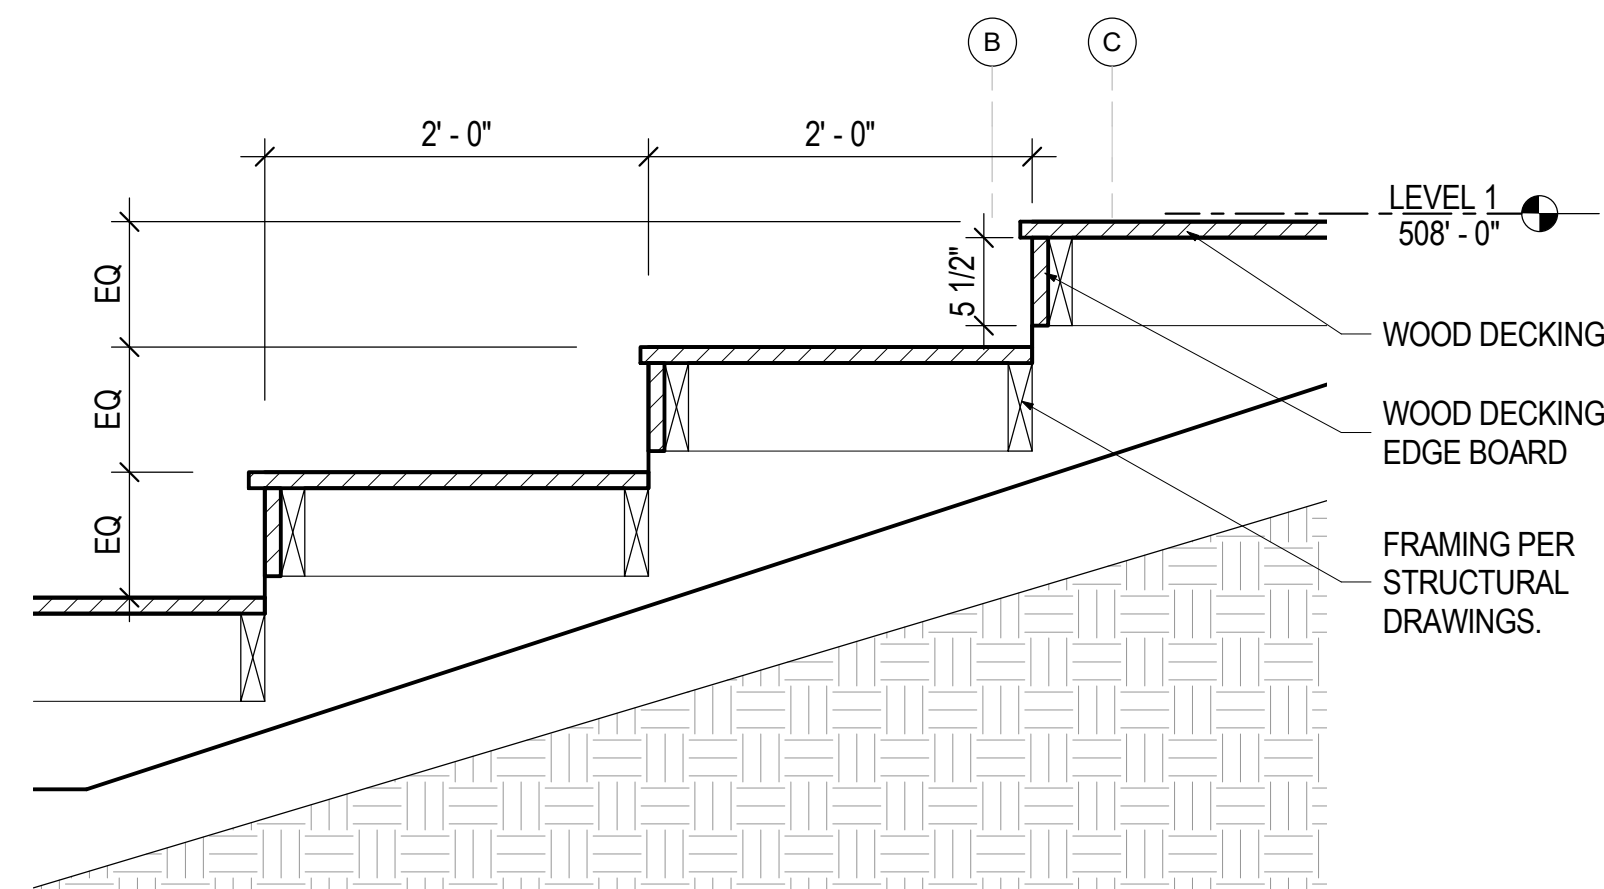


4 SECTION, WOOD STAIR
1" = 1'-0"

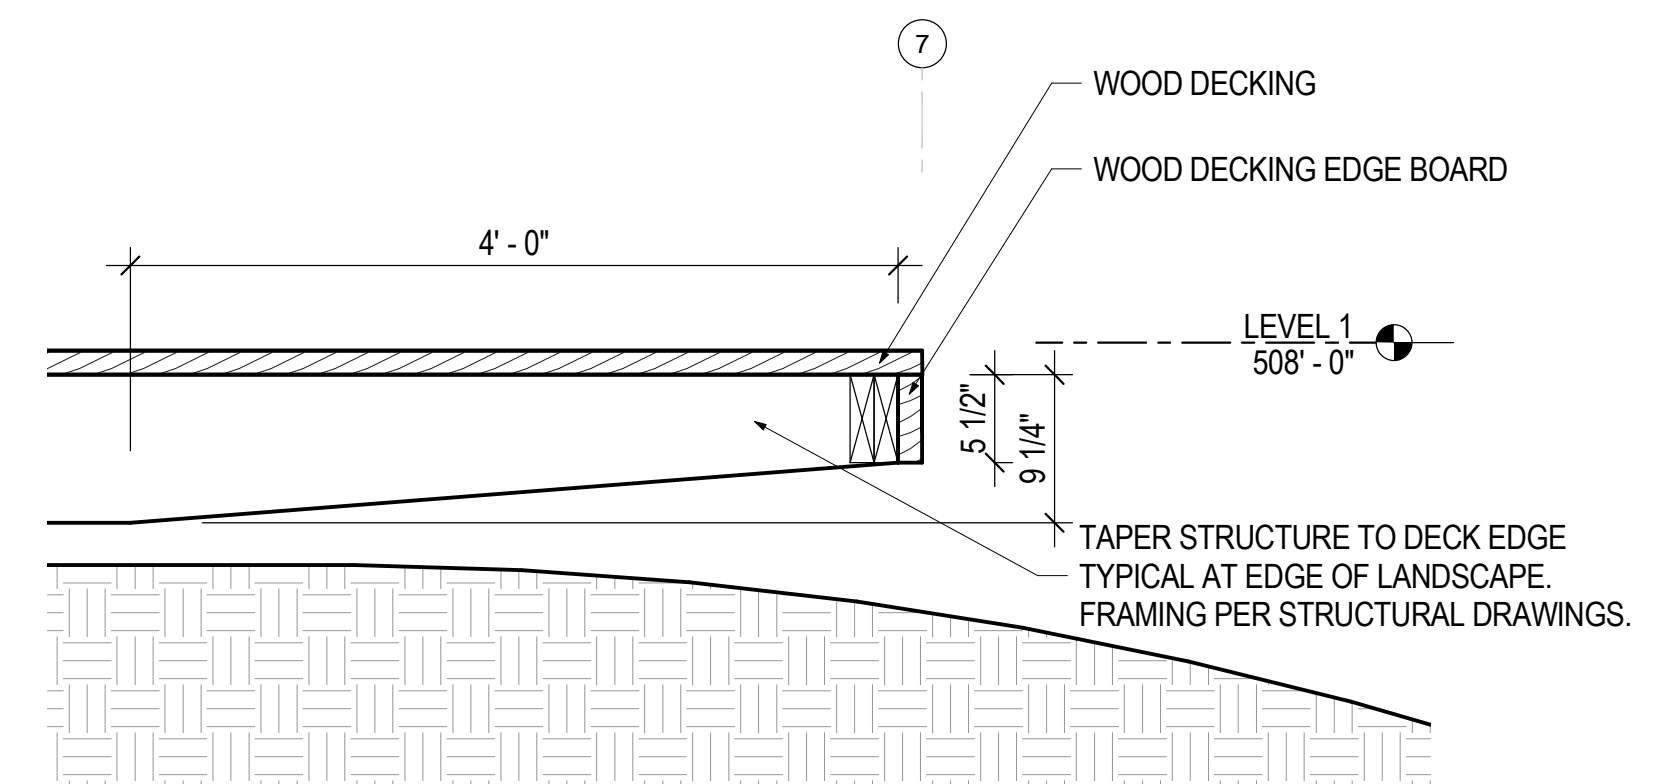


1 SECTION, DECK EDGE AT LANDSCAPE
1" = 1'-0"

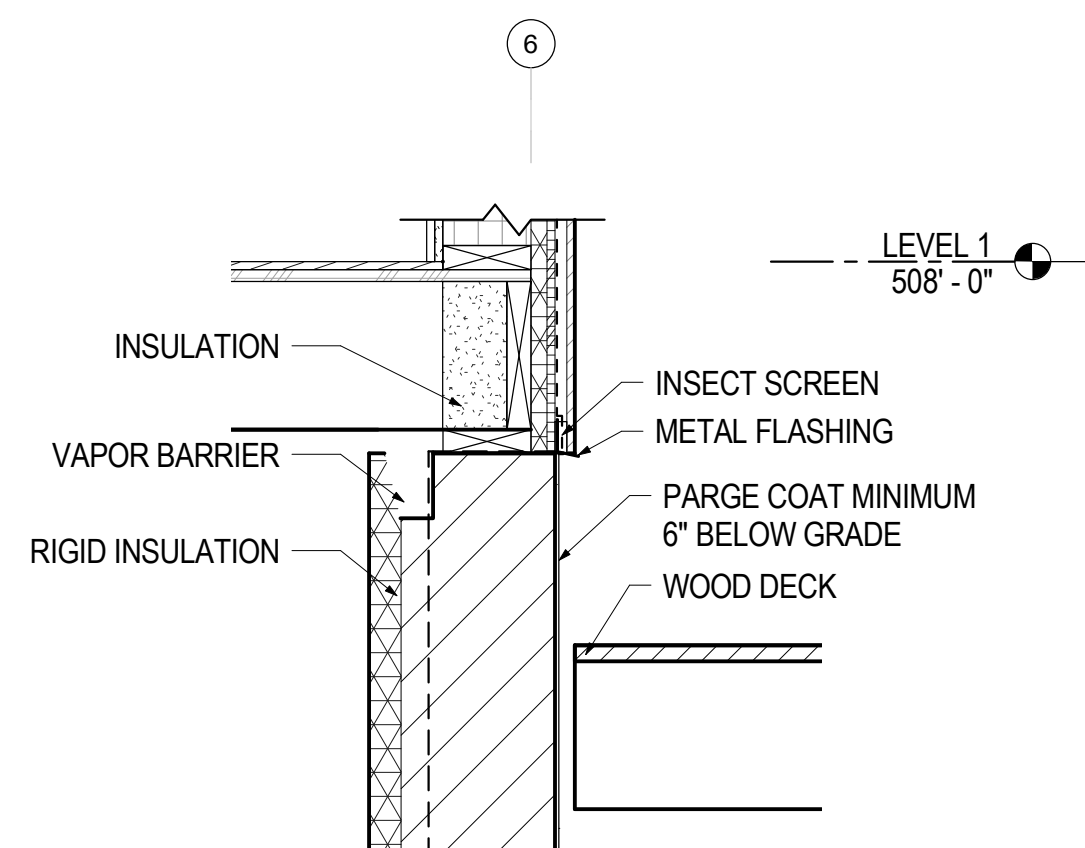


5 BASE, LOWER DECK
1" = 1'-0"

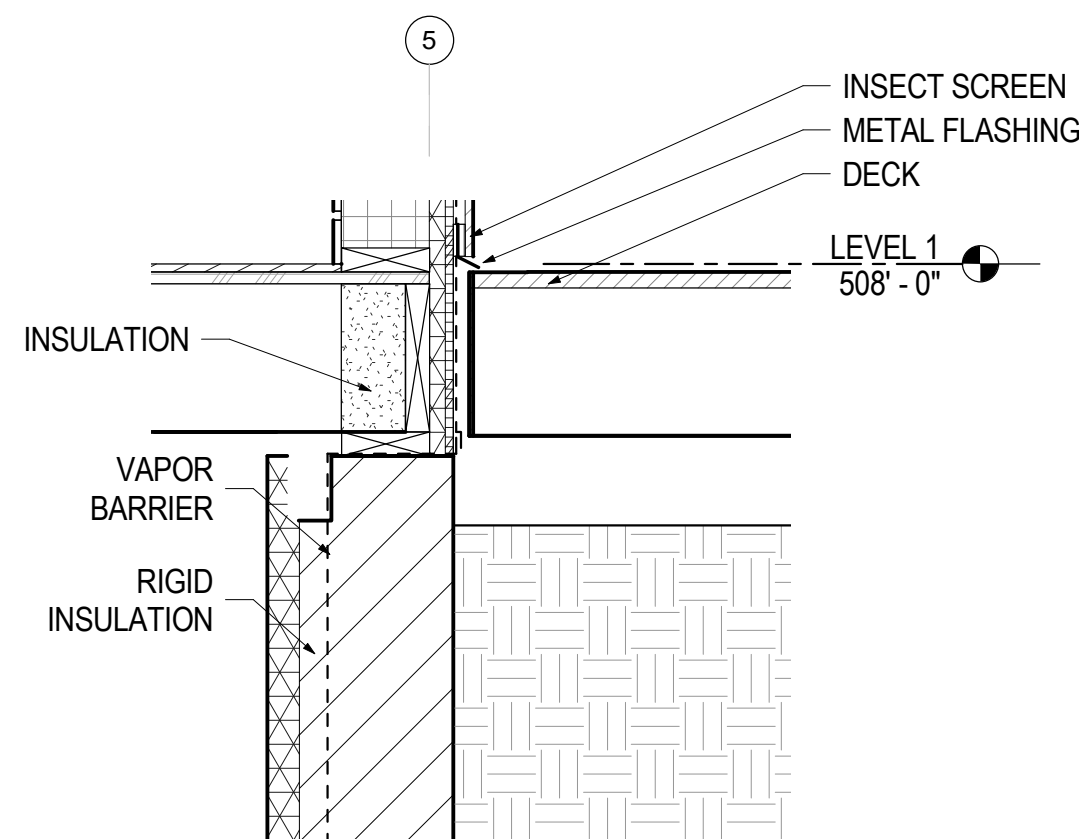


3 BASE, UPPER DECK
1" = 1'-0"

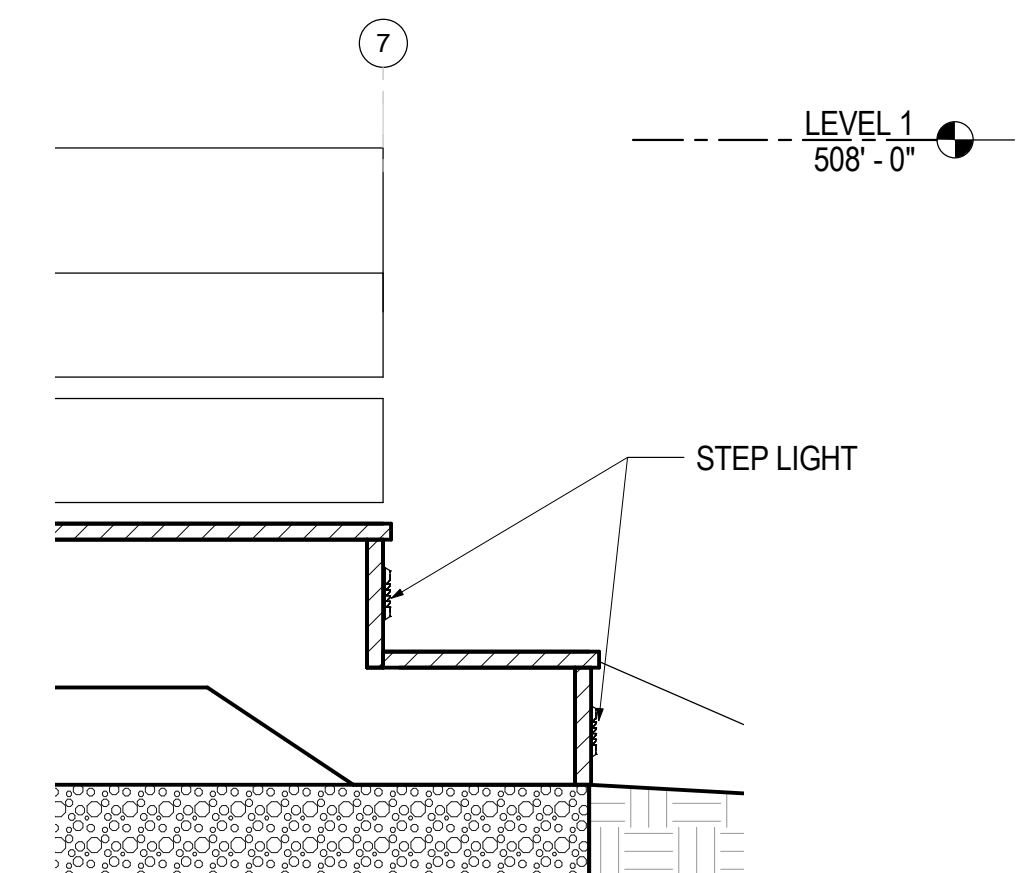

2 SECTION, SOUTH STAIR
1" = 1'-0"

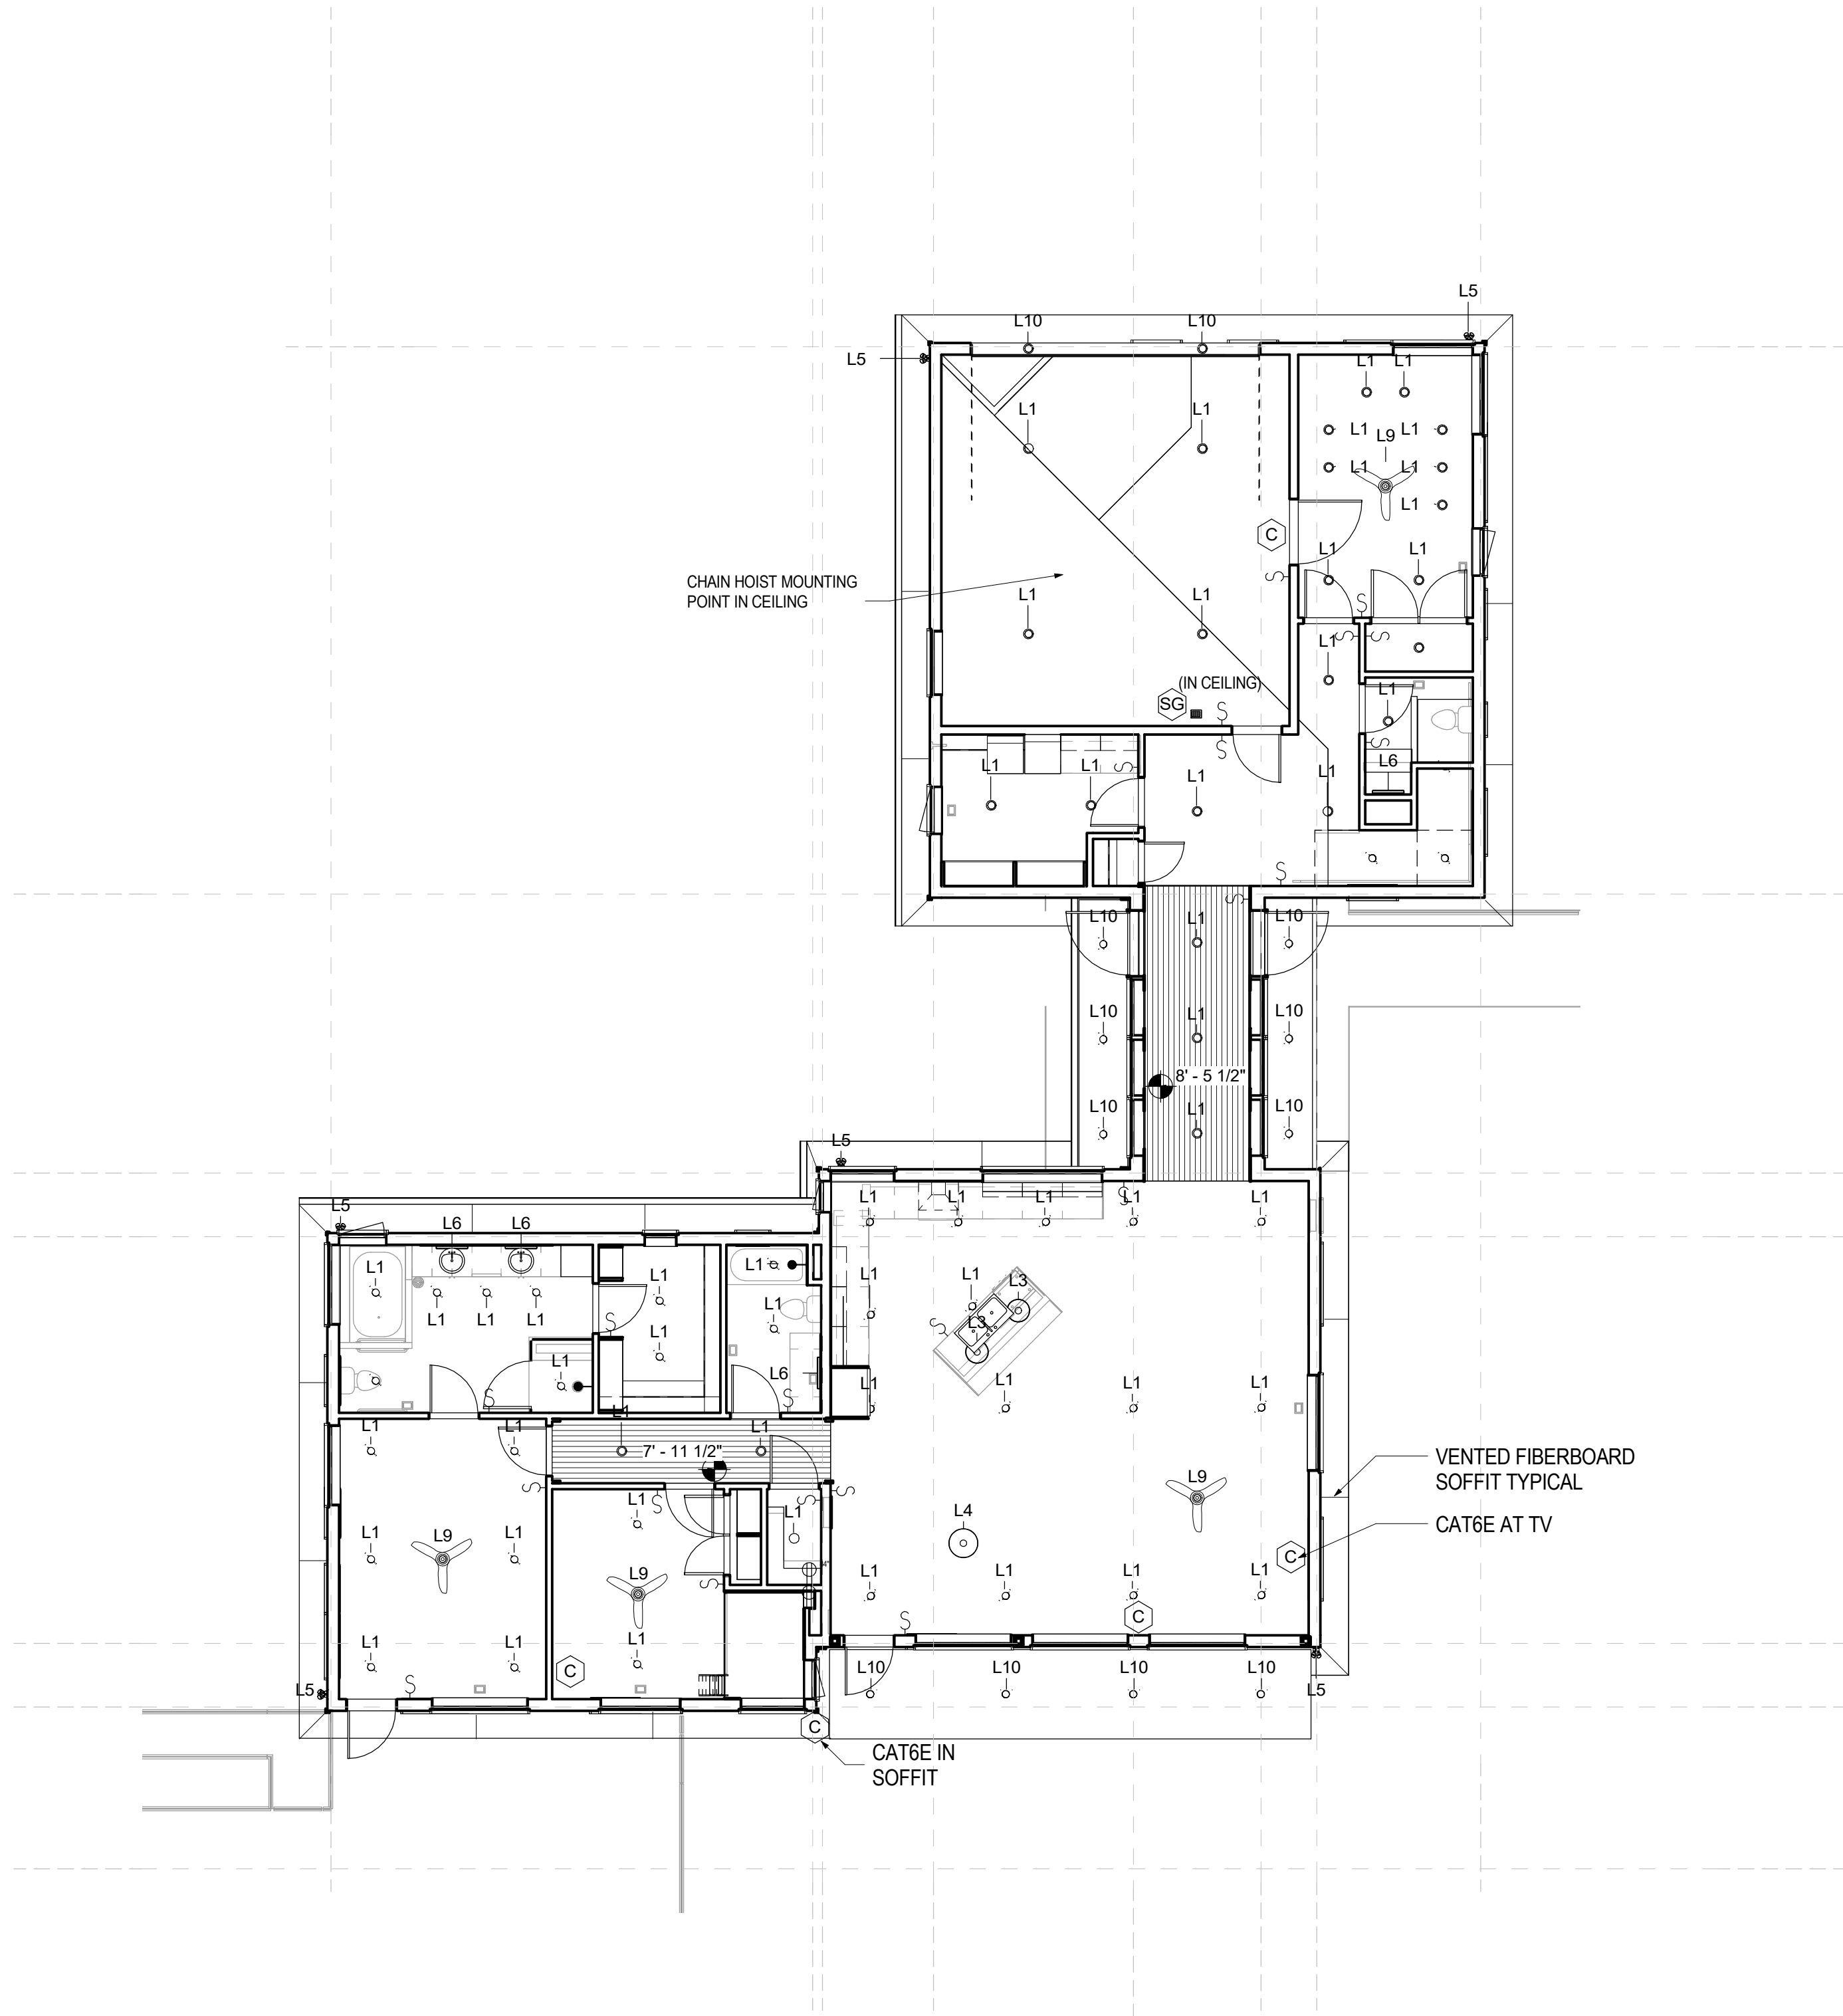

1
A6.01 REFLECTED CEILING PLAN, FIRST FLOOR
1/8" = 1'-0"

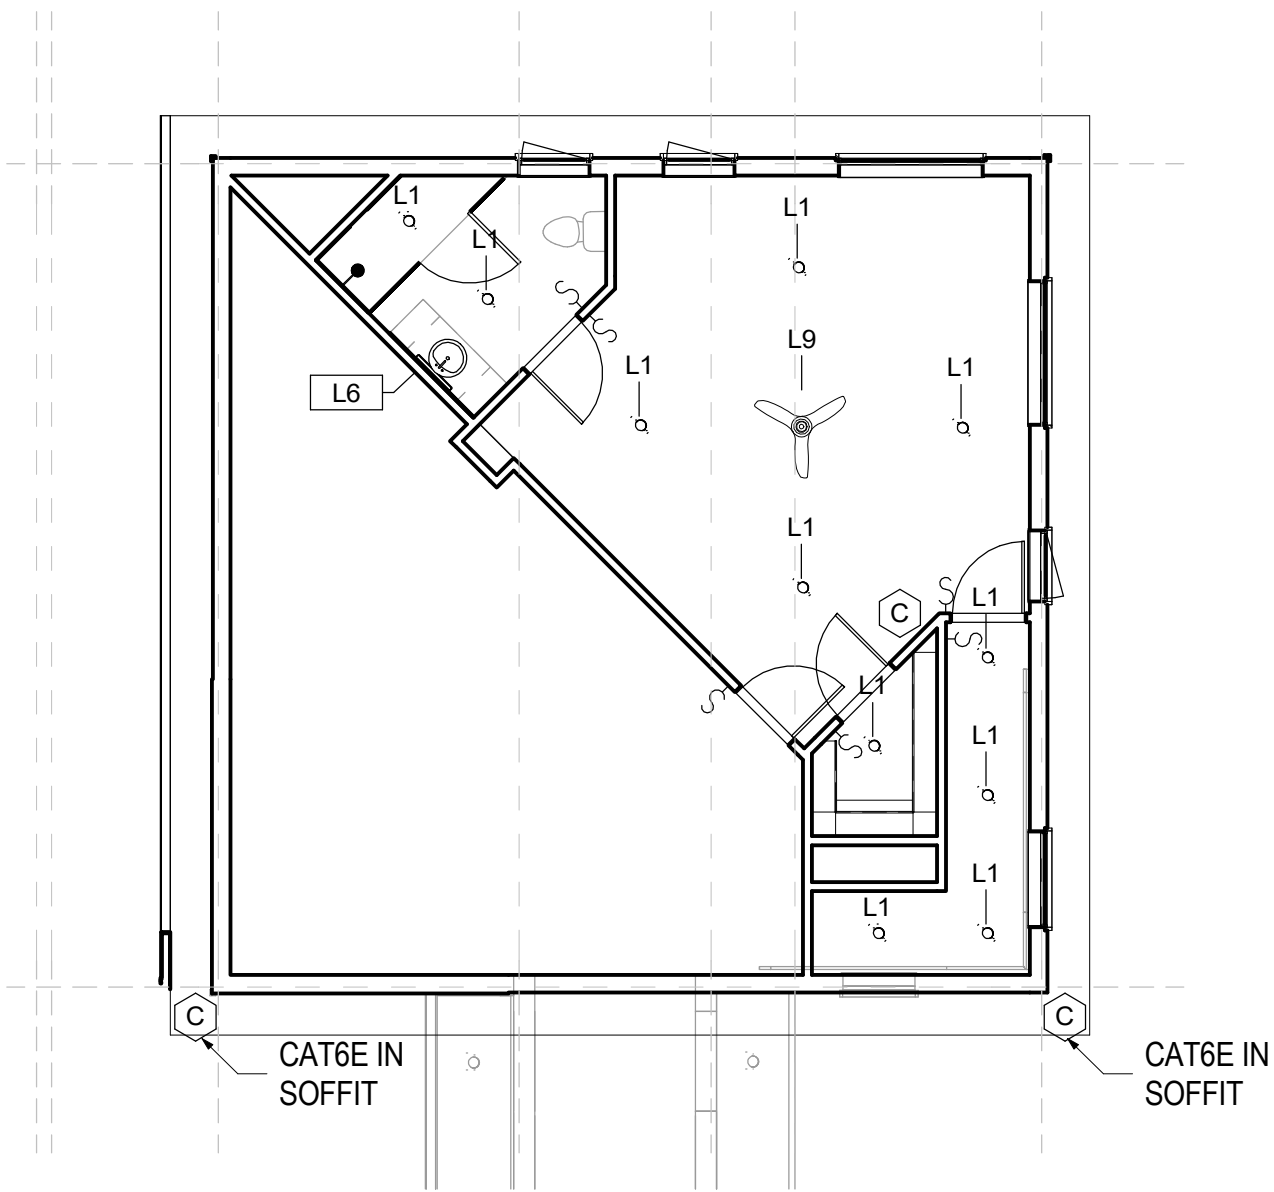


2
A6.01 REFLECTED CEILING PLAN, SECOND FLOOR
1/8" = 1'-0"

Lighting Fixture Schedule				
Type Mark	Description	Manufacturer	Model	Count
L1	6" Open Gimble Downlight	TBD		70
L3	Pendant Fixture	TBD		2
L4	Pendant Fixture	TBD		1
L5	Security Lighting	TBD		6
L6	Vanity Fixture	TBD		5
L7	Strip Lighting	TBD		2
L8	Step Light	TBD		12
L9	Ceiling Fan - No Light Fixture	TBD		5
L10	6" Open Downlight	TBD		12

NOTES

SEE ENLARGED PLANS (A2.01A,B, A5.01) FOR CASEMENT AND FLOOR LIGHTING


- CAT6E TO CEILING (MALE)
FROM PANEL ABOVE PANTRY (MALE, 84")
OR CLOSET PANEL AT LEVEL ONE OFFICE (MALE, 84")

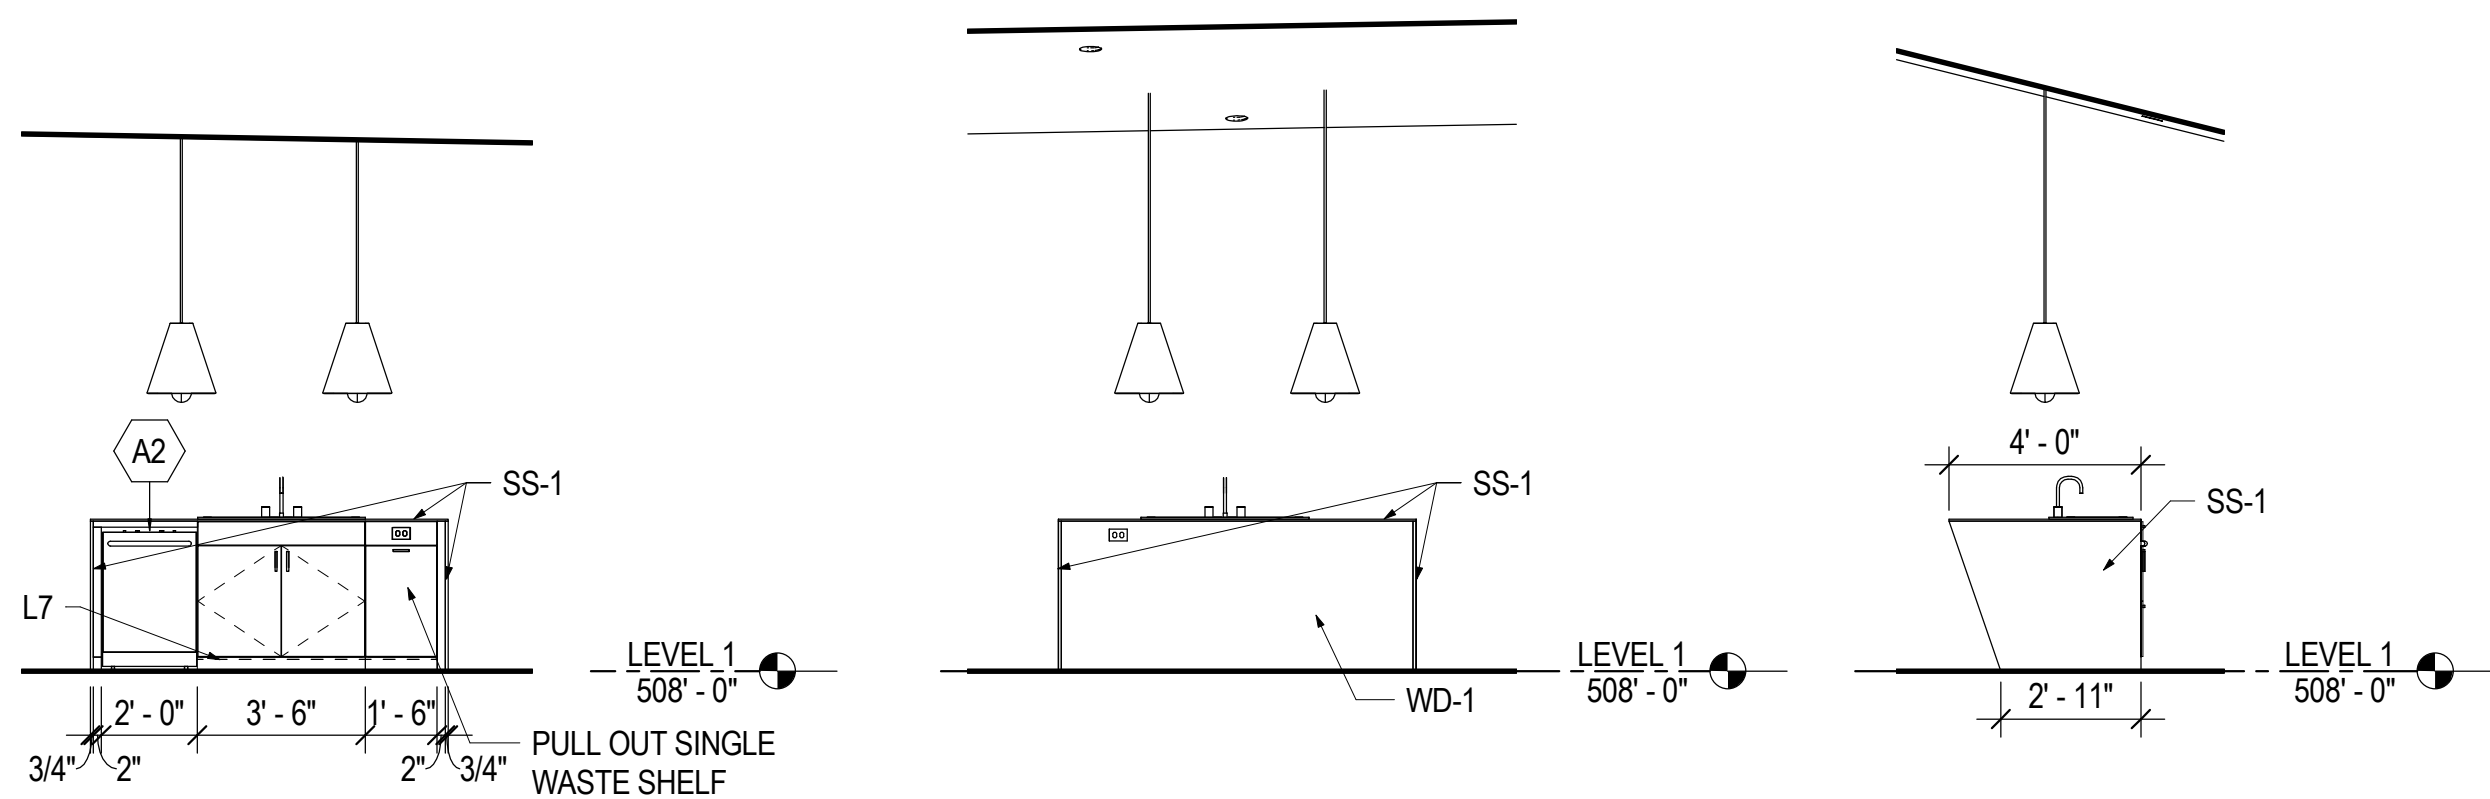


5 KITCHEN 04 - ISLAND EAST
A7.01 1/4" = 1'-0"

4 KITCHEN 04 - ISLAND WEST
A7.01 1/4" = 1'-0"


3 KITCHEN 04 - ISLAND SOUTH
A7.01 1/4" = 1'-0"

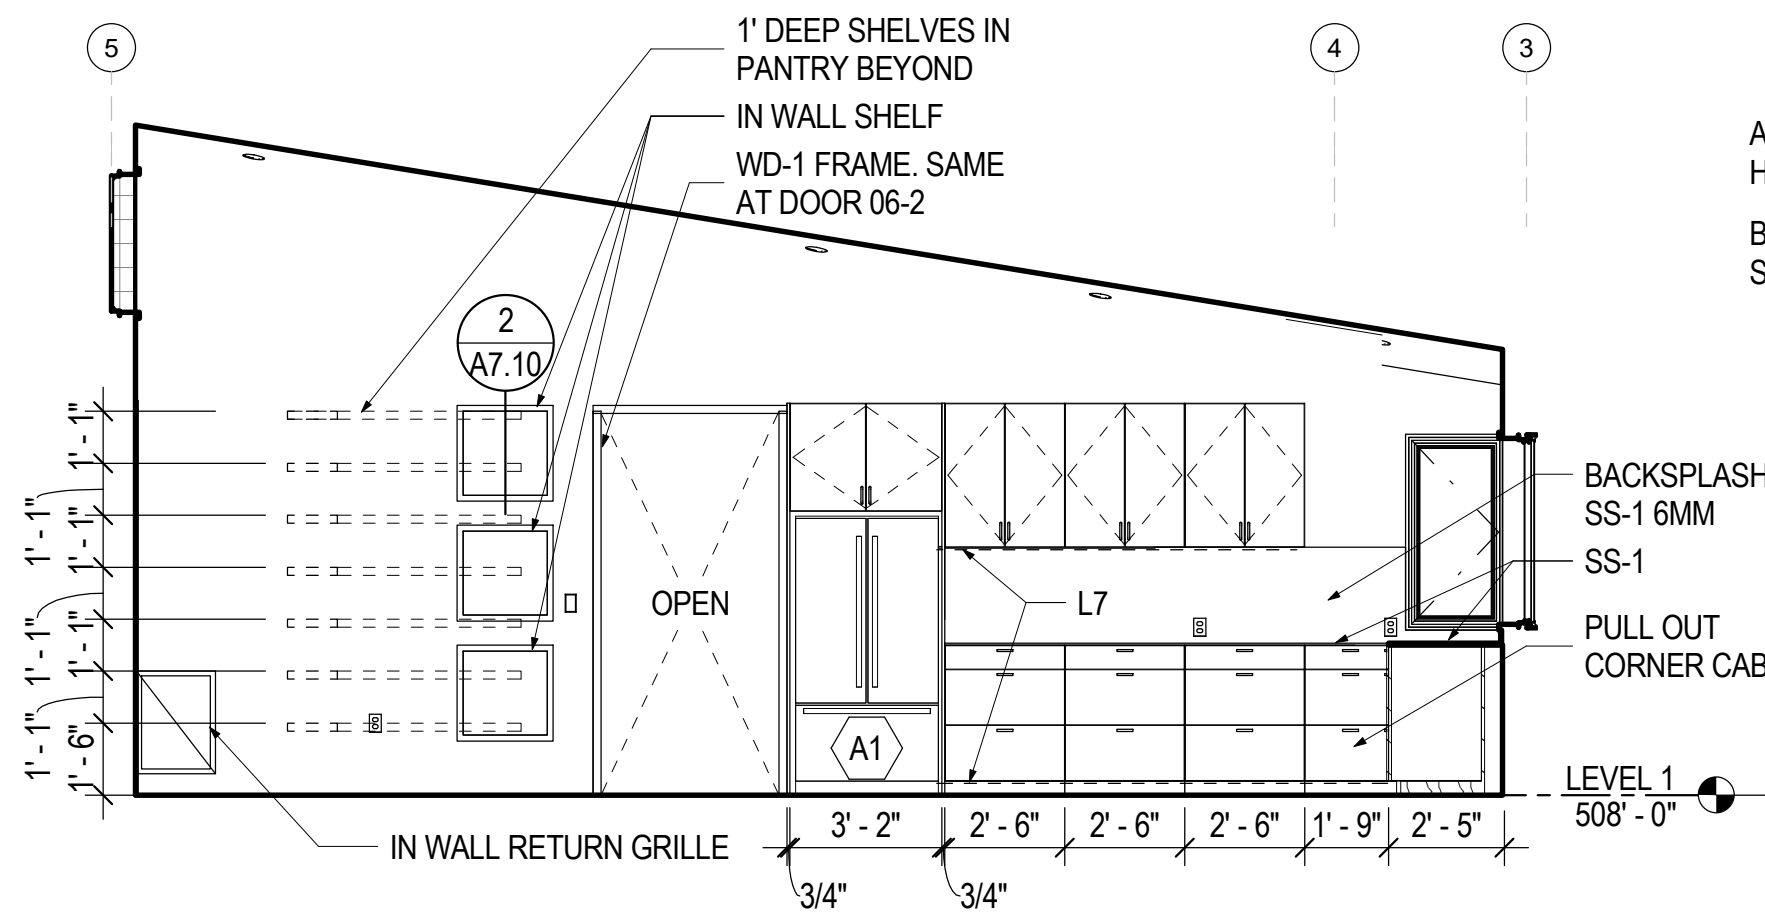


2 KITCHEN 04 - WEST
A7.01 1/4" = 1'-0"

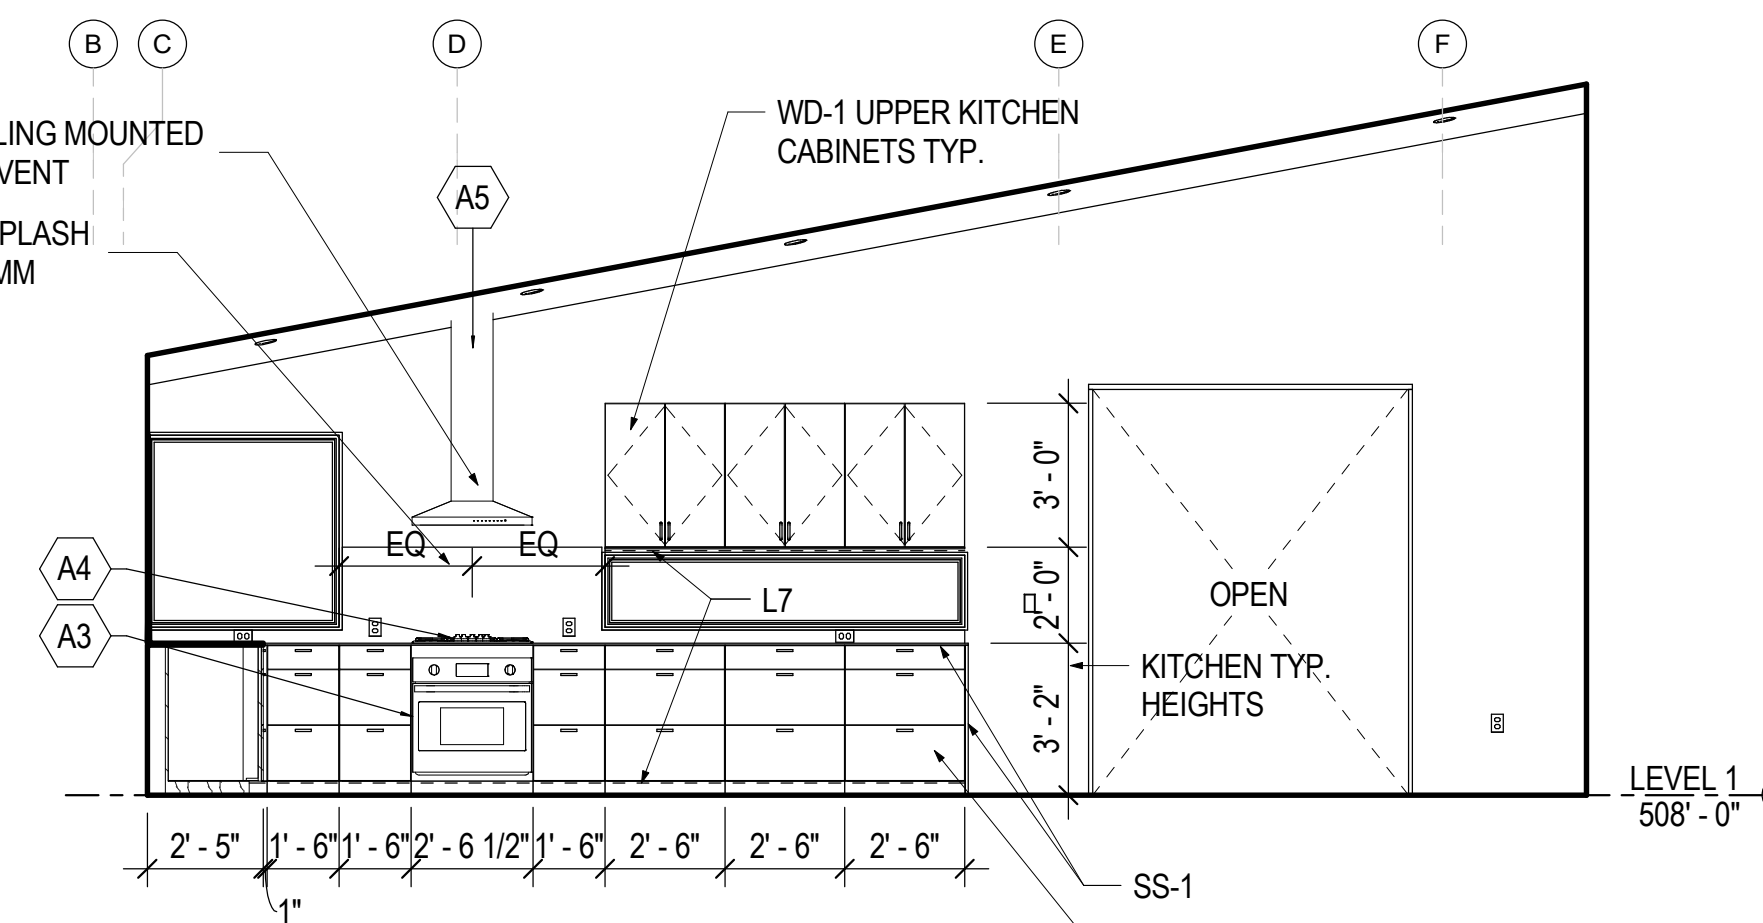


1 KITCHEN 04 - NORTH
A7.01 1/4" = 1'-0"

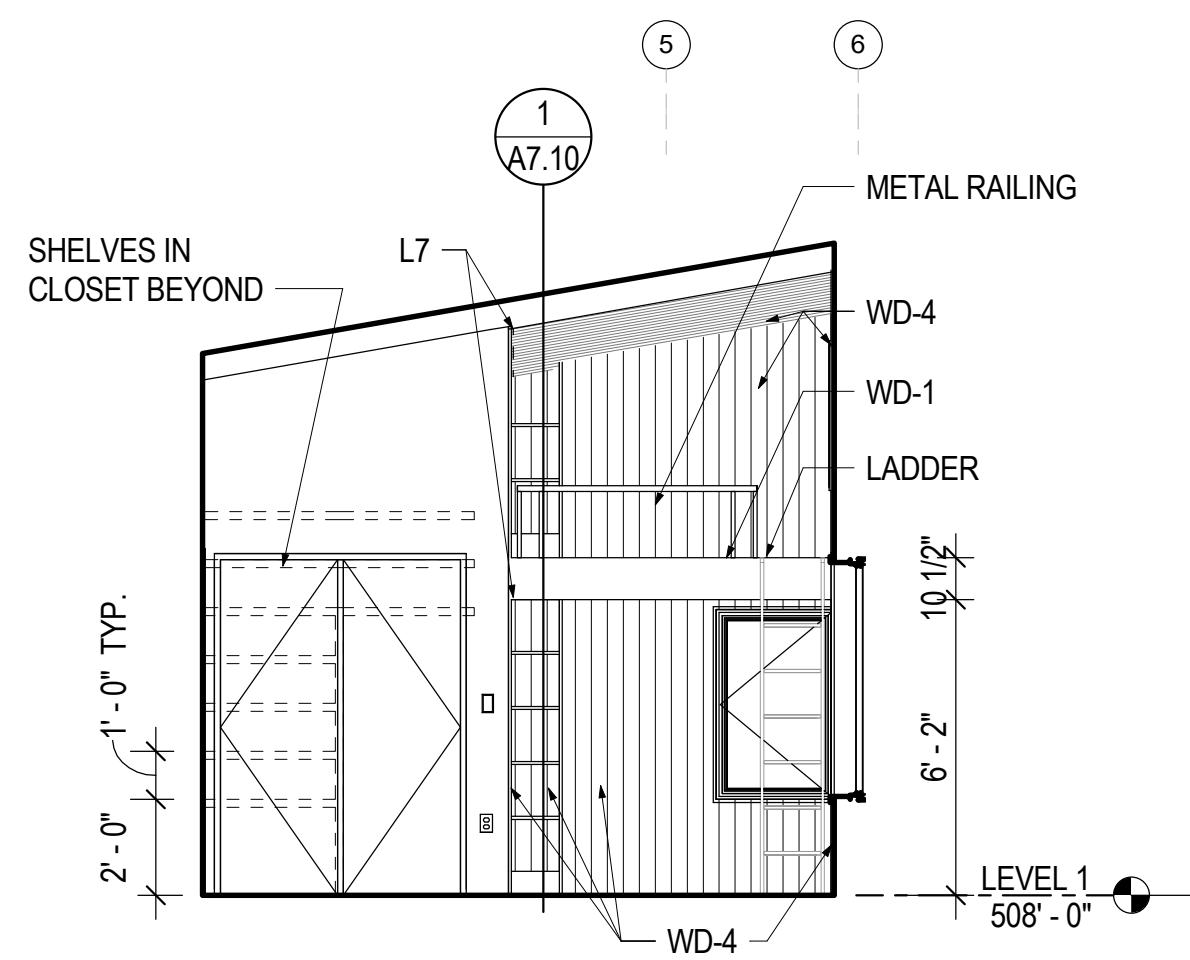


9 SECOND BEDROOM 09 - EAST
A7.01 1/4" = 1'-0"

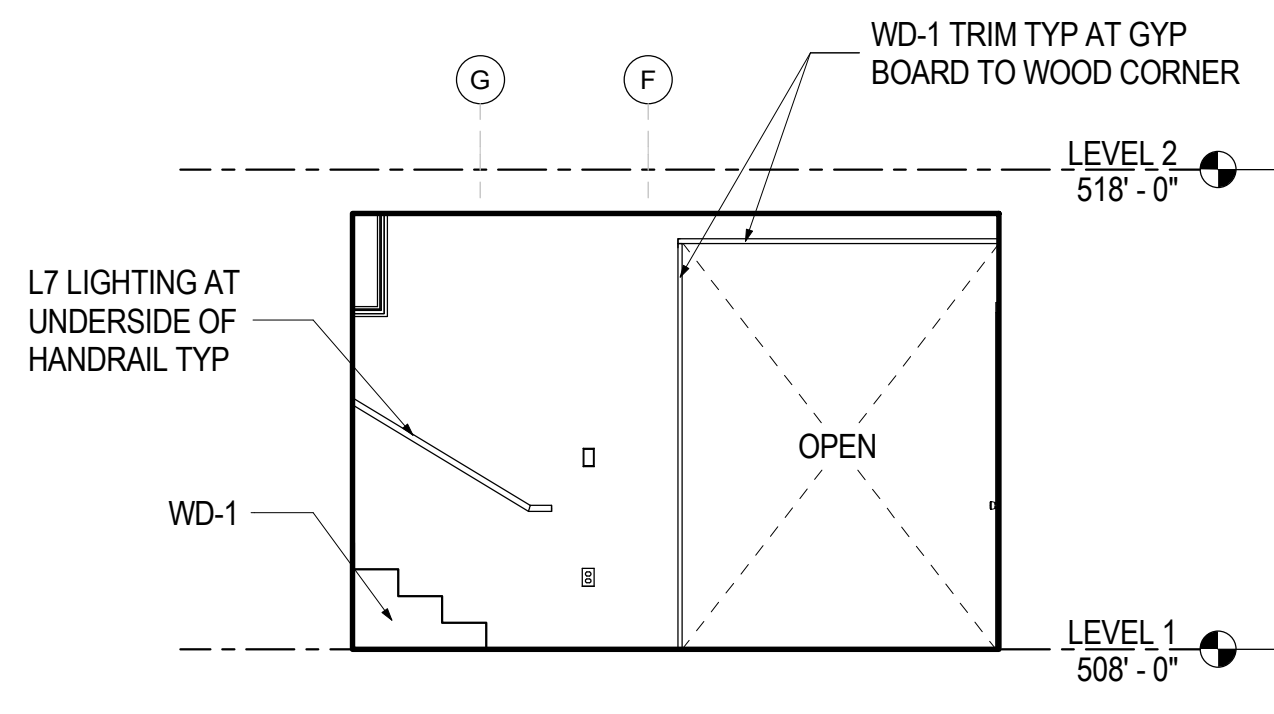


8 NORTH HALLWAY 16 - SOUTH
A7.01 1/4" = 1'-0"

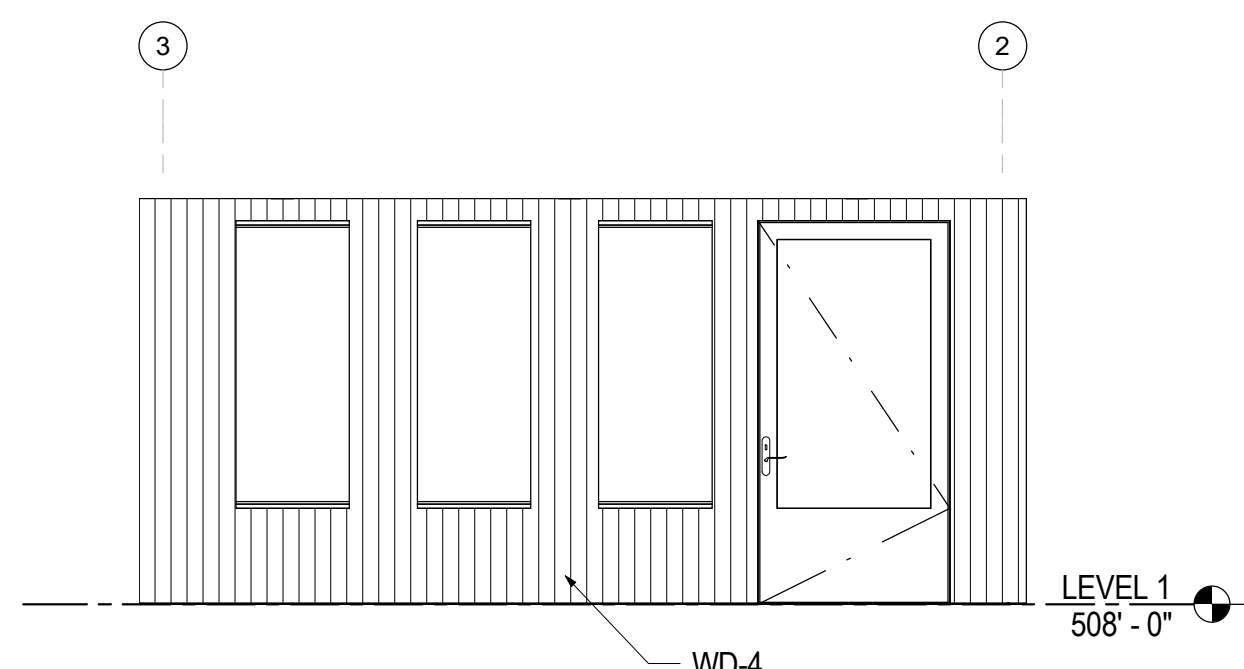


7 ENTRY HALL 01 - WEST
A7.01 1/4" = 1'-0"

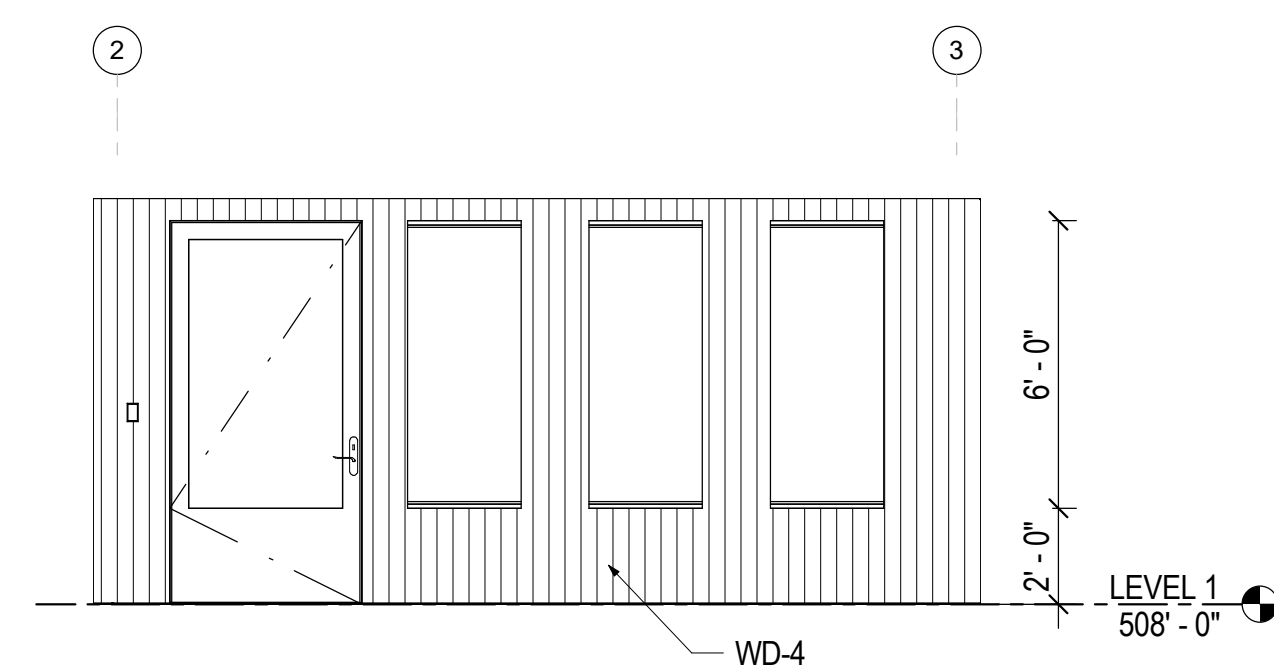


6 ENTRY HALL 01 - EAST
A7.01 1/4" = 1'-0"

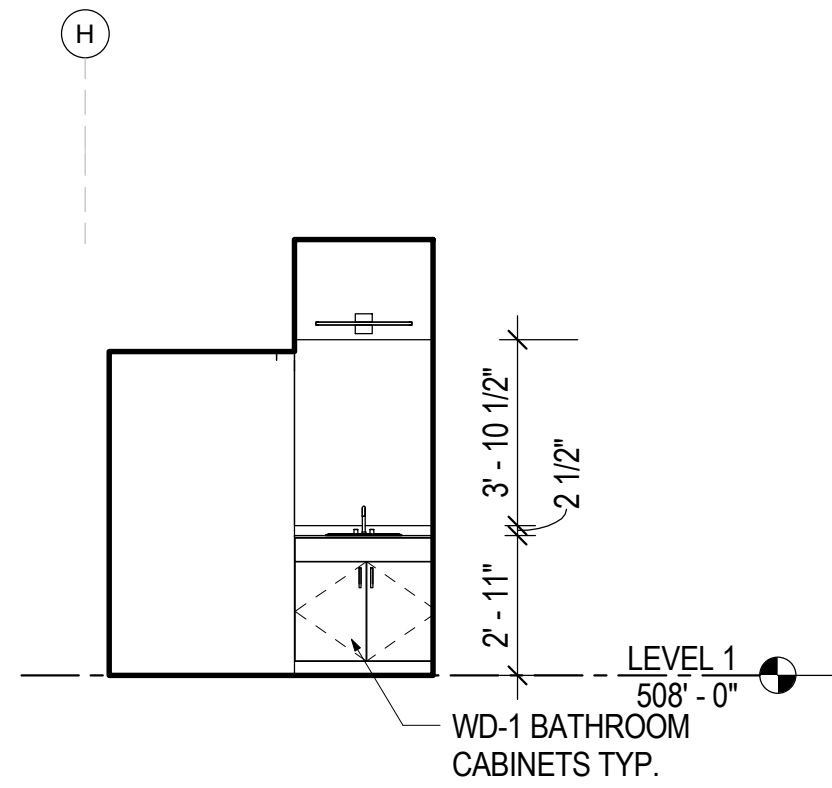


4
A7.02 **POWDER ROOM 14 - SOUTH**
1/4" = 1'-0"

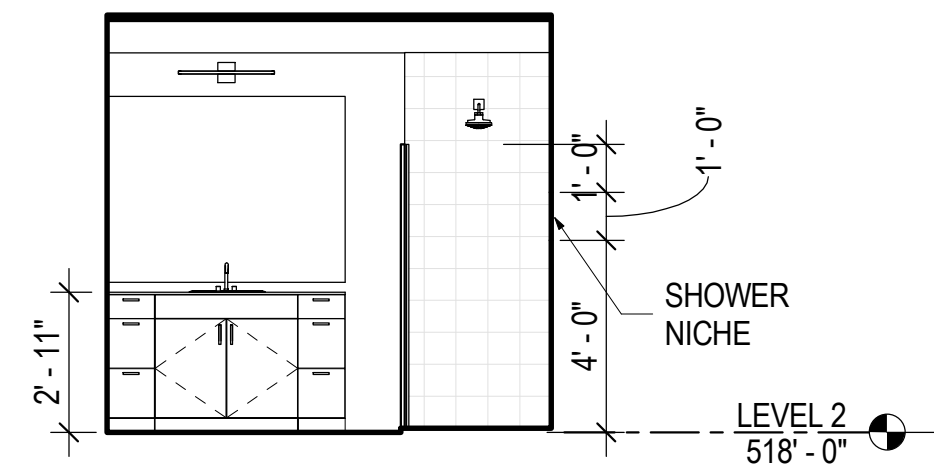


5
A7.02 **GUEST BATHROOM 19 - SOUTH**
1/4" = 1'-0"

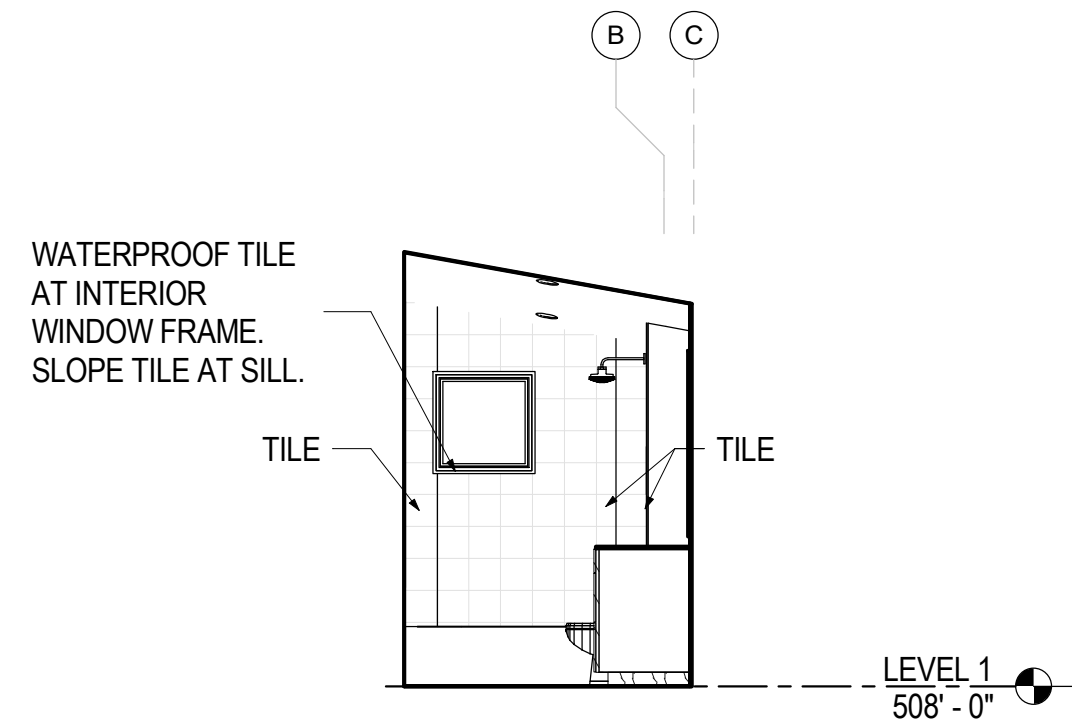


3
A7.02 **BATHROOM 11 - NORTH**
1/4" = 1'-0"

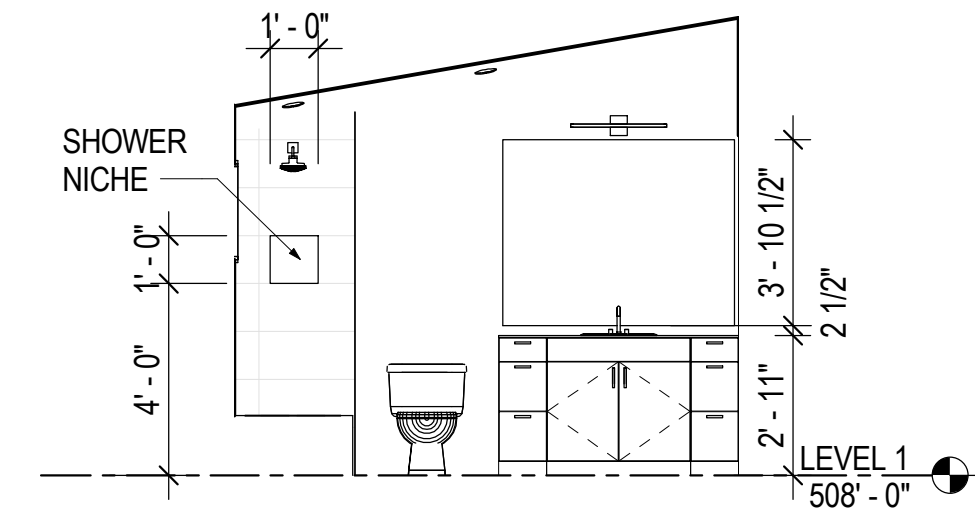


2
A7.02 **BATHROOM 11 - EAST**
1/4" = 1'-0"

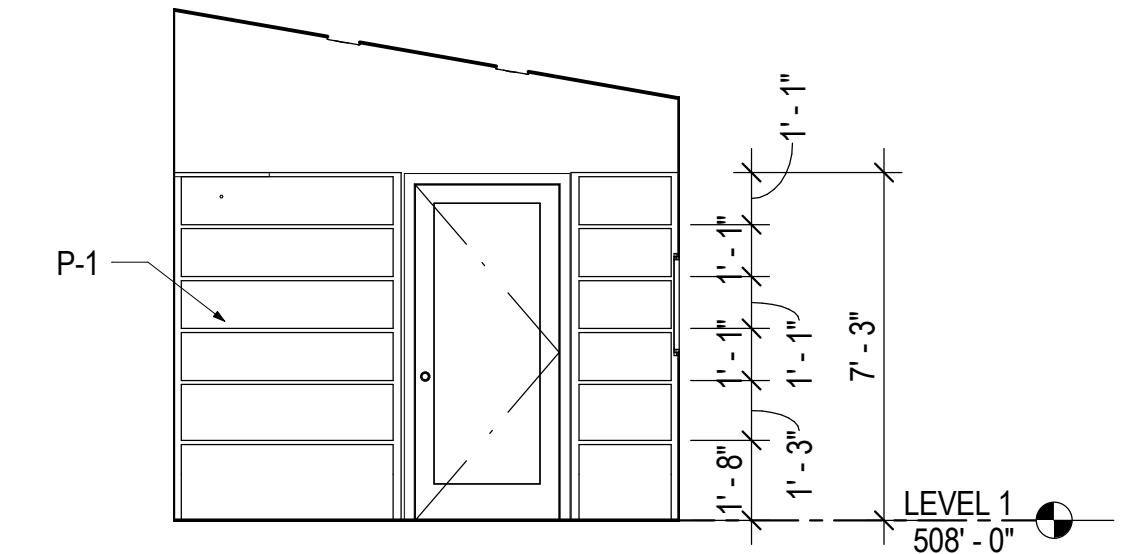


1
A7.02 **MASTER CLOSET 08 - WEST**
1/4" = 1'-0"

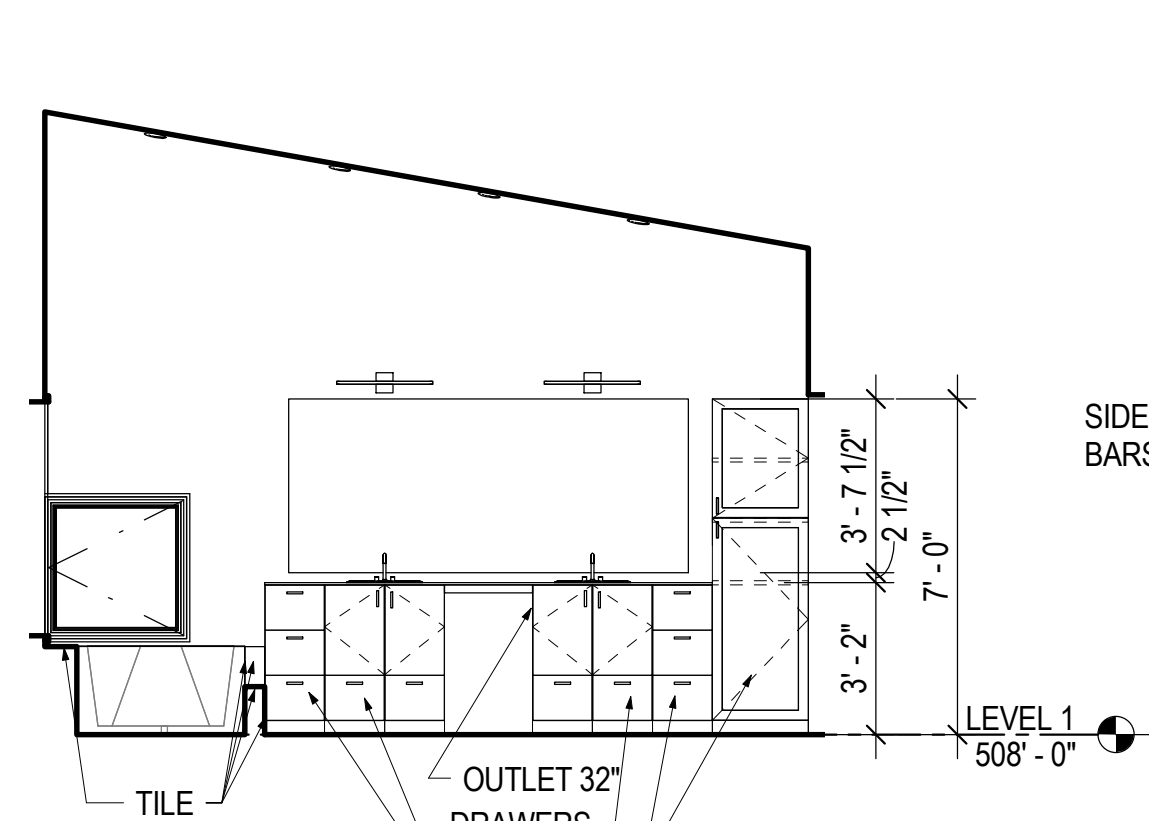


10
A7.02 **MASTER BATHROOM 07 - NORTH**
1/4" = 1'-0"

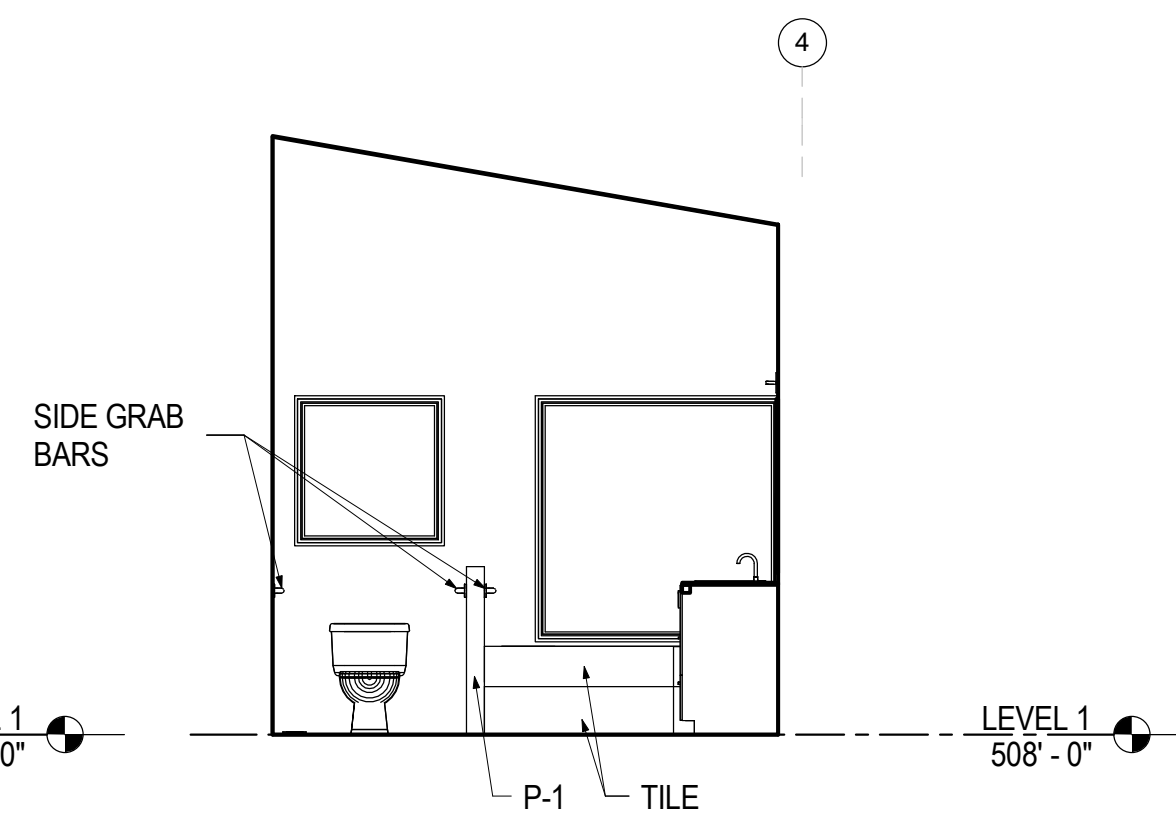


9
A7.02 **MASTER BATHROOM 07 - WEST**
1/4" = 1'-0"

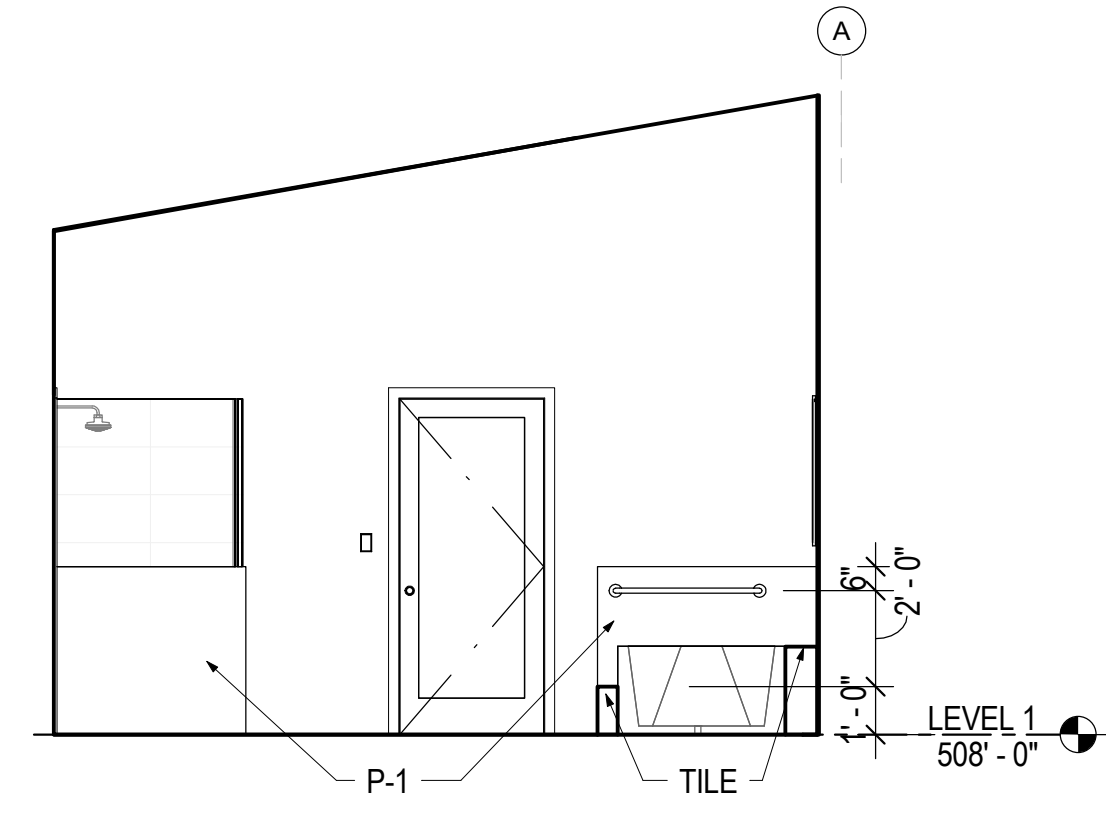


8
A7.02 **MASTER BATHROOM 07 - SOUTH**
1/4" = 1'-0"

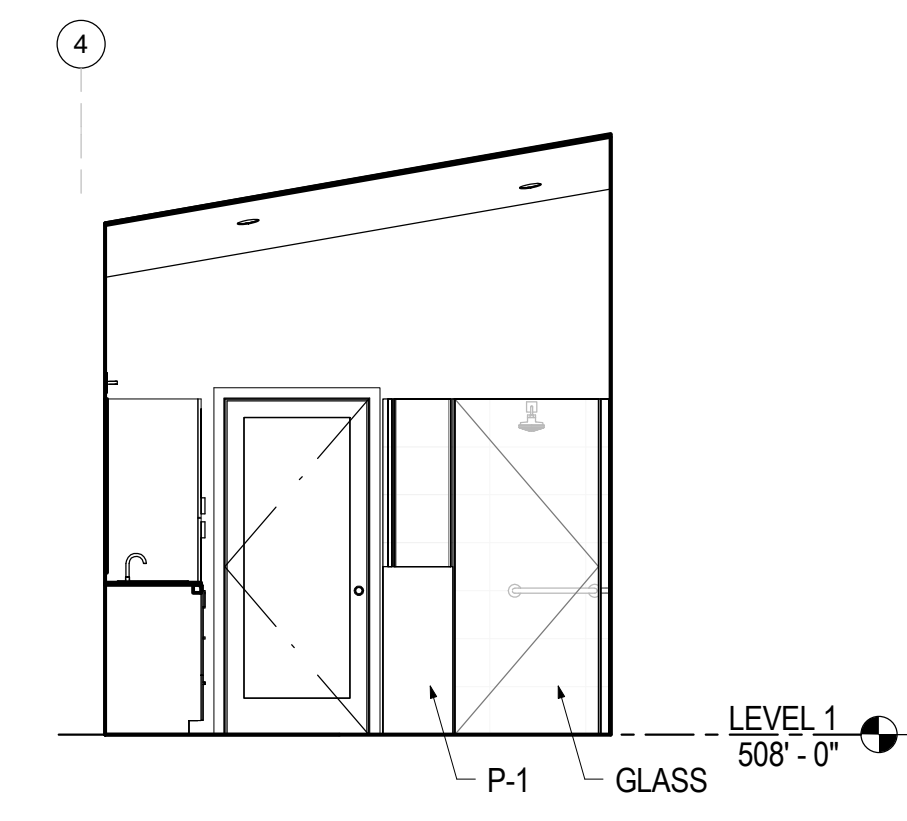


7
A7.02 **MASTER BATHROOM 07 - EAST**
1/4" = 1'-0"

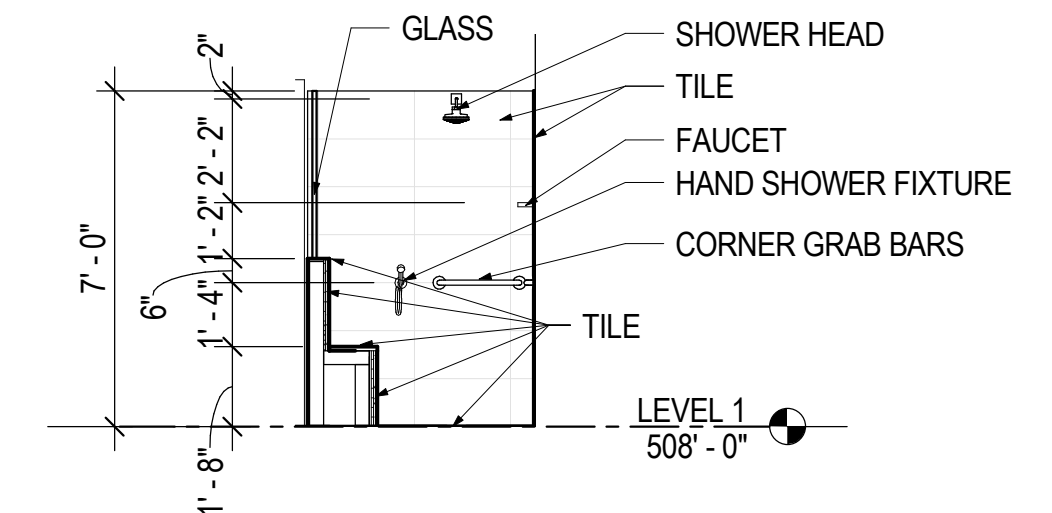


6
A7.02 **MASTER BATHROOM 07 - SHOWER EAST**
1/4" = 1'-0"

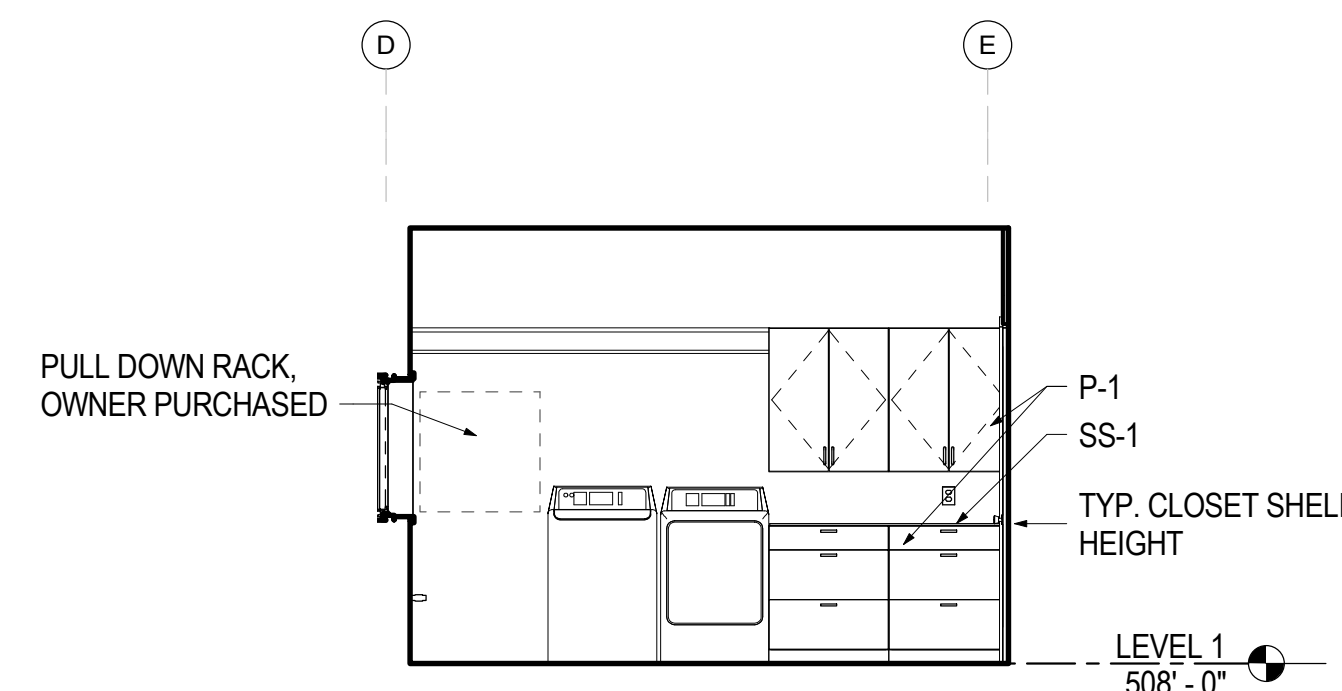


13
A7.02 **LAUNDRY ROOM 12 - NORTH**
1/4" = 1'-0"

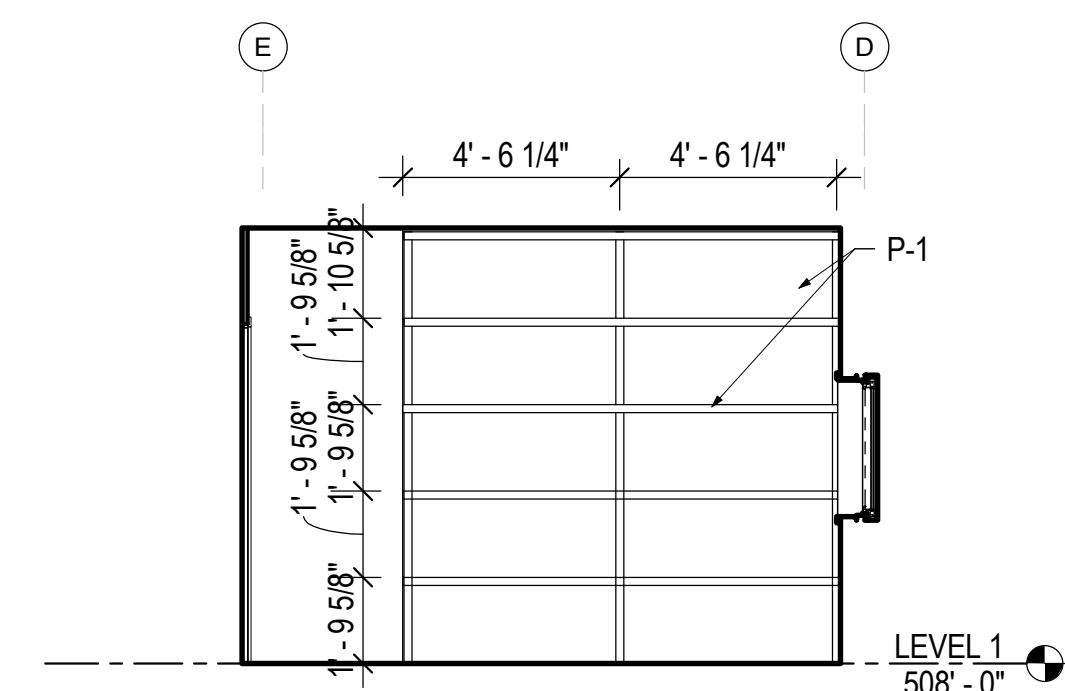


12
A7.02 **LAUNDRY ROOM 12 - SOUTH**
1/4" = 1'-0"

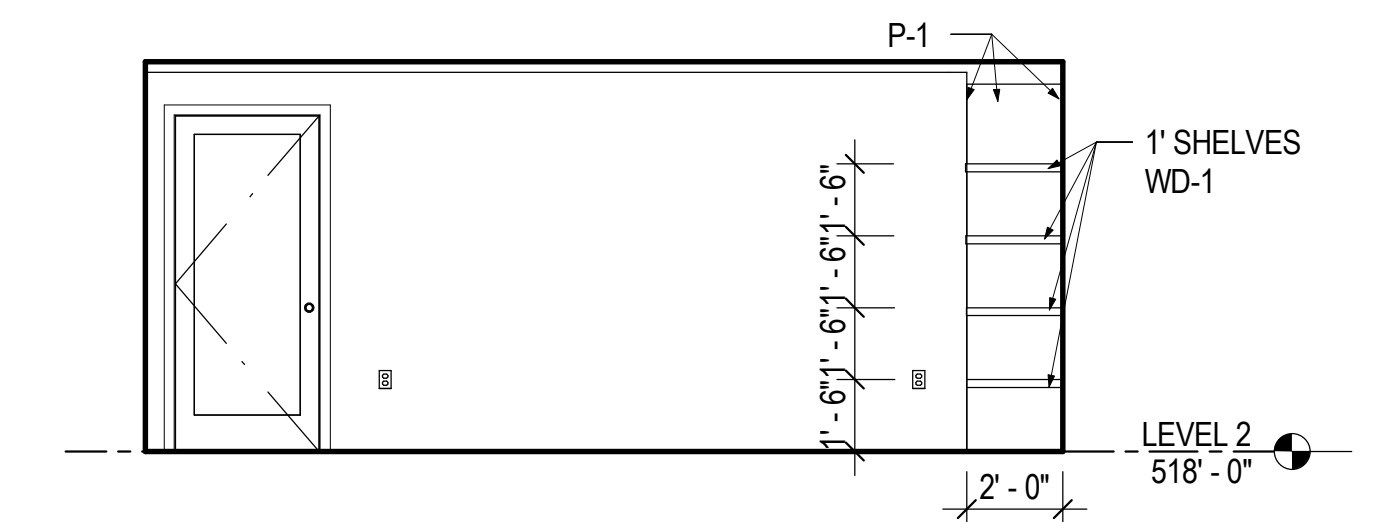


11
A7.02 **GUEST BEDROOM 17 - WEST**
1/4" = 1'-0"

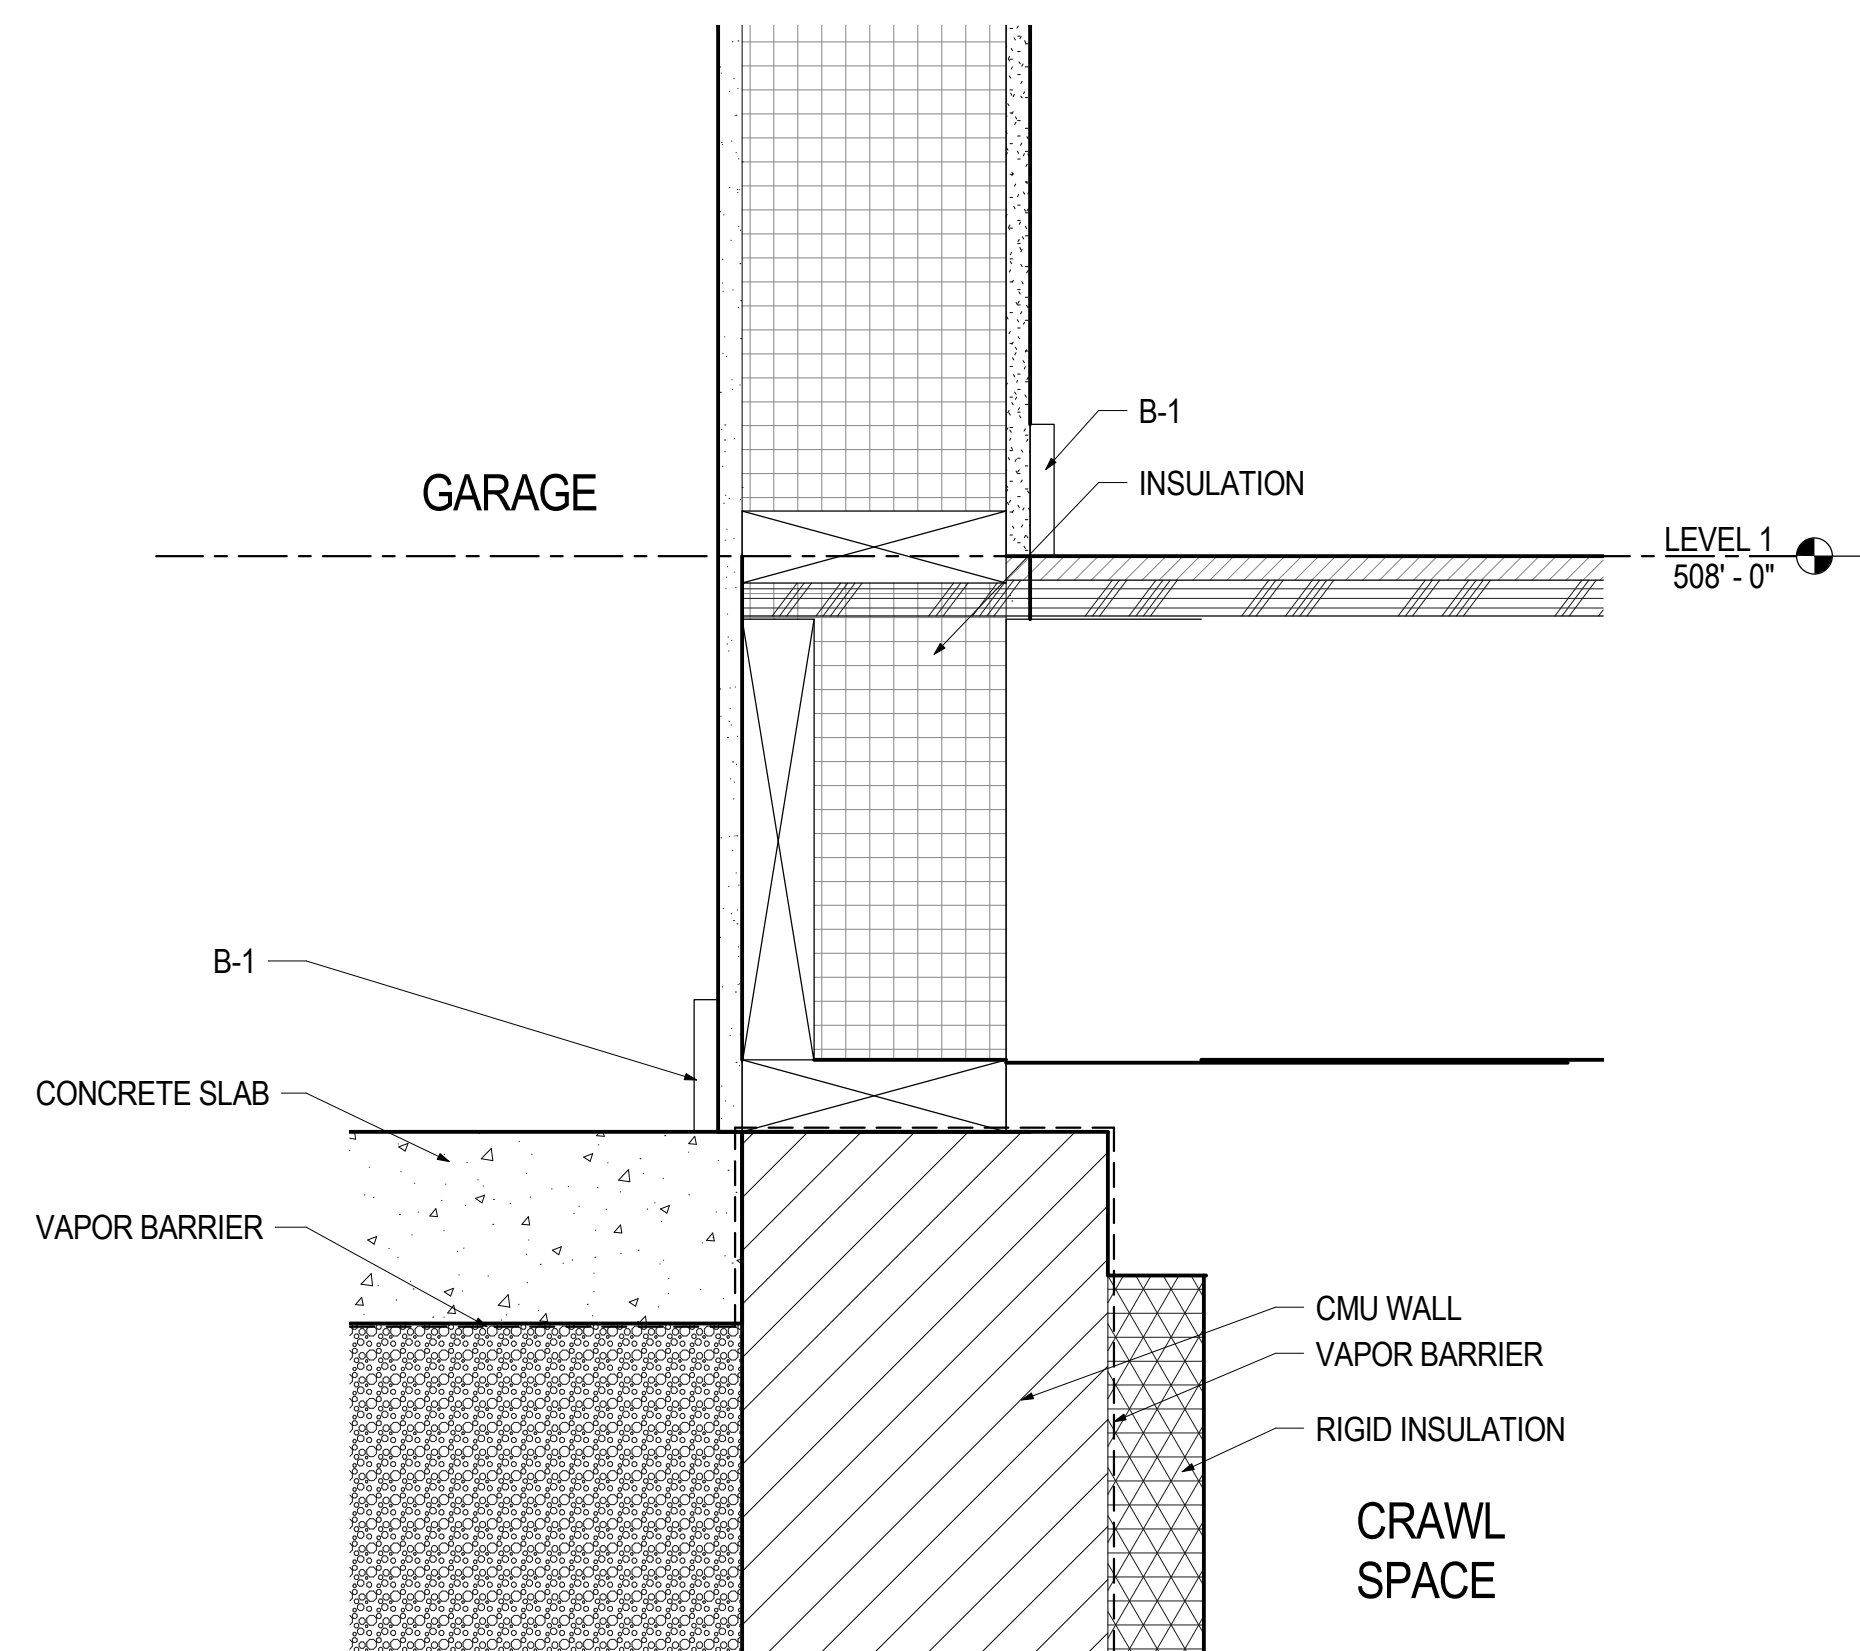

3
A7.10
BASE, GARAGE, INTERIOR
3" = 1'-0"

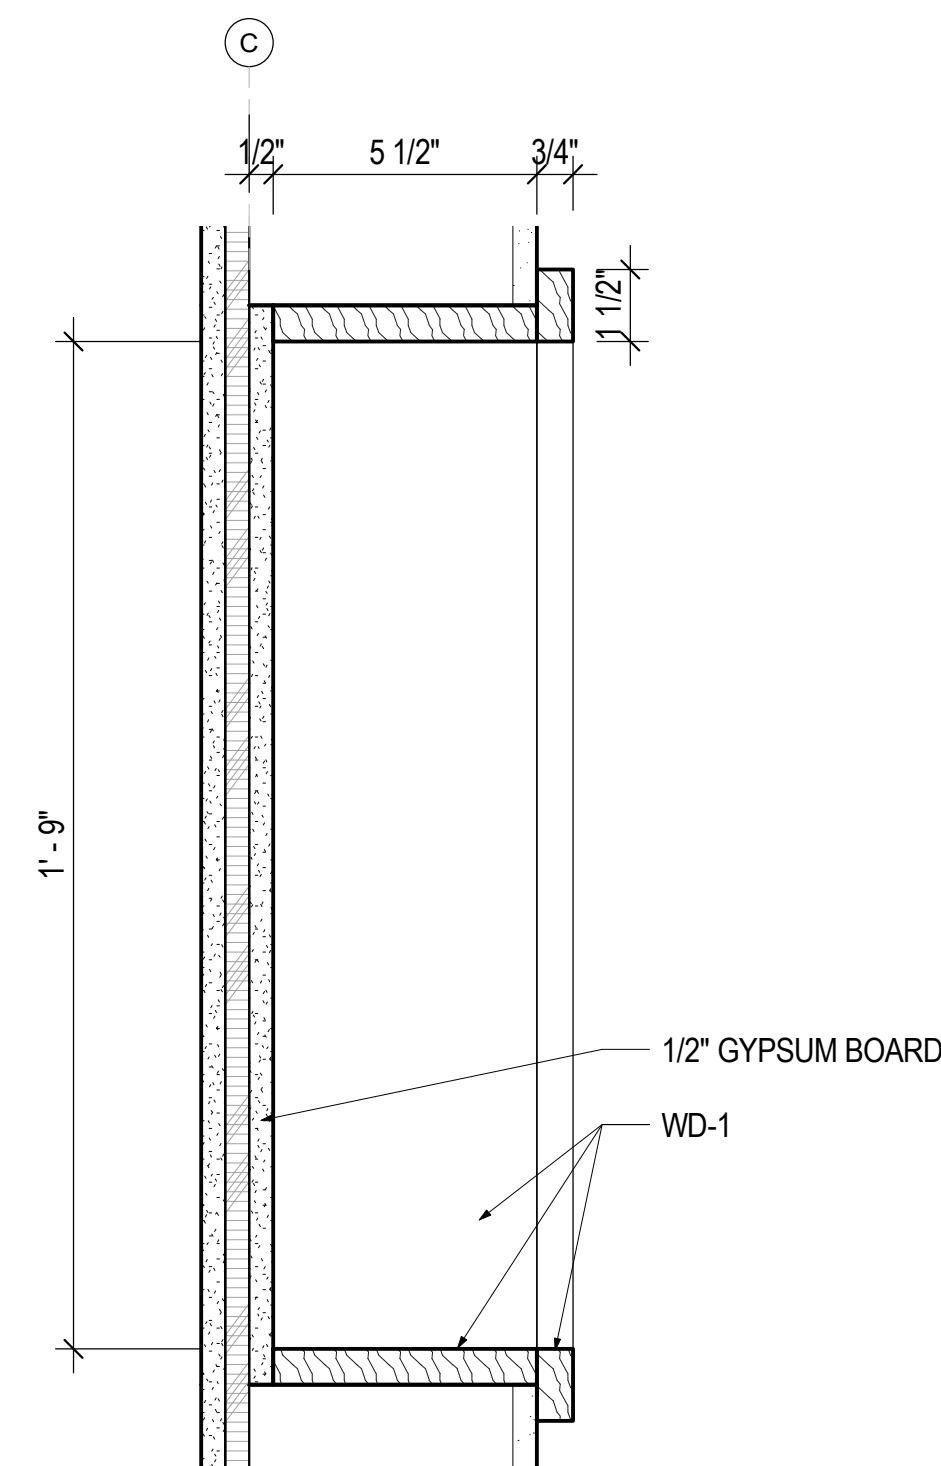

2
A7.10
SECTION, W-2 WALL SHELF, INTERIOR
3" = 1'-0"

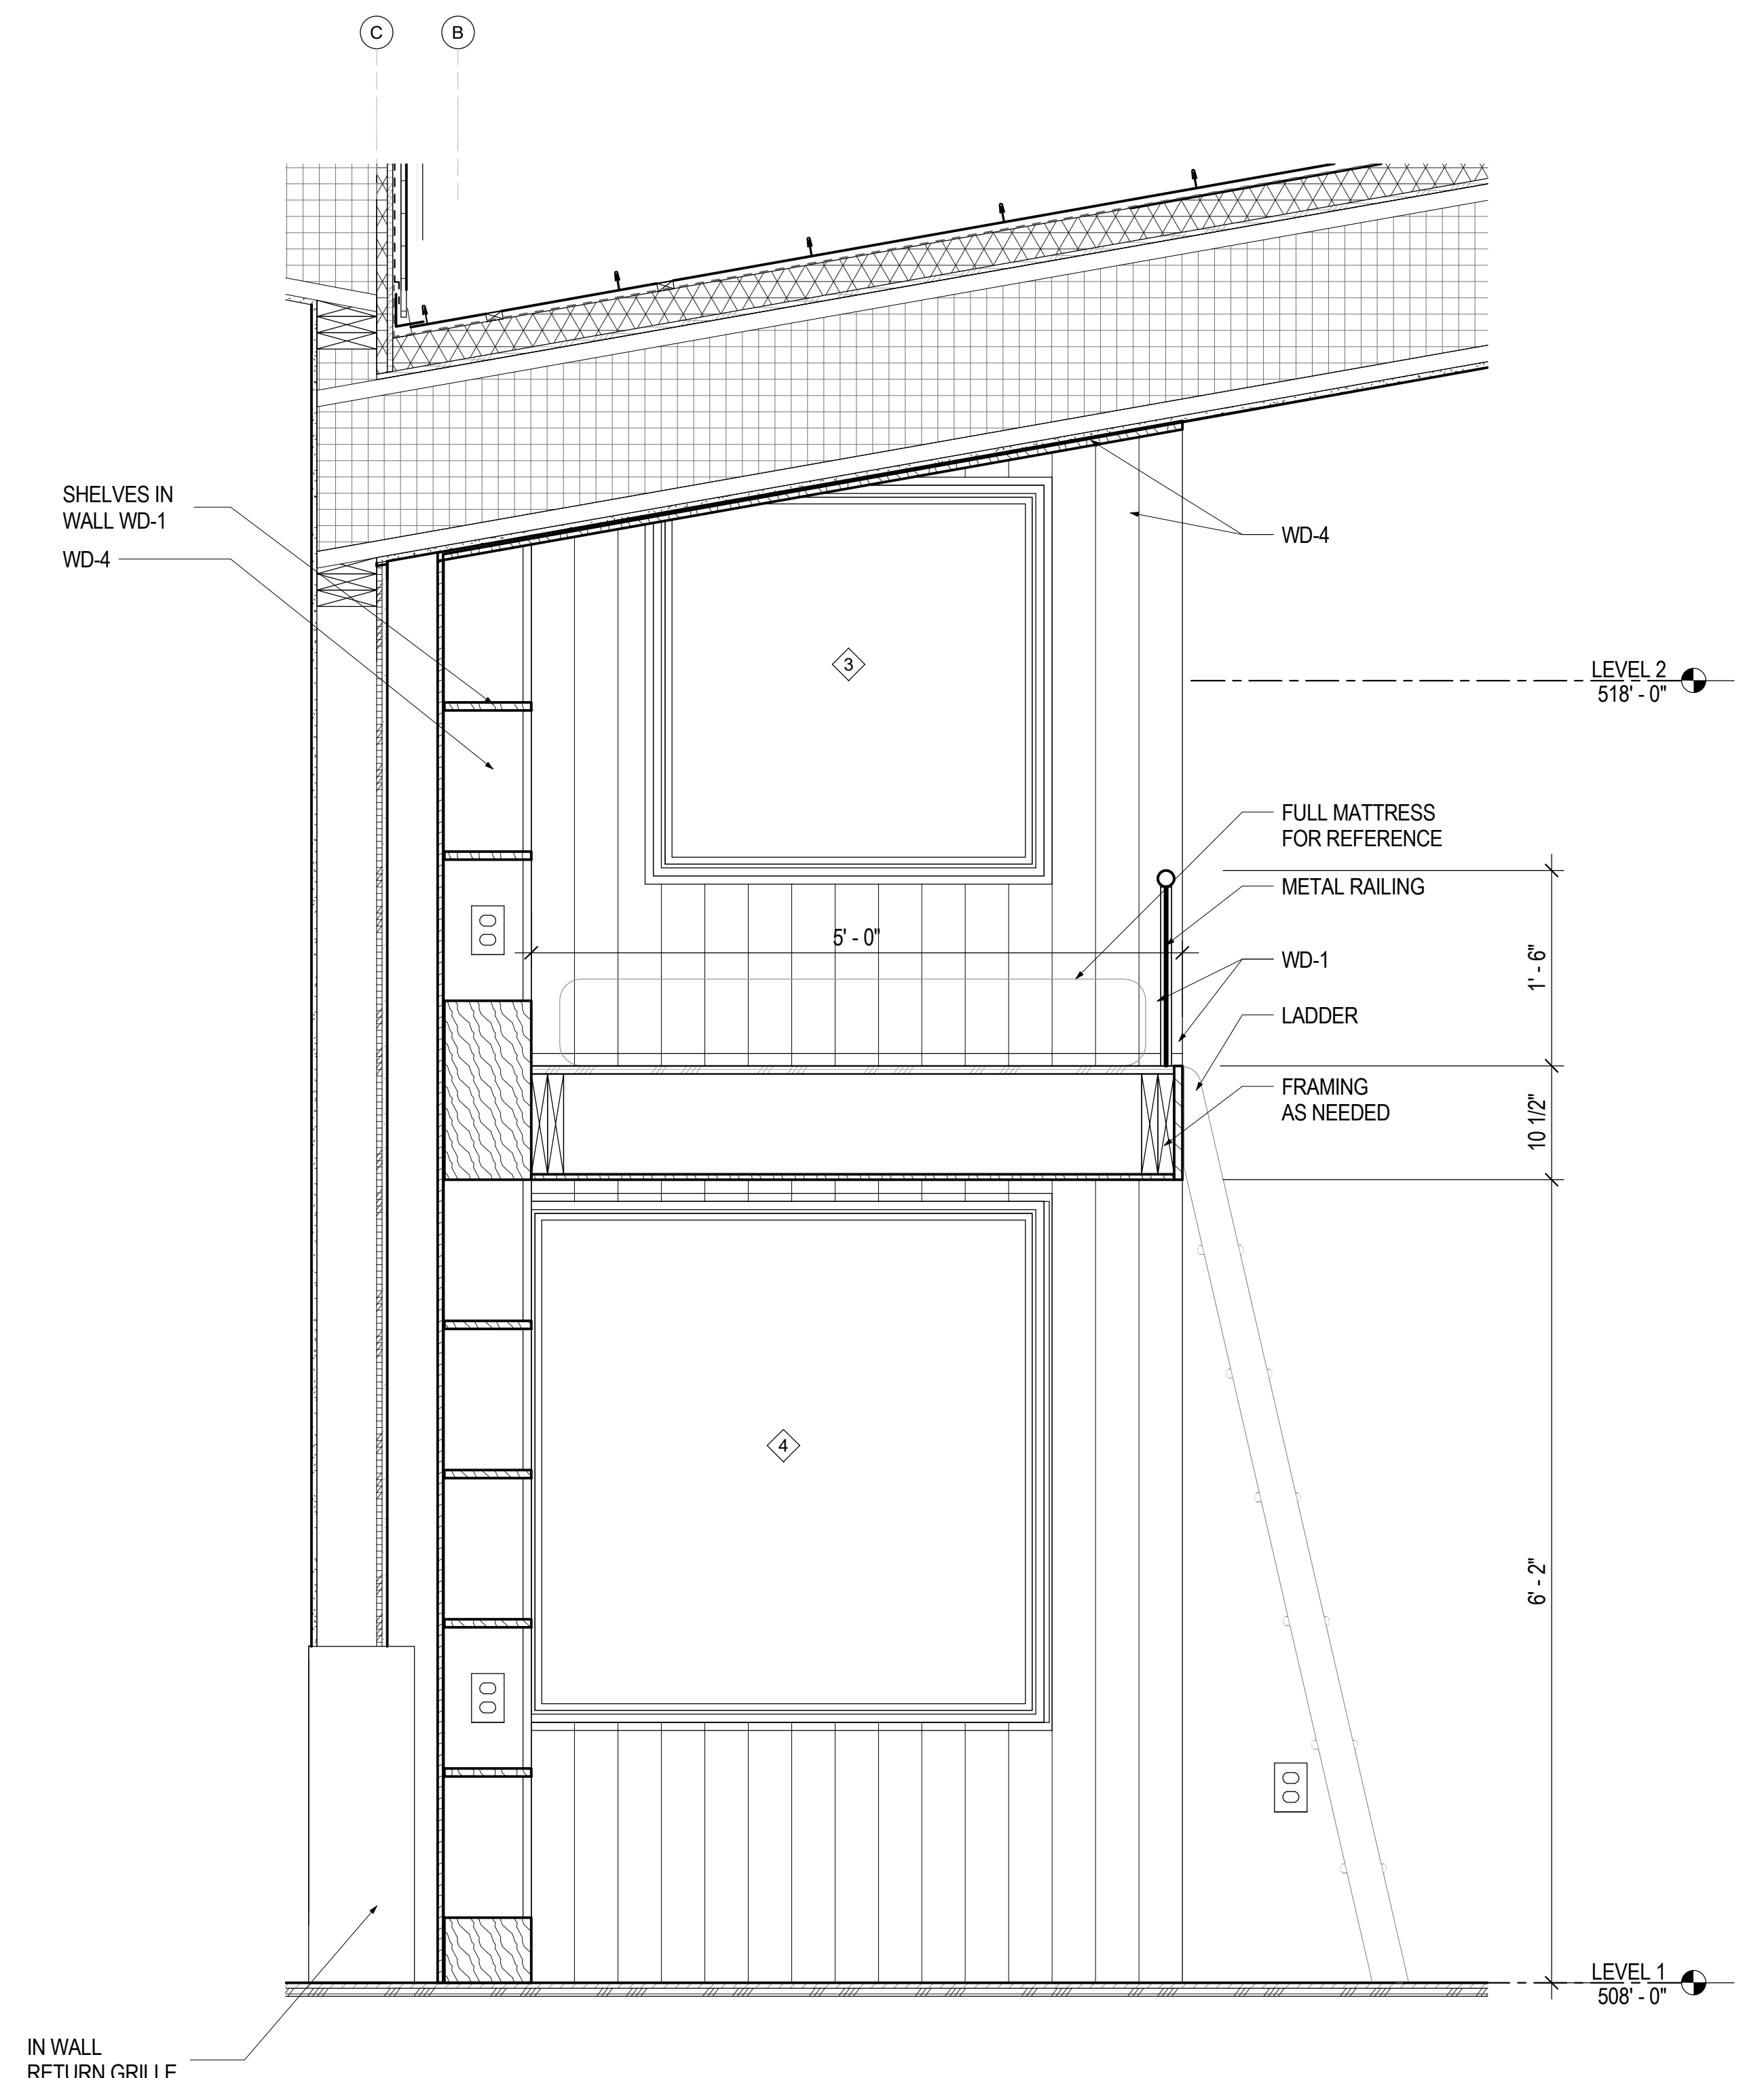

1
A7.10
SECTION, READING NOOK
1" = 1'-0"

WINDOW SCHEDULE										
WINDOW TAG	COUNT	NOMINAL WIDTH	NOMINAL HEIGHT	WINDOW TYPE	TYPE	INTERIOR MATERIAL	CLADDING MATERIAL	INTERIOR FRAME	EXTERIOR FRAME	COMMENTS
2	2	2' - 0"	2' - 0"	FIXED	ESDG2020	Ultrex-Marvin-Stonewhite	Ultrex-Marvin-Stonewhite	WD-1	WD-2	
2C	2	2' - 0"	2' - 0"	CASEMENT	ESCA2020	Ultrex-Marvin-Stonewhite	Ultrex-Marvin-Stonewhite	WD-1	WD-2	
3	6	3' - 0"	3' - 0"	FIXED	ESDG3030	Ultrex-Marvin-Stonewhite	Ultrex-Marvin-Stonewhite	WD-1	WD-2	
3C	7	3' - 0"	3' - 0"	CASEMENT	ESCA3030	Ultrex-Marvin-Stonewhite	Ultrex-Marvin-Stonewhite	WD-1	WD-2	
4	8	4' - 0"	4' - 0"	FIXED	ESDG4040	Ultrex-Marvin-Stonewhite	Ultrex-Marvin-Stonewhite	WD-1	WD-2	
5	8	5' - 0"	5' - 0"	FIXED	ESDG5050	Ultrex-Marvin-Stonewhite	Ultrex-Marvin-Stonewhite	WD-1	WD-2	
6	8	6' - 0"	6' - 0"	FIXED	ESDG6060	Ultrex-Marvin-Stonewhite	Ultrex-Marvin-Stonewhite	WD-1	WD-2	
7C	1	2' - 0"	4' - 0"	CASEMENT	ESCA2040	Ultrex-Marvin-Stonewhite	Ultrex-Marvin-Stonewhite	WD-1	WD-2	
8C	1	2' - 6"	4' - 0"	CASEMENT	ESCA2640	Ultrex-Marvin-Stonewhite	Ultrex-Marvin-Stonewhite	WD-1	WD-2	
9	6	3' - 6"	6' - 0"	FIXED	ESDG3660	Ultrex-Marvin-Stonewhite	Ultrex-Marvin-Stonewhite	WD-1	WD-2	
10	1	7' - 6"	1' - 6"	FIXED	ESDG7616	Ultrex-Marvin-Stonewhite	Ultrex-Marvin-Stonewhite	WD-1	WD-2	

DOOR SCHEDULE							
DOOR NUMBER	FUNCTION	WIDTH	HEIGHT	DOOR MATERIAL	FRAME MATERIAL	FINISH	HARDWARE

01-1	Exterior	4' - 0"	8' - 0"	WOOD, GLASS	WOOD	STAINED	
01-2	Exterior	4' - 0"	8' - 0"	WOOD, GLASS	WOOD	STAINED	
03-1	Exterior	3' - 0"	8' - 0"	METAL	WOOD	STAINED	
05-1	Interior	3' - 0"	7' - 0"	WOOD (SOLID-CORE)	WOOD	PAINTED	
06-1	Exterior	3' - 0"	8' - 0"	WOOD, GLASS	WOOD	STAINED	
06-2	Interior	3' - 0"	7' - 0"	WOOD RAIL & STILE + FROSTED GLASS PANEL	WOOD	PAINTED	
07-1	Interior	3' - 0"	7' - 0"	WOOD (SOLID-CORE)	WOOD	PAINTED	
07-2	Interior	3' - 0"	7' - 0"	GLASS	NONE	CLEAR	SHOWER DOOR HARDWARE
08-1	Interior	3' - 0"	7' - 0"	WOOD (SOLID-CORE)	WOOD	PAINTED	
09-1	Interior	3' - 0"	7' - 0"	WOOD (SOLID-CORE)	WOOD	PAINTED	
09-2	Interior	4' - 0"	7' - 0"	WOOD (SOLID-CORE)	WOOD	PAINTED	
10-1	Interior	3' - 0"	7' - 0"	WOOD (SOLID-CORE)	WOOD	PAINTED	
12-1	Interior	3' - 0"	7' - 0"	WOOD (SOLID-CORE)	WOOD	PAINTED	
13-1	Interior	3' - 0"	7' - 0"	WOOD (SOLID-CORE)	WOOD	PAINTED	
13-2	Interior	4' - 0"	7' - 0"	WOOD (SOLID-CORE)	WOOD	PAINTED	
13-3	Interior	6' - 0"	7' - 0"	WOOD (SOLID-CORE)	WOOD	PAINTED	
14-1	Interior	1' -10"	7' - 0"	WOOD (SOLID-CORE)	WOOD	PAINTED	
15-1	Exterior	18' - 0"	8' - 0"	METAL	WOOD	PAINTED	GARAGE DOOR HARDWARE
16-1	Interior	3' - 0"	7' - 0"	WOOD (SOLID-CORE)	WOOD	PAINTED	
16-2	Interior	2' - 6"	7' - 0"	WOOD (SOLID-CORE)	WOOD	PAINTED	
17-1	Interior	3' - 0"	7' - 0"	WOOD (SOLID-CORE)	WOOD	PAINTED	
18-1	Interior	3' - 0"	7' - 0"	WOOD (SOLID-CORE)	WOOD	PAINTED	
18-2	Interior	3' - 0"	6' - 0"	GLASS	NONE	CLEAR	SHOWER DOOR HARDWARE
19-1	Interior	3' - 0"	7' - 0"	WOOD (SOLID-CORE)	WOOD	PAINTED	
20-1	Interior	3' - 0"	7' - 0"	WOOD (SOLID-CORE)	WOOD	PAINTED	
21-1	Exterior	5' - 0"	5' - 0"	METAL	HOLLOW METAL	PAINTED	CRAWL SPACE DOOR HARDWARE
22-1	Exterior	3' - 0"	4' - 0"	WOOD, CABLE	WOOD	STAINED	GATE LATCH HARDWARE
22-2	Exterior	3' - 0"	4' - 0"	WOOD, CABLE	WOOD	STAINED	GATE LATCH HARDWARE

NOTES
1. DOORS FRAMED 6" OFF OF WALL FRAMING TYP UNLESS DIMENSIONED

ROOM FINISH SCHEDULE								
NAME	ROOM NAME	FLOOR	BASE	WALLS				COMMENTS
				NORTH	EAST	SOUTH	WEST	
01	Entry Hall	F-2	B-2	-	P-1	-	WD-1	
02	Living Room	F-1	B-1	P-1	P-1	P-1	-	
03	Dining Room	F-1	B-1	-	-	P-1	P-1	
04	Kitchen	F-1	B-1	P-1	-	-	P-1	
05	South Hallway	F-1	B-1	P-1	-	P-1	-	
06	Master Bedroom	F-1	B-1	P-1	P-1	P-1	P-1	
07	Master Bathroom	F-2	B-1	P-1	P-1	P-1	P-1	FOR SHOWER FINISHES SEE 6/ A7.02
08	Master Closet	F-4	B-1	P-1	P-1	P-1	P-1	
09	Second Bedroom	F-1	B-1	P-1	P-1	P-1	P-1	
10	Reading Nook	F-1	-	WD-1	WD-1	WD-1	-	
11	Bathroom	F-2	B-1	T-1	P-1	P-1	P-1	FOR SHOWER FINISHES SEE 3/ A7.02
12	Laundry Room	F-2	B-1	P-1	P-1	P-1	P-1	
13	Office	F-1	B-1	P-1	P-1	P-1	P-1	
14	Powder Room	F-4	B-1	P-1	P-1	P-1	P-1	
15	Garage	F-5	B-1	P-1	P-1	P-1	P-1	
16	North Hallway	F-1	B-1	P-1	P-1	P-1	P-1	
17	Guest Bedroom	F-1	B-1	P-1	P-1	P-1	P-1	
18	Guest Bathroom	F-2	B-1	P-1	P-1	P-1	P-1	FOR SHOWER FINISHES SEE 5/ A7.02
19	Guest Closet	F-1	B-1	P-1	P-1	P-1	P-1	
20	Attic	Plywood Sheathing	-	Unfinished	Unfinished	Unfinished	Unfinished	

Appliance Schedule		
SYM.	Location	Description

A1	04 - Kitchen	Refrigerator
A2	04 - Kitchen	Dishwasher
A3	04 - Kitchen	Oven
A4	04 - Kitchen	Cooktop
A5	04 - Kitchen	Hood
A6	12 - Laundry Room	Washer
A7	12 - Laundry Room	Dryer

NOTES
1. SEE SPECS FOR FINISH DESCRIPTIONS
2. SEE SPECS FOR APPLIANCE MODELS